


町道(道路敷=広川町名義) ※42条認定確認中 ― 北面は道路際・出入口なし(顔=会議室大窓+サイン帯)

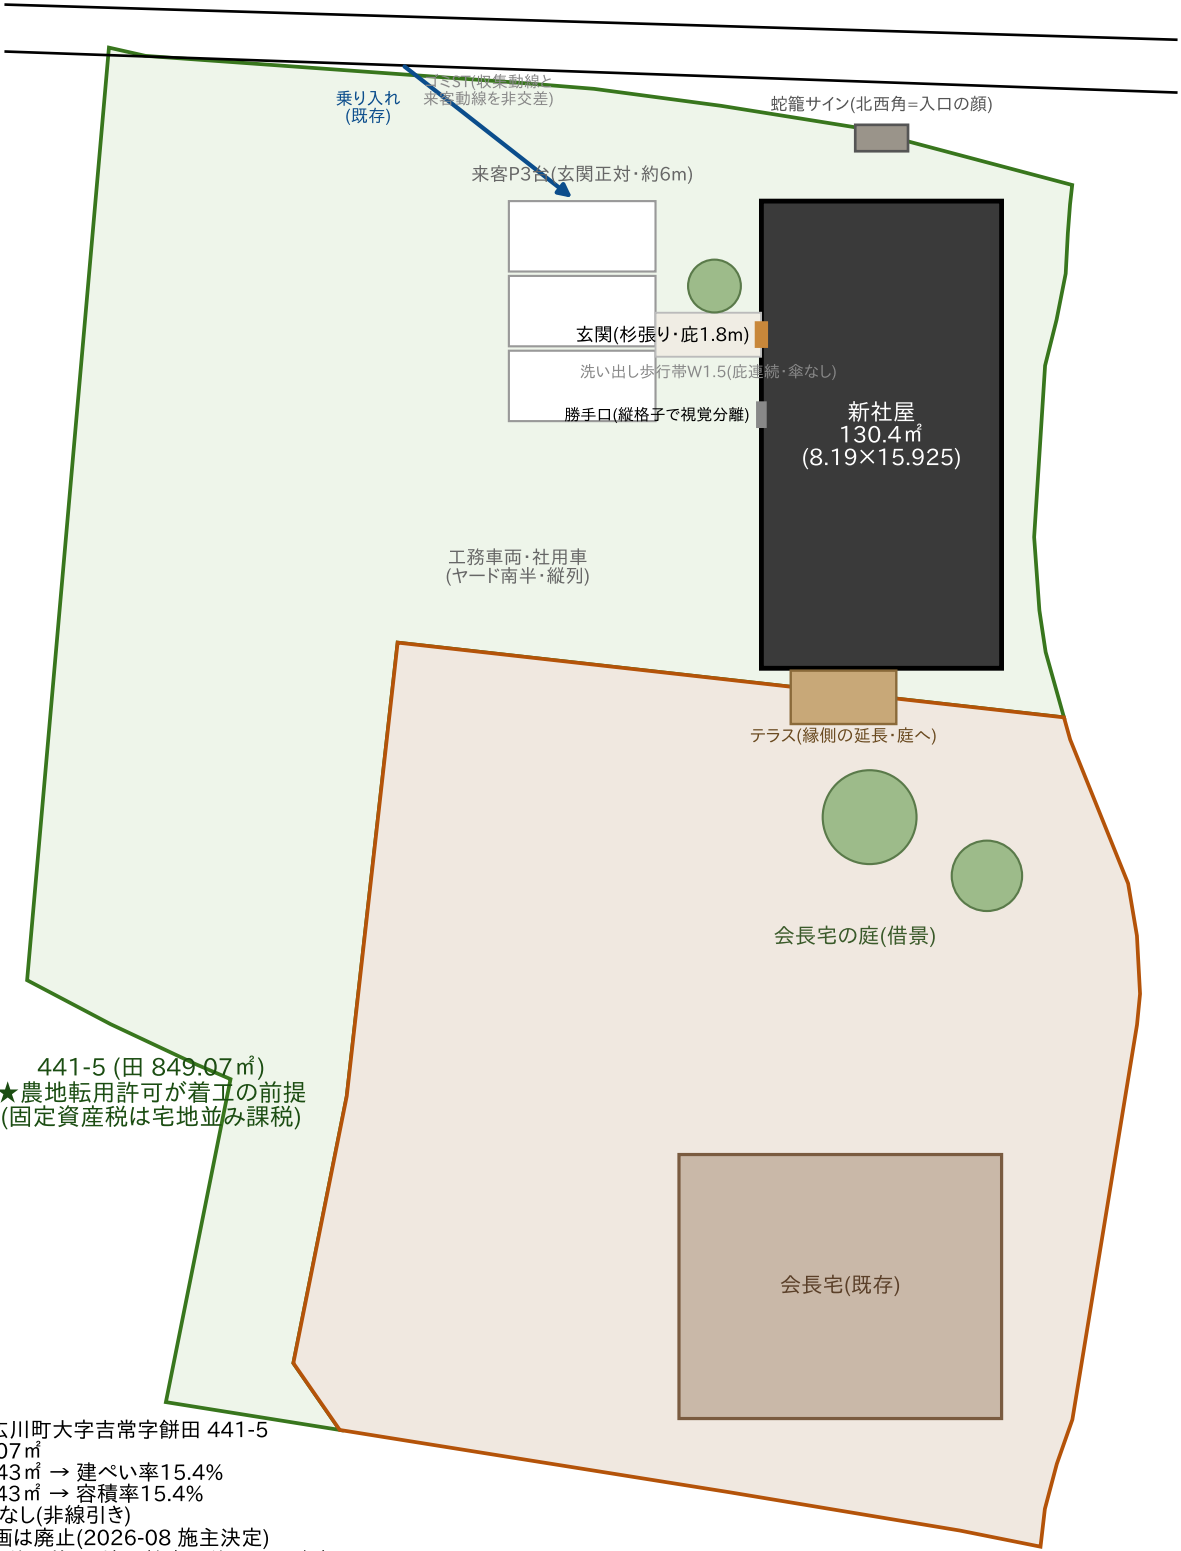


生垣・水路 → 隣地(友野氏・駐車場)

441-5 (田 849.07㎡)
★農地転用許可が着工の前提
(固定資産税は宅地並み課税)

【敷地】八女郡広川町大字吉常字餅田 441-5
敷地面積 849.07㎡
建築面積 130.43㎡ → 建ぺい率15.4%
延べ面積 130.43㎡ → 容積率15.4%
用途地域: 指定なし(非線引き)
※GYM増築計画は廃止(2026-08 施主決定)
※農地転用許可後に着工/境界杭実測後に配置確定

樋口工業有限会社 新小屋新築工事「北に顔、西に口、南に縁」	
図面名: 配置図	A-01
縮尺 1/250・2026-08-19・計画案v7(たたき台)	

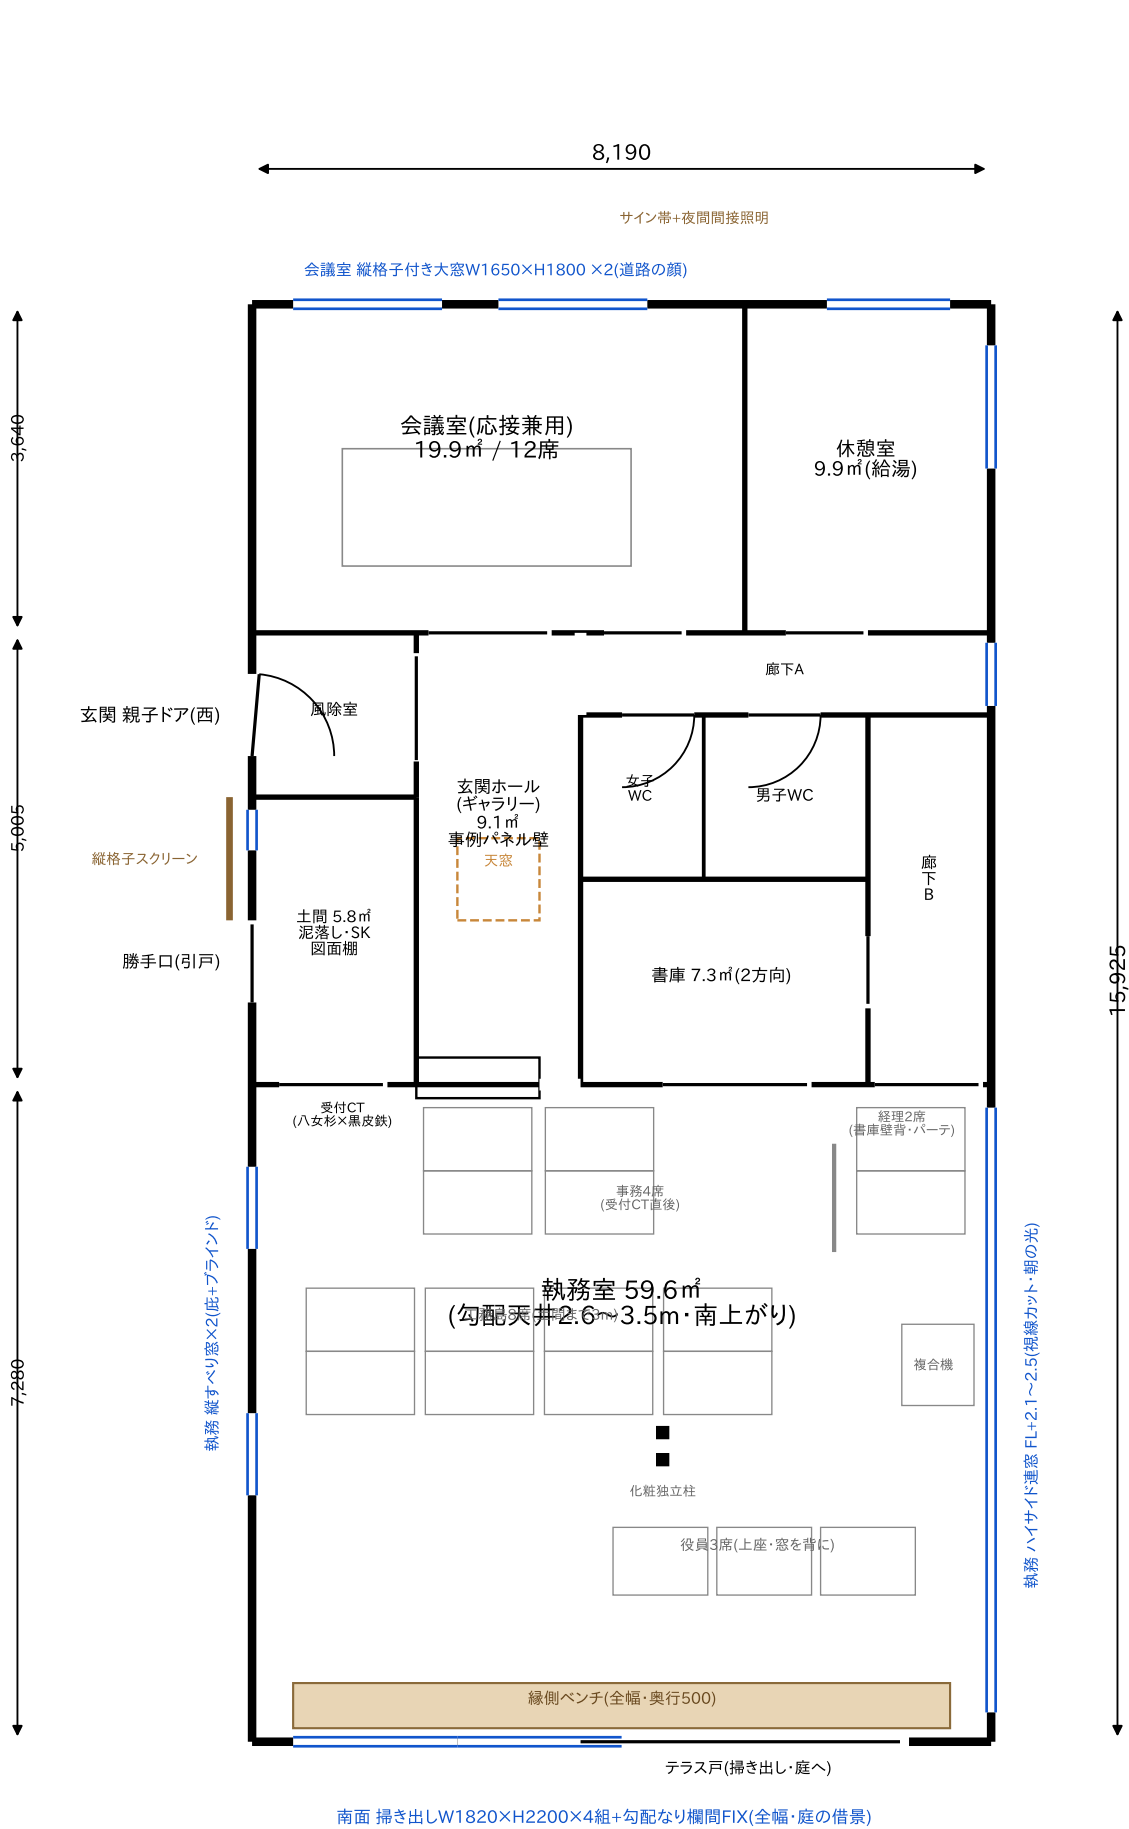


- 【v7「北に顔、西に口、南に縁」の要点】
- ・玄関=西面: 来客P(西ヤード北半・玄関正対6m)から洗い出し歩行帯+庇1.8mで傘なしアプローチ
 - ・北面=道路際のため出入口なし。会議室大窓×2+サイン帯の「顔」
 - ・玄関ホールは南北のギャラリー: 北端=会議室、南端=受付CT。来客動線は廊下ゼロ(玄関→ホール→会議室)
 - ・来客WC: ホール脇開口から2〜3m(ドアは死角)。
 - ・社員は執務→廊下B→廊下Aでホール不通過
 - ・勝手口は玄関と1.8m離隔+縦格子で泥動線を視覚分離。土間→工務島3m。ゴミは土間経由一方
 - ・お茶出し: 休憩→廊下A→会議室3m(執務・ホール不通過)
 - ・経理は書庫壁を背に+バーテ(受付の視軸から完全に外れる)
 - ・執務室59.6㎡: 南全幅開口+縁側ベンチ+東ハイサイド+勾配天井2.6→3.5m=庭に向かって開く
 - ・天窓: ギャラリーホール中央に910角
 - ・GYM増築は廃止(制約なし・西面全面自由)


【面積表(壁芯)】
延べ面積 130.43㎡ (39.5坪)
会議19.9/休憩9.9/風除3.3/ホール9.1/廊下A4.1
女WC2.5/男WC3.3/廊下B5.6/土間5.8/書庫7.3/執務59.6
※敷地(441-5)は農地転用許可後に着工




樋口工業有限会社 新社屋新築工事「北に顔、西に口、南に縁」	
図面名: 平面図	A-02
縮尺 1/100・2026-08-19・計画案v7(たたき台)	

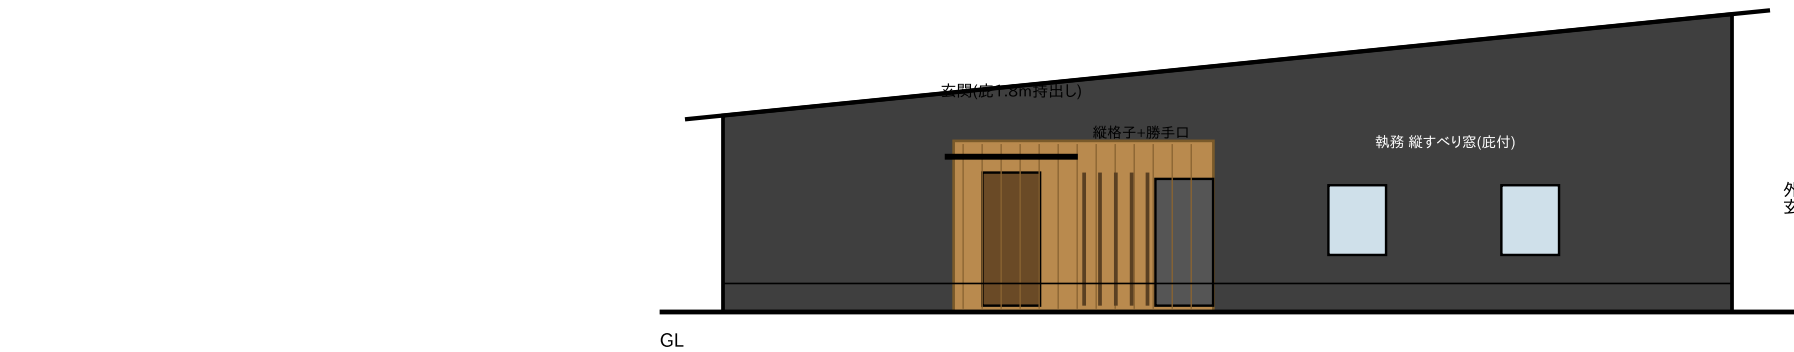


西立面図(駐車場・アプローチ側=入口の顔) 1/150

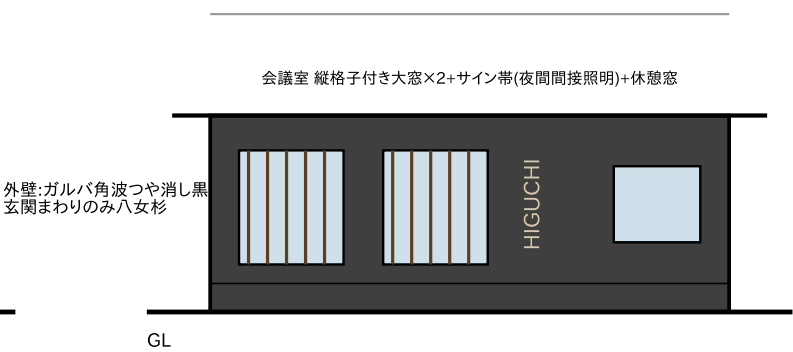


北立面図(道路の顔・出入口なし) 1/150

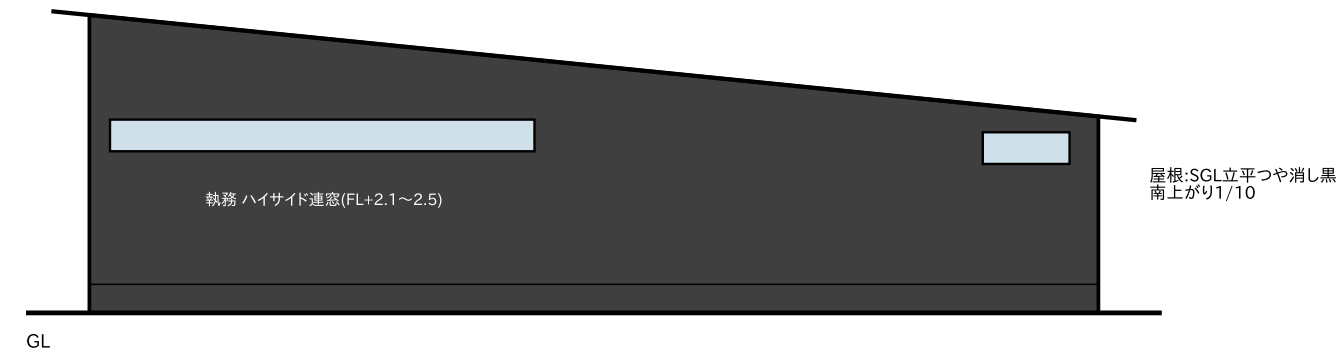

東立面図(生垣・水路側) 1/150

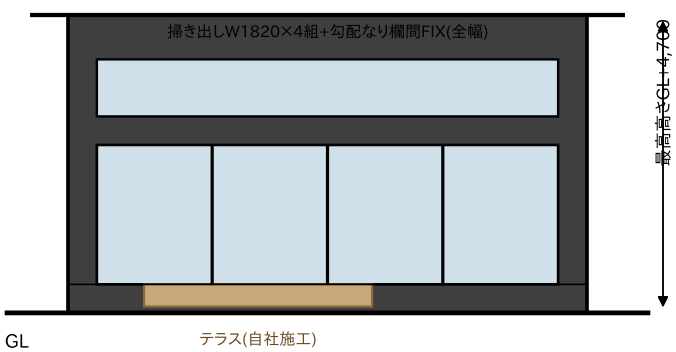

南立面図(庭・借景側) 1/150

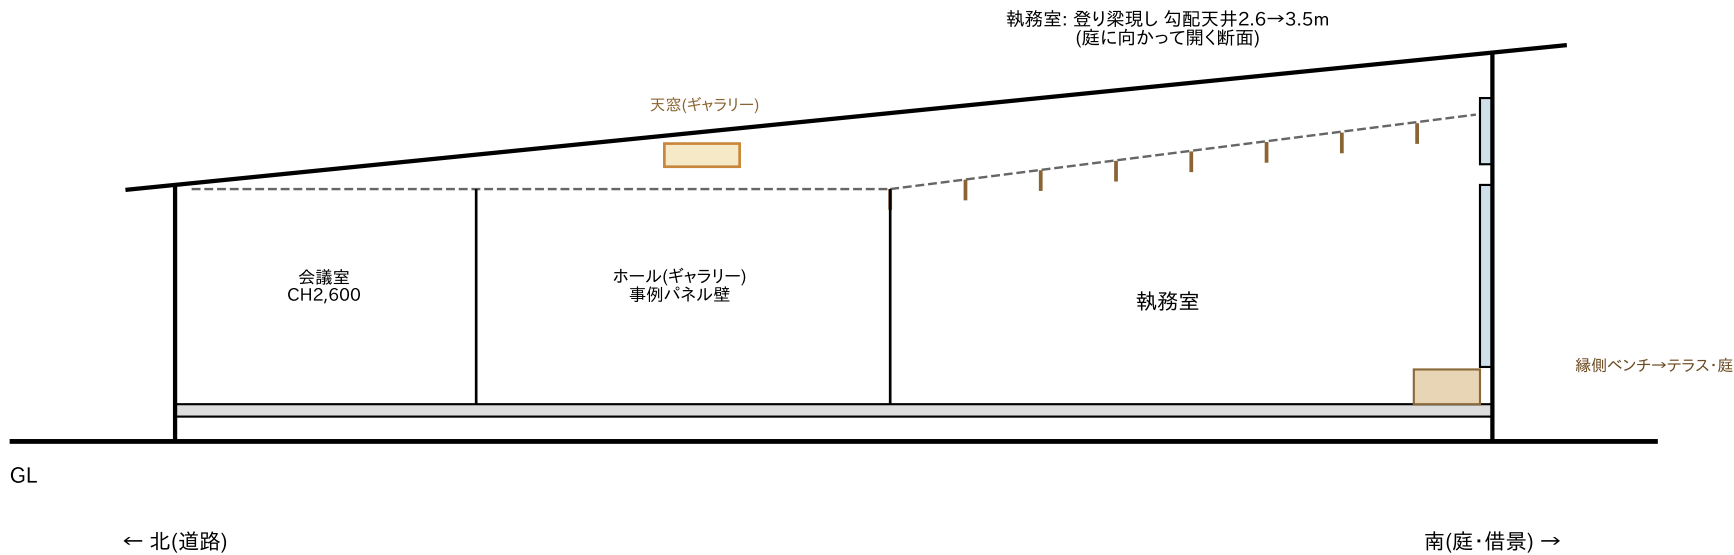


【構造・仕上概要(v7)】
構造: 木造在来・平屋(8.19×15.925m) / 基礎: ベタ基礎 / 壁量: 2025年改正基準(南面全幅開口の耐力は書庫・WC回り耐力壁+執務内化粧独立柱x=4.55で補完・要壁量計算)
屋根: SGLガルバ立平つや消し黒・南上がり1/10 / 外壁: ガルバ角波つや消し黒+西面玄関まわりのみ八女杉(艶は全部消し・3色で止める)
サッシ: アルミ樹脂複合 黒 / 断熱: 屋根HGW16K155×2・壁HGW16K105・基礎XPS50 / 天窗: FIX断熱型910角
内装: 執務=構造現し+腰壁合板クリア+タイルカーペット / 会議=杉板1面壁+素材見本棚 / ホール=モルタル金鏝+施工事例パネル+八女杉受付CT(自社鉄工脚)
外構(自社施工=原価): 舗装+白線・洗い出し歩行帯W1.5・蛇籠サイン(北西角)・アオダモ・テラス・電球色2700K
設備: 24h換気(3種) / エアコン執務2・会議1 / LAN Cat6A / 給排水は土間系+WC系の2系統
※GYM増築計画は廃止(2026-08施主決定) ※屋根は北流れ=太陽光不向き ※建設地(441-5)は農地転用許可が前提 ※最終確認は設計者(建築士)による

外観イメージ(北西=駐車場側から)

「黒い箱に、八女杉の切り欠き」

- ・車を降りると正面に杉張りの玄関(庇1.8m・傘なし6m)
- ・左手前=蛇籠サイン(八女石+切文字)、玄関脇にアオダモ
- ・道路側(左奥)は会議室の格子窓+サイン帯の「顔」
- ・屋根は南(右)へ伸び上がる: 庭に向かって開く断面
- ・縦格子の奥が勝手口: 泥動線は視覚分離
- ・白線ピシッの駐車場・洗い出しの白い帯=自社施工の名刺
- ・夜は電球色2700K: ポーチ・蛇籠・アオダモだけ照らす

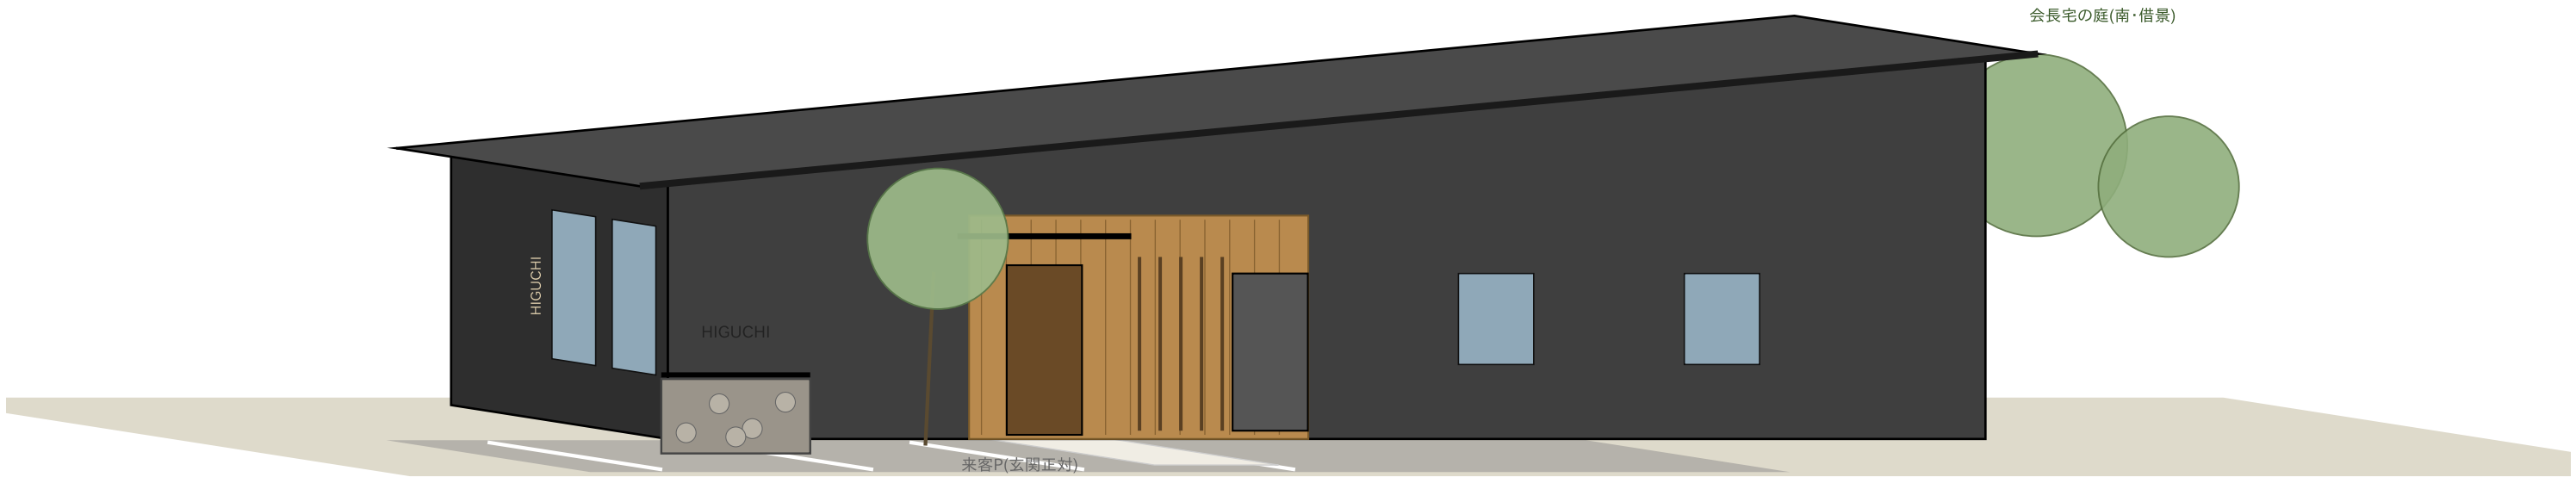

樋口工業有限会社 新社屋新築工事「北に顔、西に口、南に縁」

図面名: 外観イメージ

A-05

縮尺 NTS・2026-08-19・計画案v7(たたき台)