




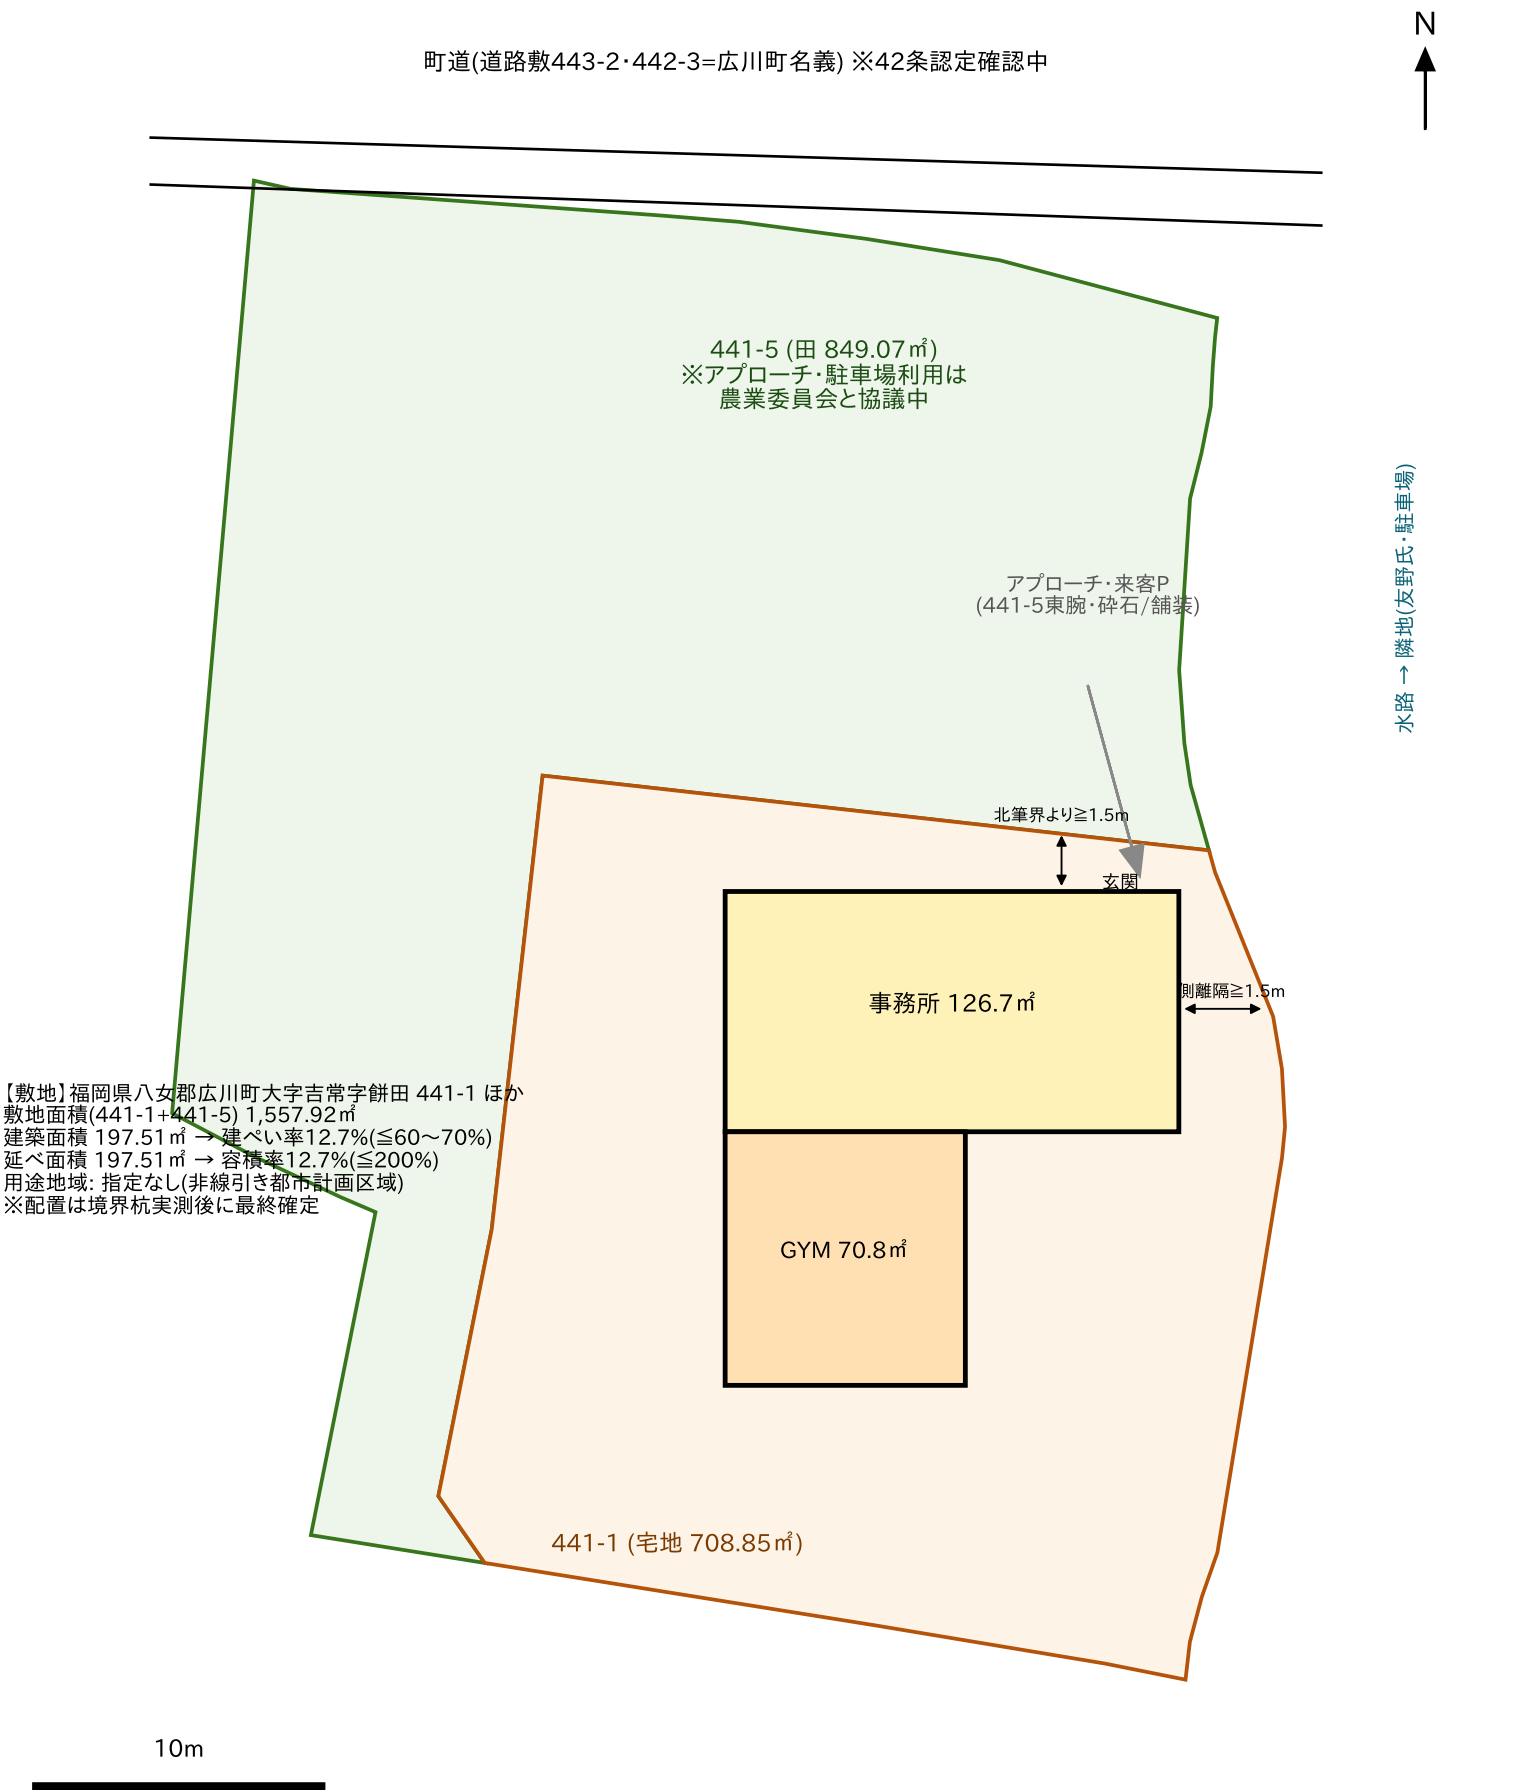


樋口工業有限会社 新社屋(事務所・GYM棟)新築工事	
図面名: 配置図	A-01
縮尺 1/250・2026-08-19・計画案(たたき台)	

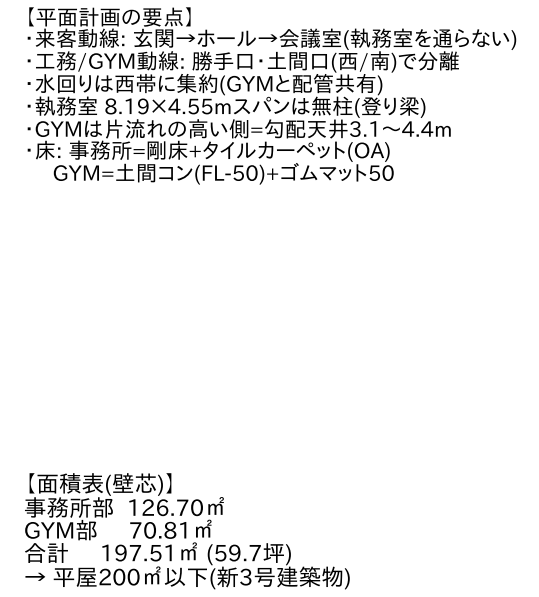


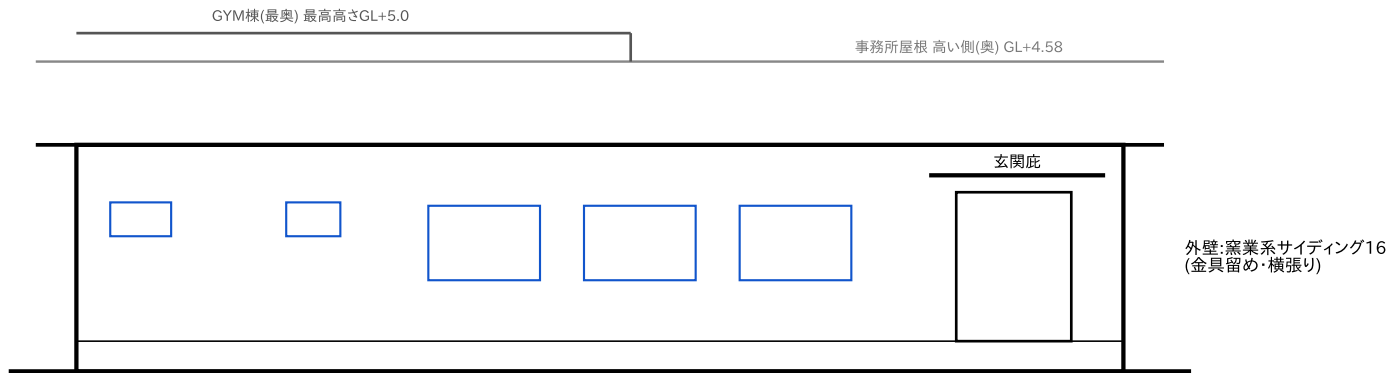


北立面図(道路側) 1/150

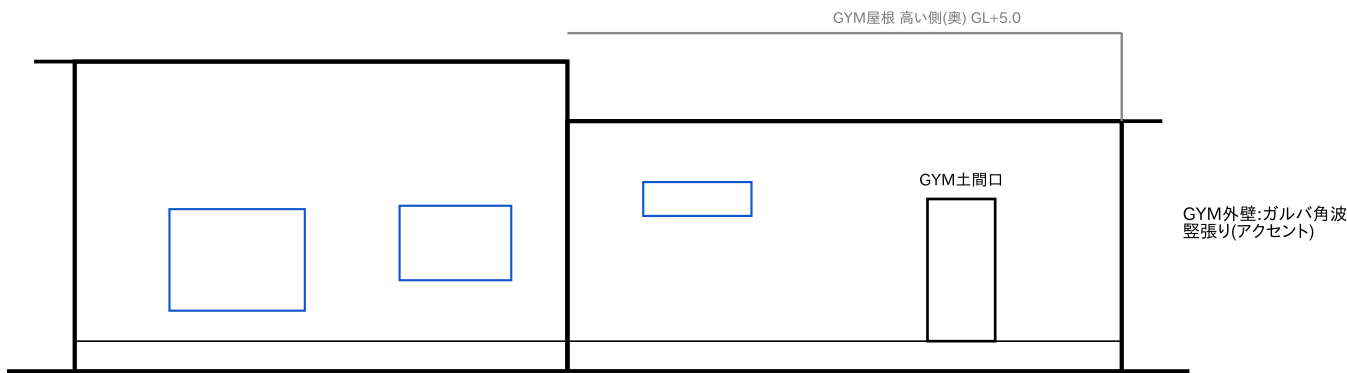

南立面図 1/150

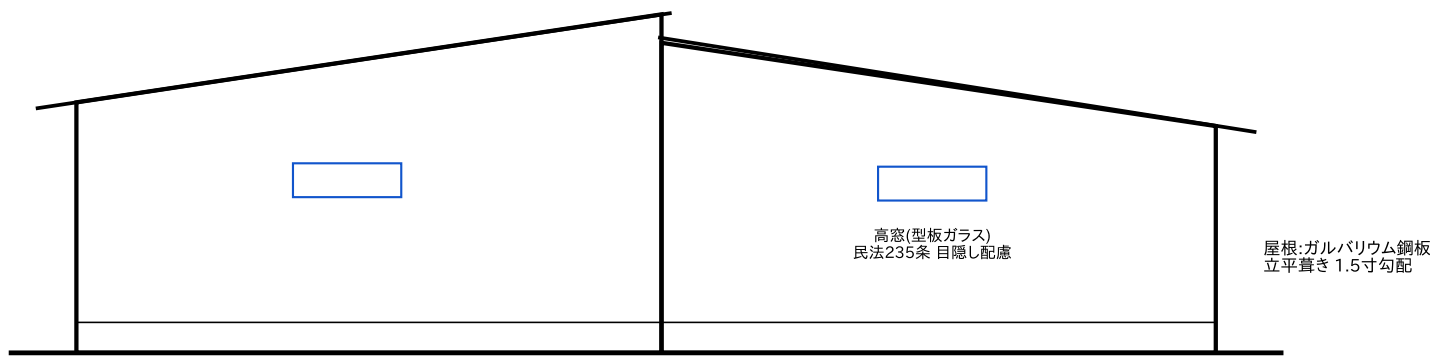


(GYM東面は事務所面より7.3m奥) 東立面図(水路側) 1/150

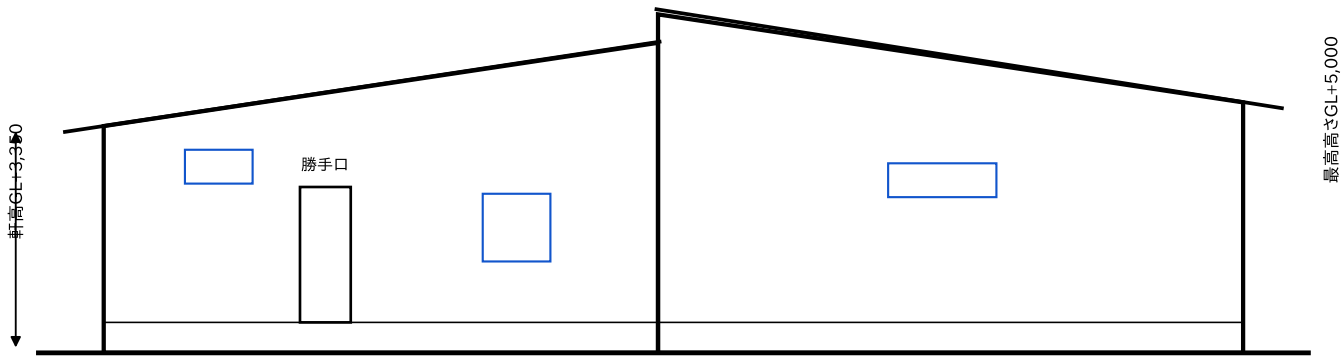

西立面図(ヤード側) 1/150

樋口工業有限会社 新社屋(事務所・GYM棟)新築工事	
図面名: 断面図・仕様概要	A-04
縮尺 1/60・2026-08-19・計画案(たたき台)	

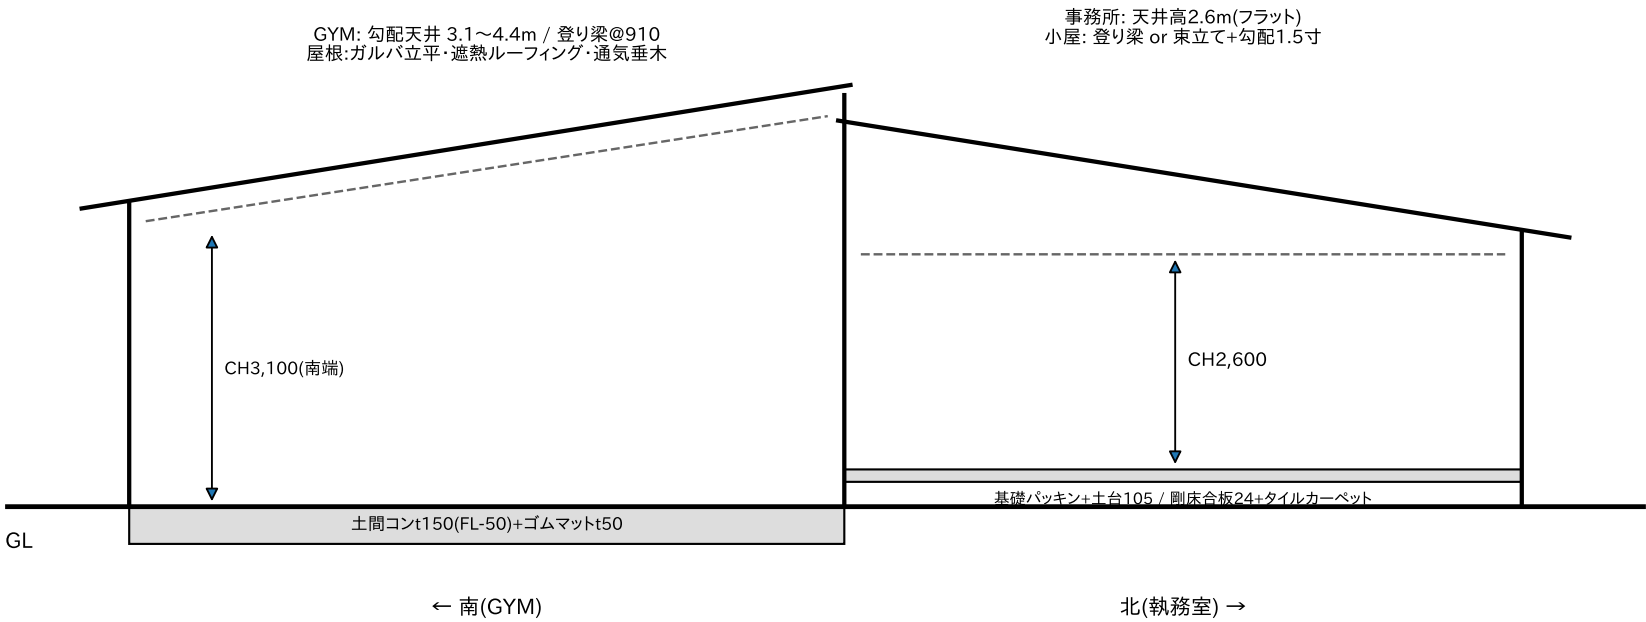

A-A断面図(南北) 1/60 ※雨仕舞い: GYM高壁と事務所低軒の取り合いは雨押え板金・両屋根とも接合部から離れる方向に排水

【構造・仕上概要(たたき台)】

構造: 木造在来軸組・平屋 / 基礎: ベタ基礎(GYM部は土間一体・機材アンカー対応配筋)
壁量: 2025年改正基準による壁量計算(構造用合板9mm N50@150 外周耐力壁)
屋根: ガルバリウム鋼板立平葺き1.5寸 / 軒の出600 / 太陽光はGYM南流れ屋根に搭載可(約5kW)
外壁: 窯業系サイディング16(事務所)+ガルバ角波縦張り(GYM)・通気工法
断熱: 屋根 HGW16K155×2層 / 壁 HGW16K105 / 基礎・土間 XPS50 / サッシ アルミ樹脂複合Low-E
内装: 事務所 PB12.5+塗装(AEP)・タイルカーペット / GYM 腰壁合板12(t)現し+PB・ゴムマット50
設備: 24h換気(3種)+GYM換気強化 / エアコン 執務2・会議1・GYM1 / LAN Cat6A / 照明LED
※本図は実施設計前の計画案。寸法・構造・法適合の最終確認は設計者(建築士)による。