


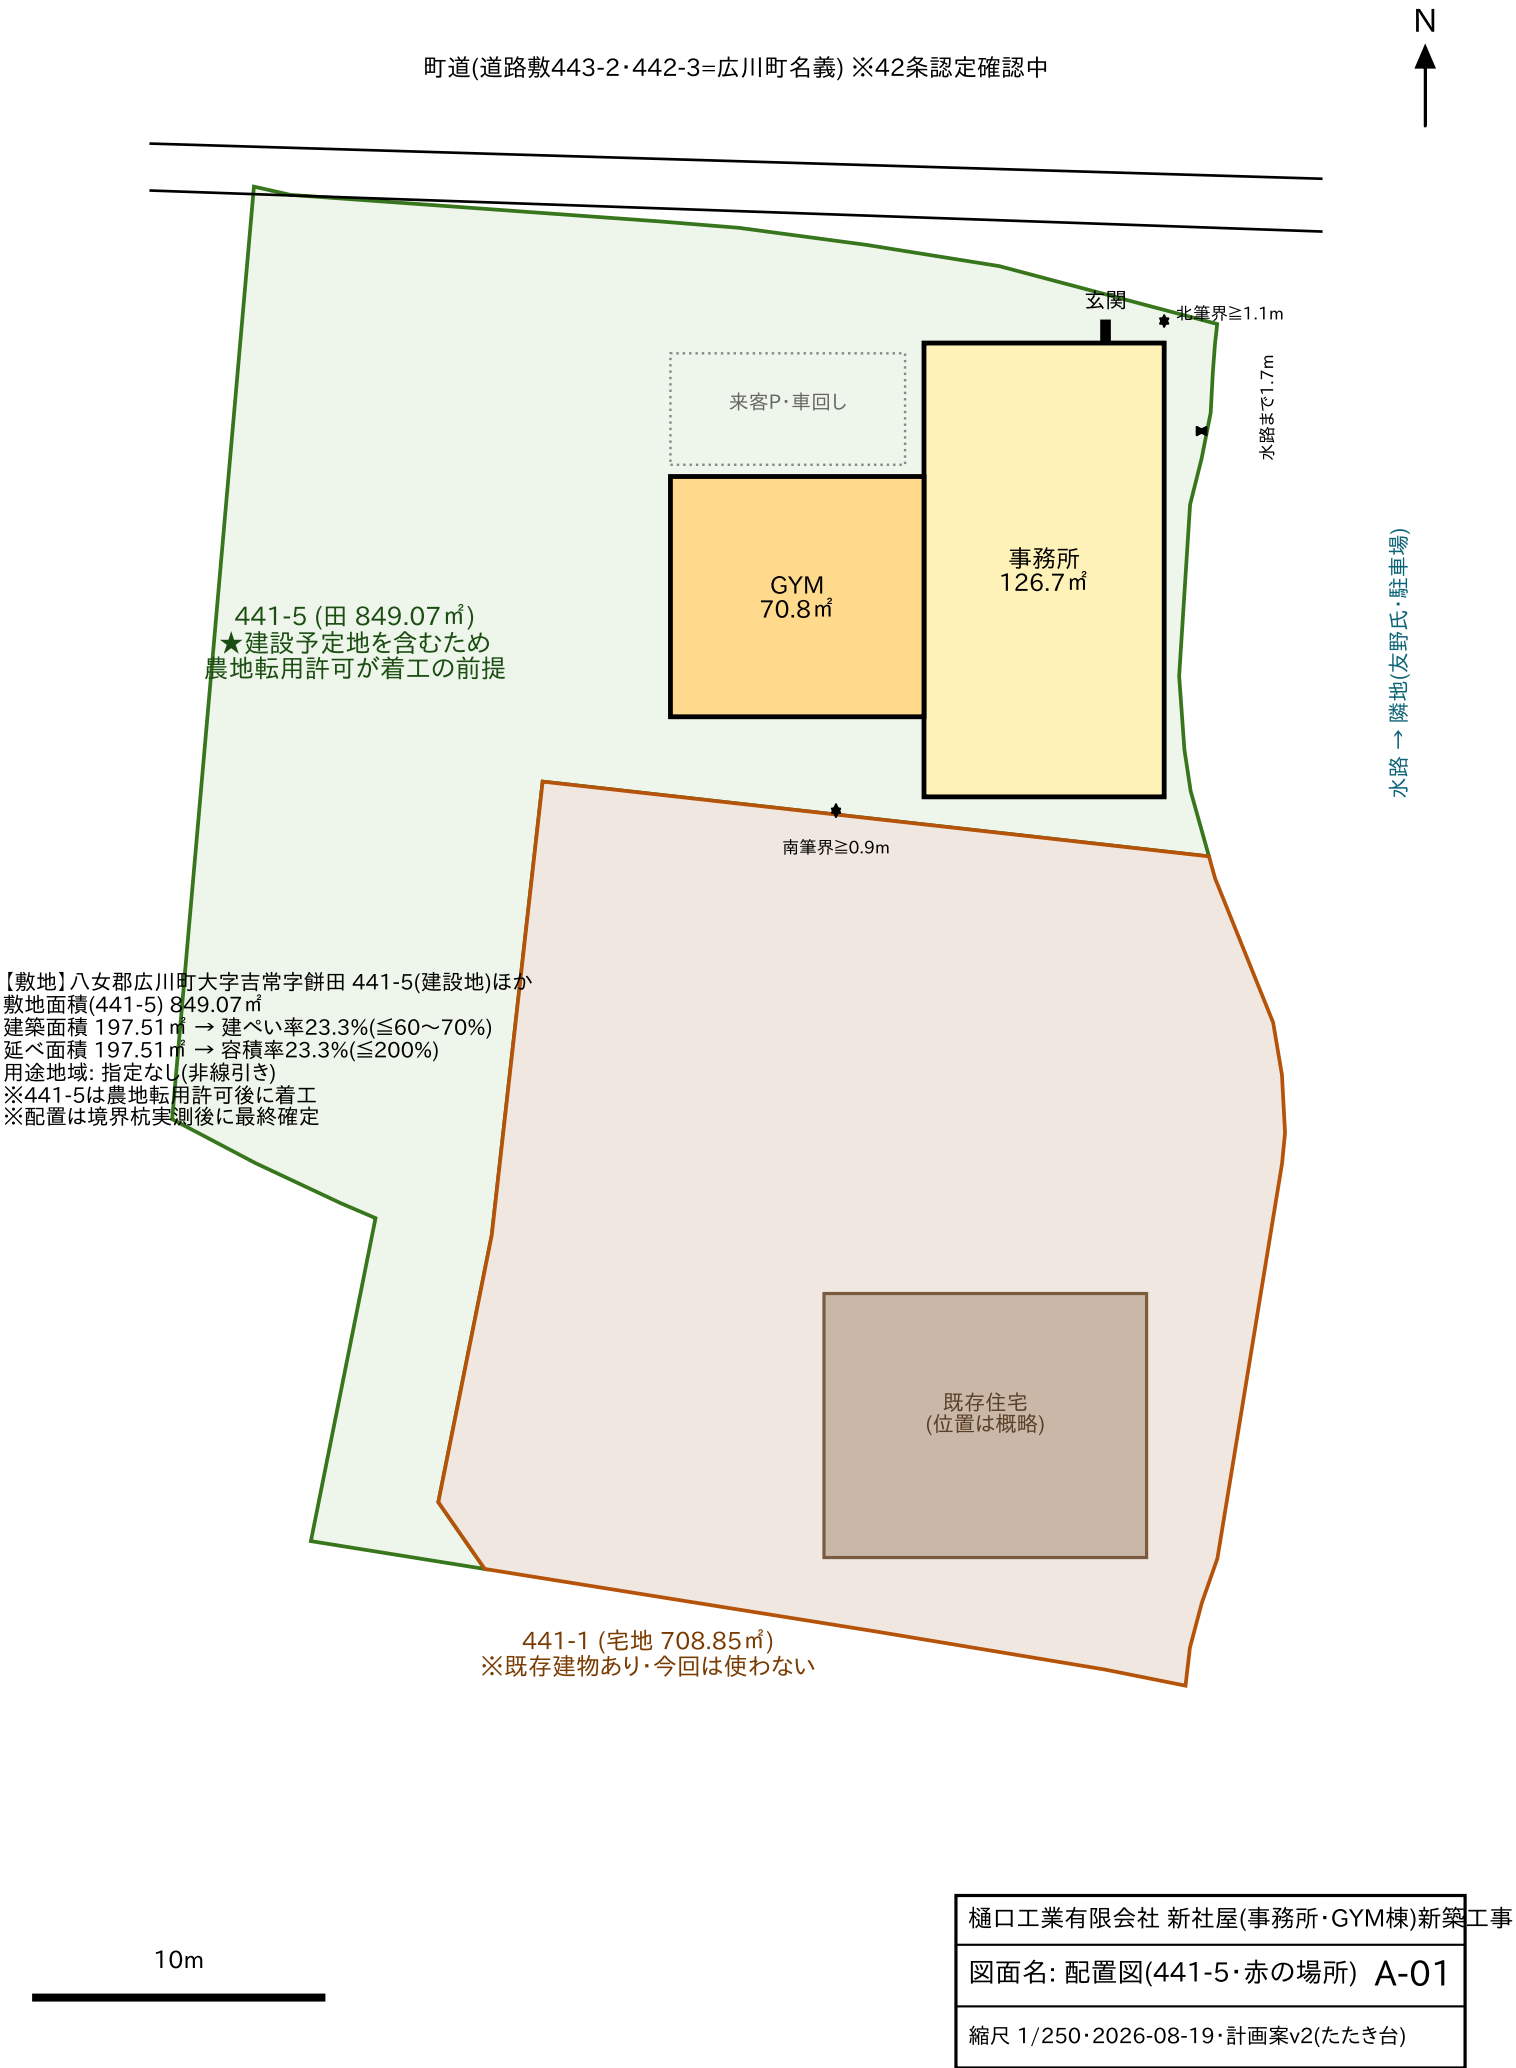





【平面計画の要点(v2=赤の場所版)】
・建物の向きを90°変更: 事務所は南北棟
玄関=北面(道路からすぐ)
・来客: 玄関→ホール→会議室(執務を通らない)
・会議室は北窓=道路側で明るい
・執務室の東窓は型板ガラス(隣地P側の視線カット)
・GYMは西側接続: 車回し・来客Pに北ポケットを確保
・水回りは南帯に集約 / 勝手口は西面(ヤード側)
・GYM: 土間コン+ゴムマット50 / 勾配天井3.1~4.4m

【面積表(壁芯)】
事務所部 126.70㎡
GYM部 70.81㎡
合計 197.51㎡ (59.7坪)
→ 平屋200㎡以下(新3号建築物)
※敷地(441-5)は農地転用許可後に着工


樋口工業有限会社 新社屋(事務所・GYM棟)新築工事	
図面名: 平面図	A-02
縮尺 1/100・2026-08-19・計画案v2(たたき台)	

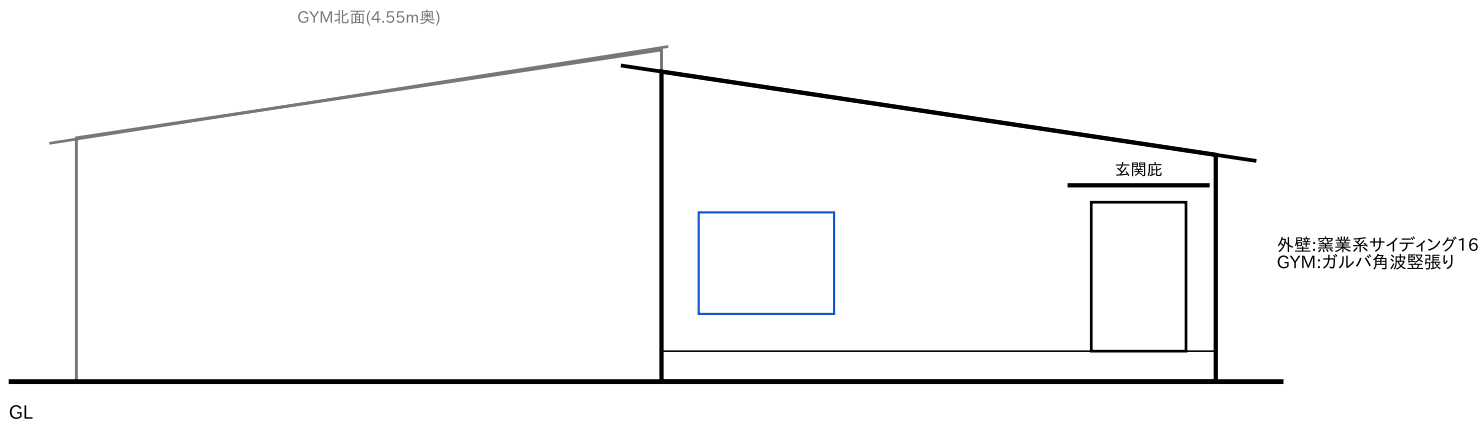


北立面図(道路側) 1/150

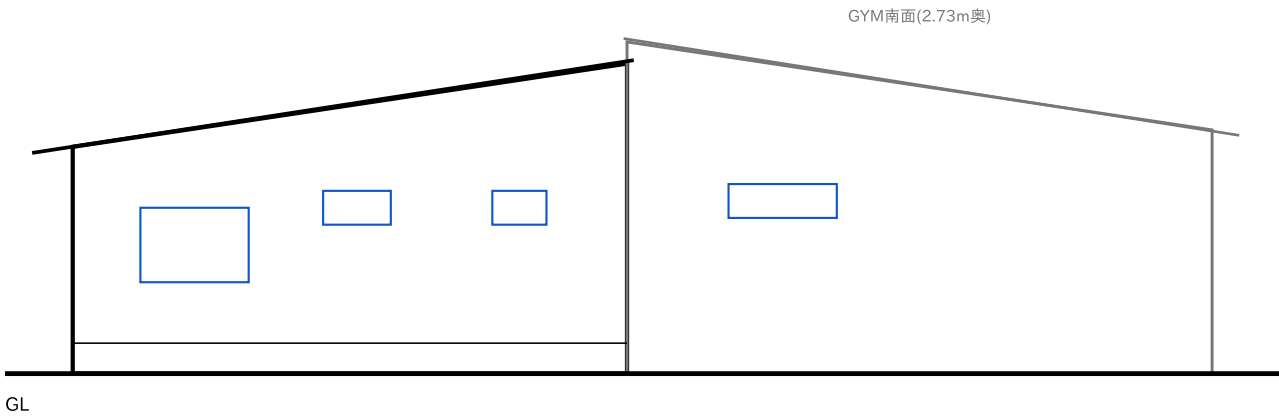

南立面図 1/150

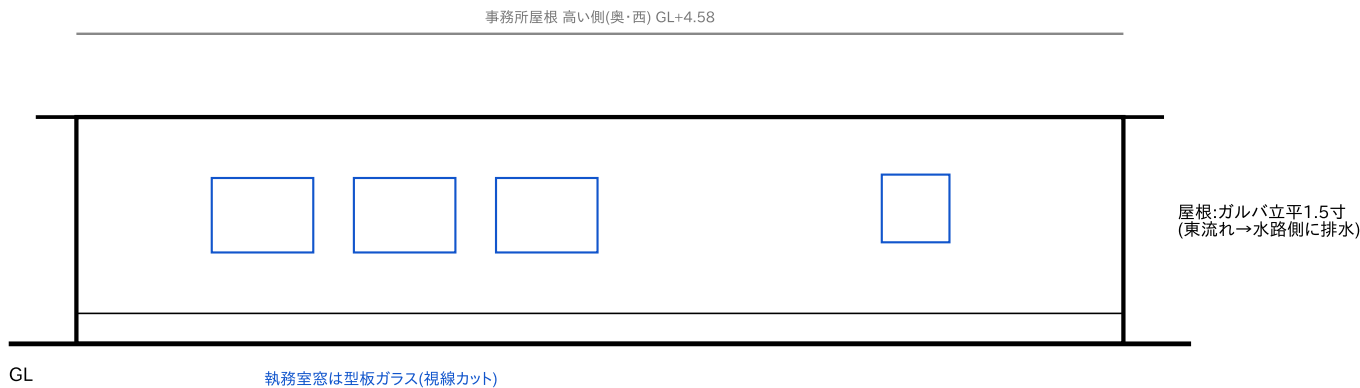


東立面図(隣地駐車場側) 1/150

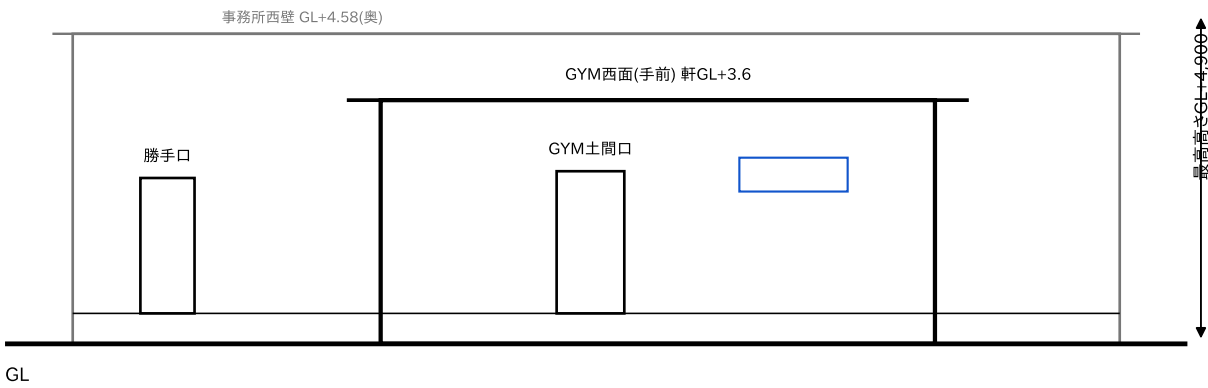

西立面図(ヤード側) 1/150

樋口工業有限会社 新社屋(事務所・GYM棟)新築工事	
図面名: 立面図(4面)	A-03
縮尺 1/150・2026-08-19・計画案v2(たたき台)	

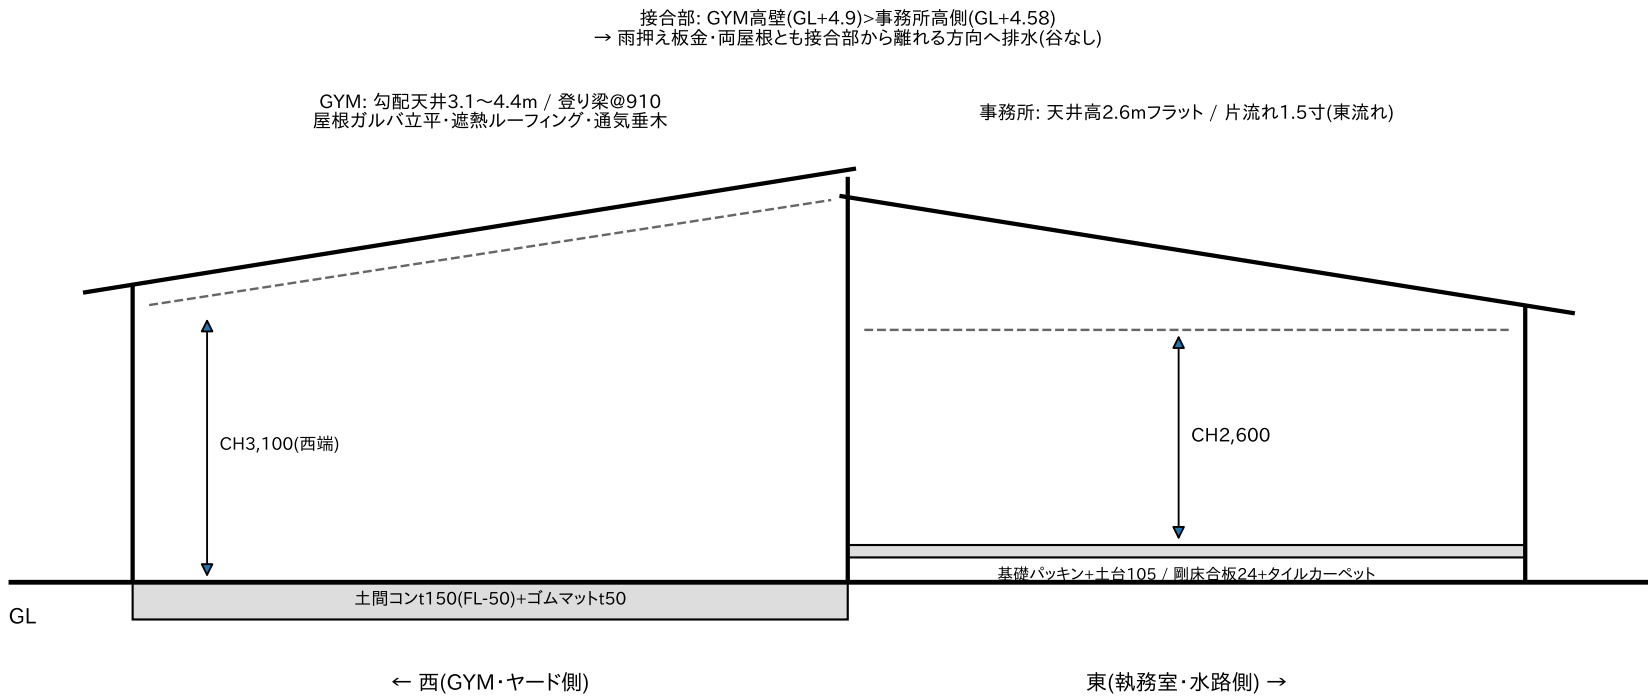

A-A断面図(東西) 1/60

【構造・仕上概要(たたき台)】

構造: 木造在来軸組・平屋 / 基礎: ベタ基礎(GYM部は土間一体・機材アンカー対応配筋)
壁量: 2025年改正基準による壁量計算(構造用合板9mm N50@150 外周耐力壁)
屋根: ガルバリウム鋼板立平葺き1.5寸 / 軒の出600 / 事務所=東流れ・GYM=西流れ
外壁: 窯業系サイディング16(事務所)+ガルバ角波縦張り(GYM)・通気工法
断熱: 屋根HGW16K155×2層 / 壁HGW16K105 / 基礎・土間XPS50 / サッシ アルミ樹脂複合Low-E
内装: 事務所 PB12.5+塗装(AEP)・タイルカーペット / GYM 腰壁合板12現し+PB・ゴムマット50
設備: 24h換気(3種)+GYM換気強化 / エアコン執務2・会議1・GYM1 / LAN Cat6A / 照明LED
※建設地(441-5)は農地転用許可が着工の前提。※本図は実施設計前の計画案。最終確認は設計者(建築士)による。

樋口工業有限会社 新社屋(事務所・GYM棟)新築工事	
図面名: 断面図・仕様概要	A-04
縮尺 1/60・2026-08-19・計画案v2(たたき台)	