




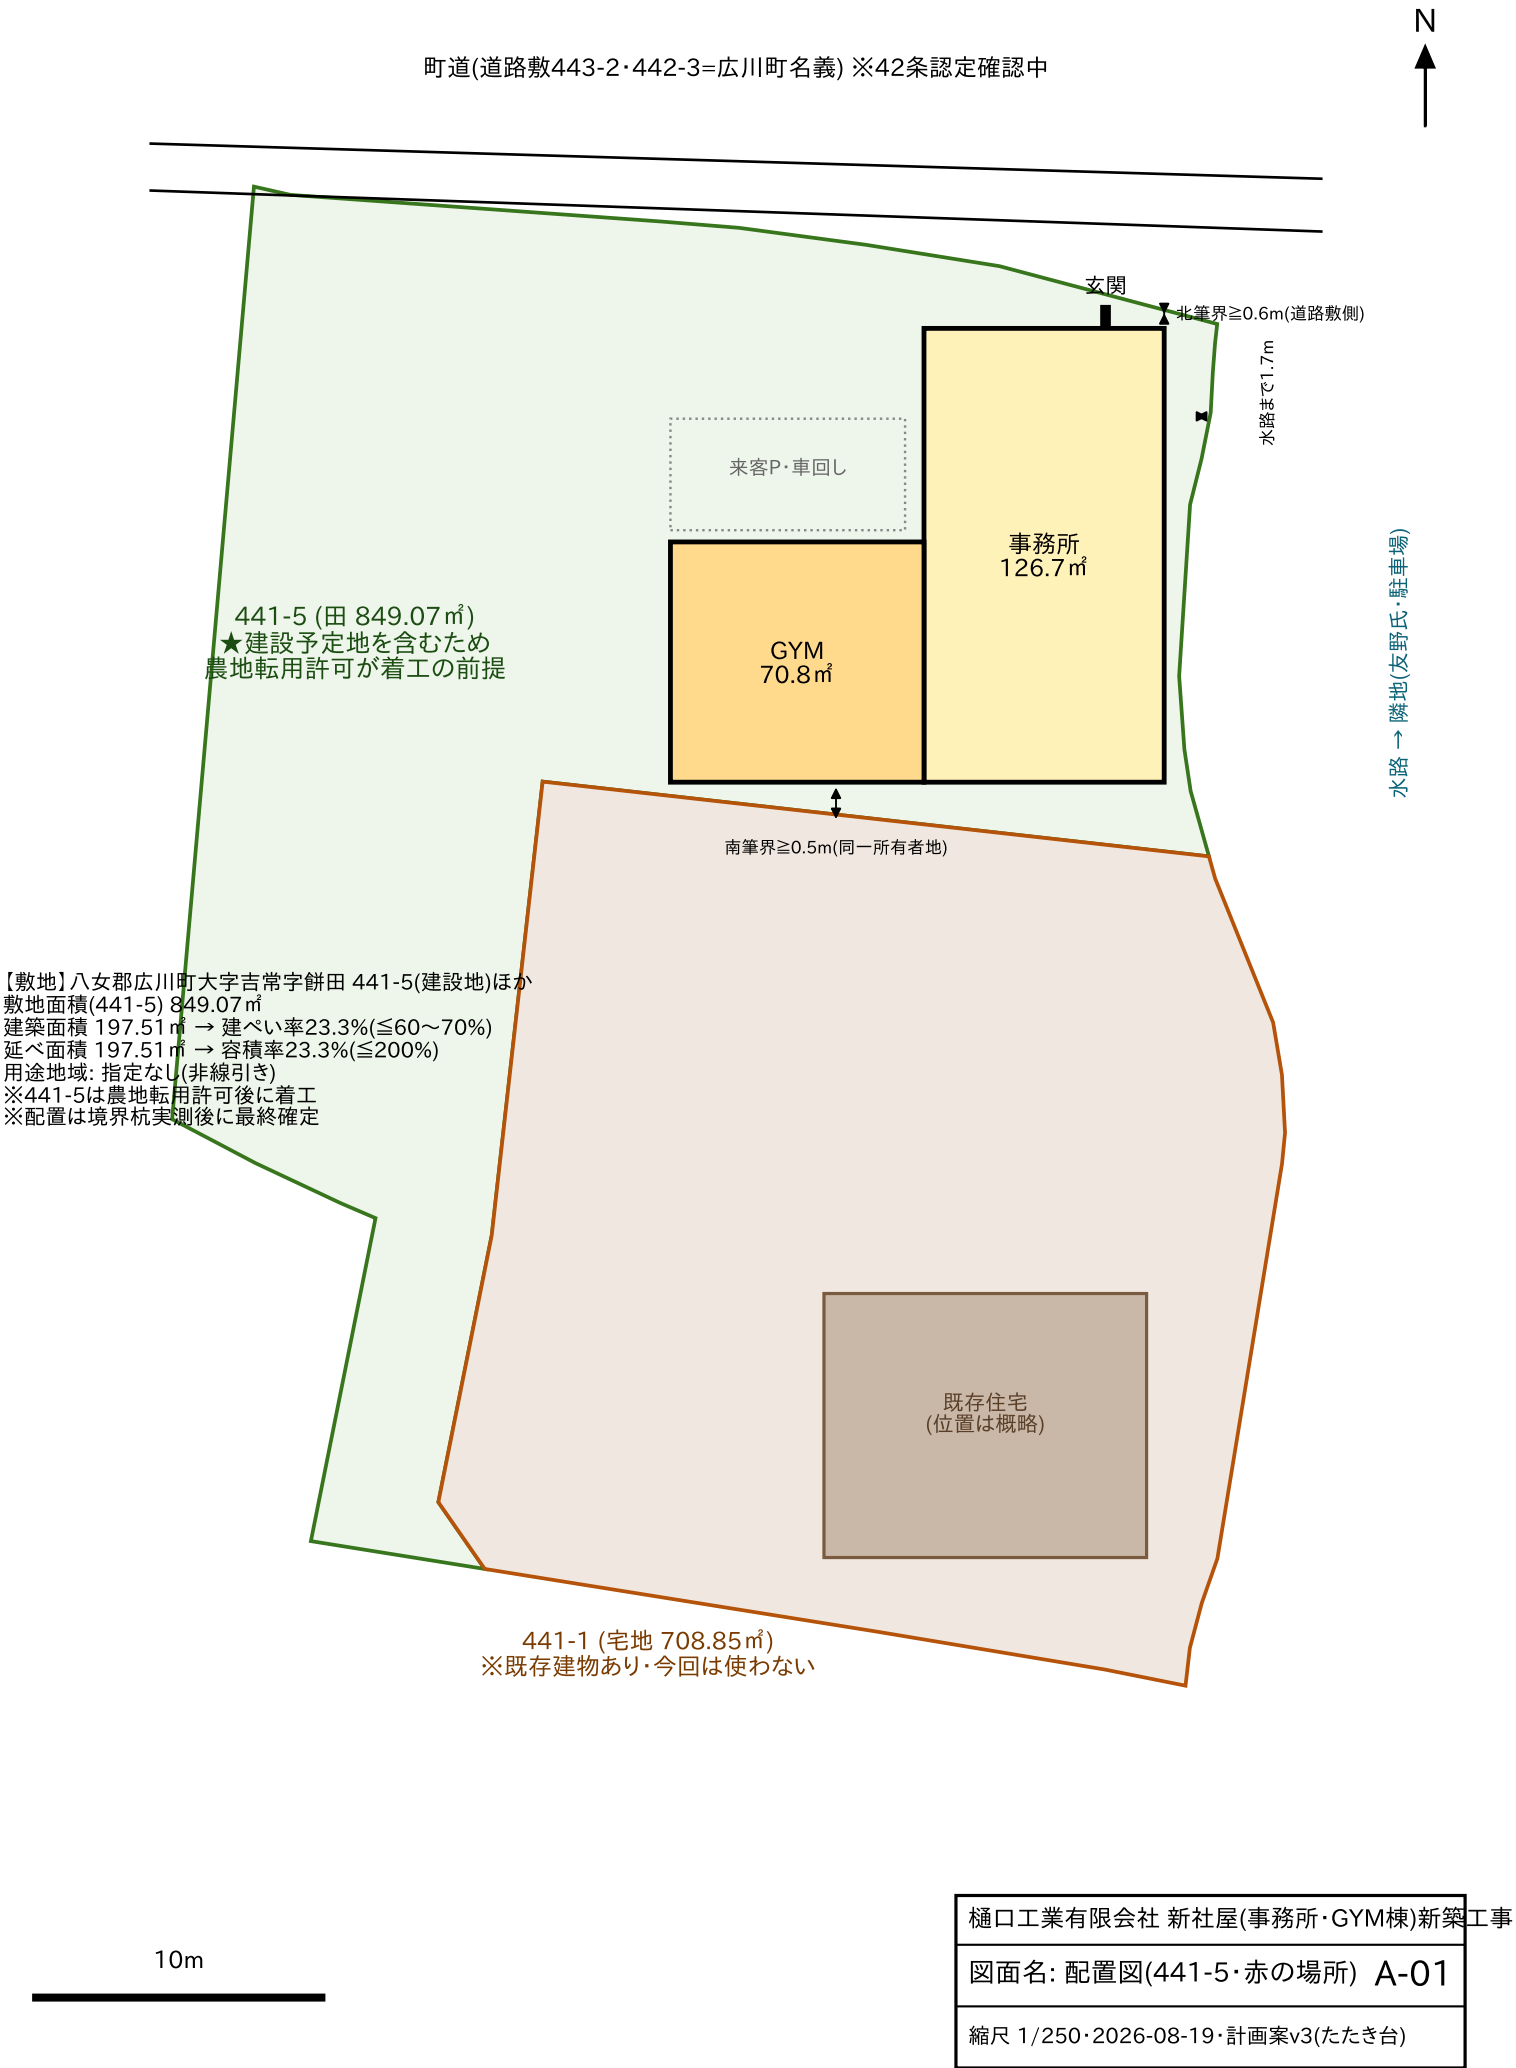


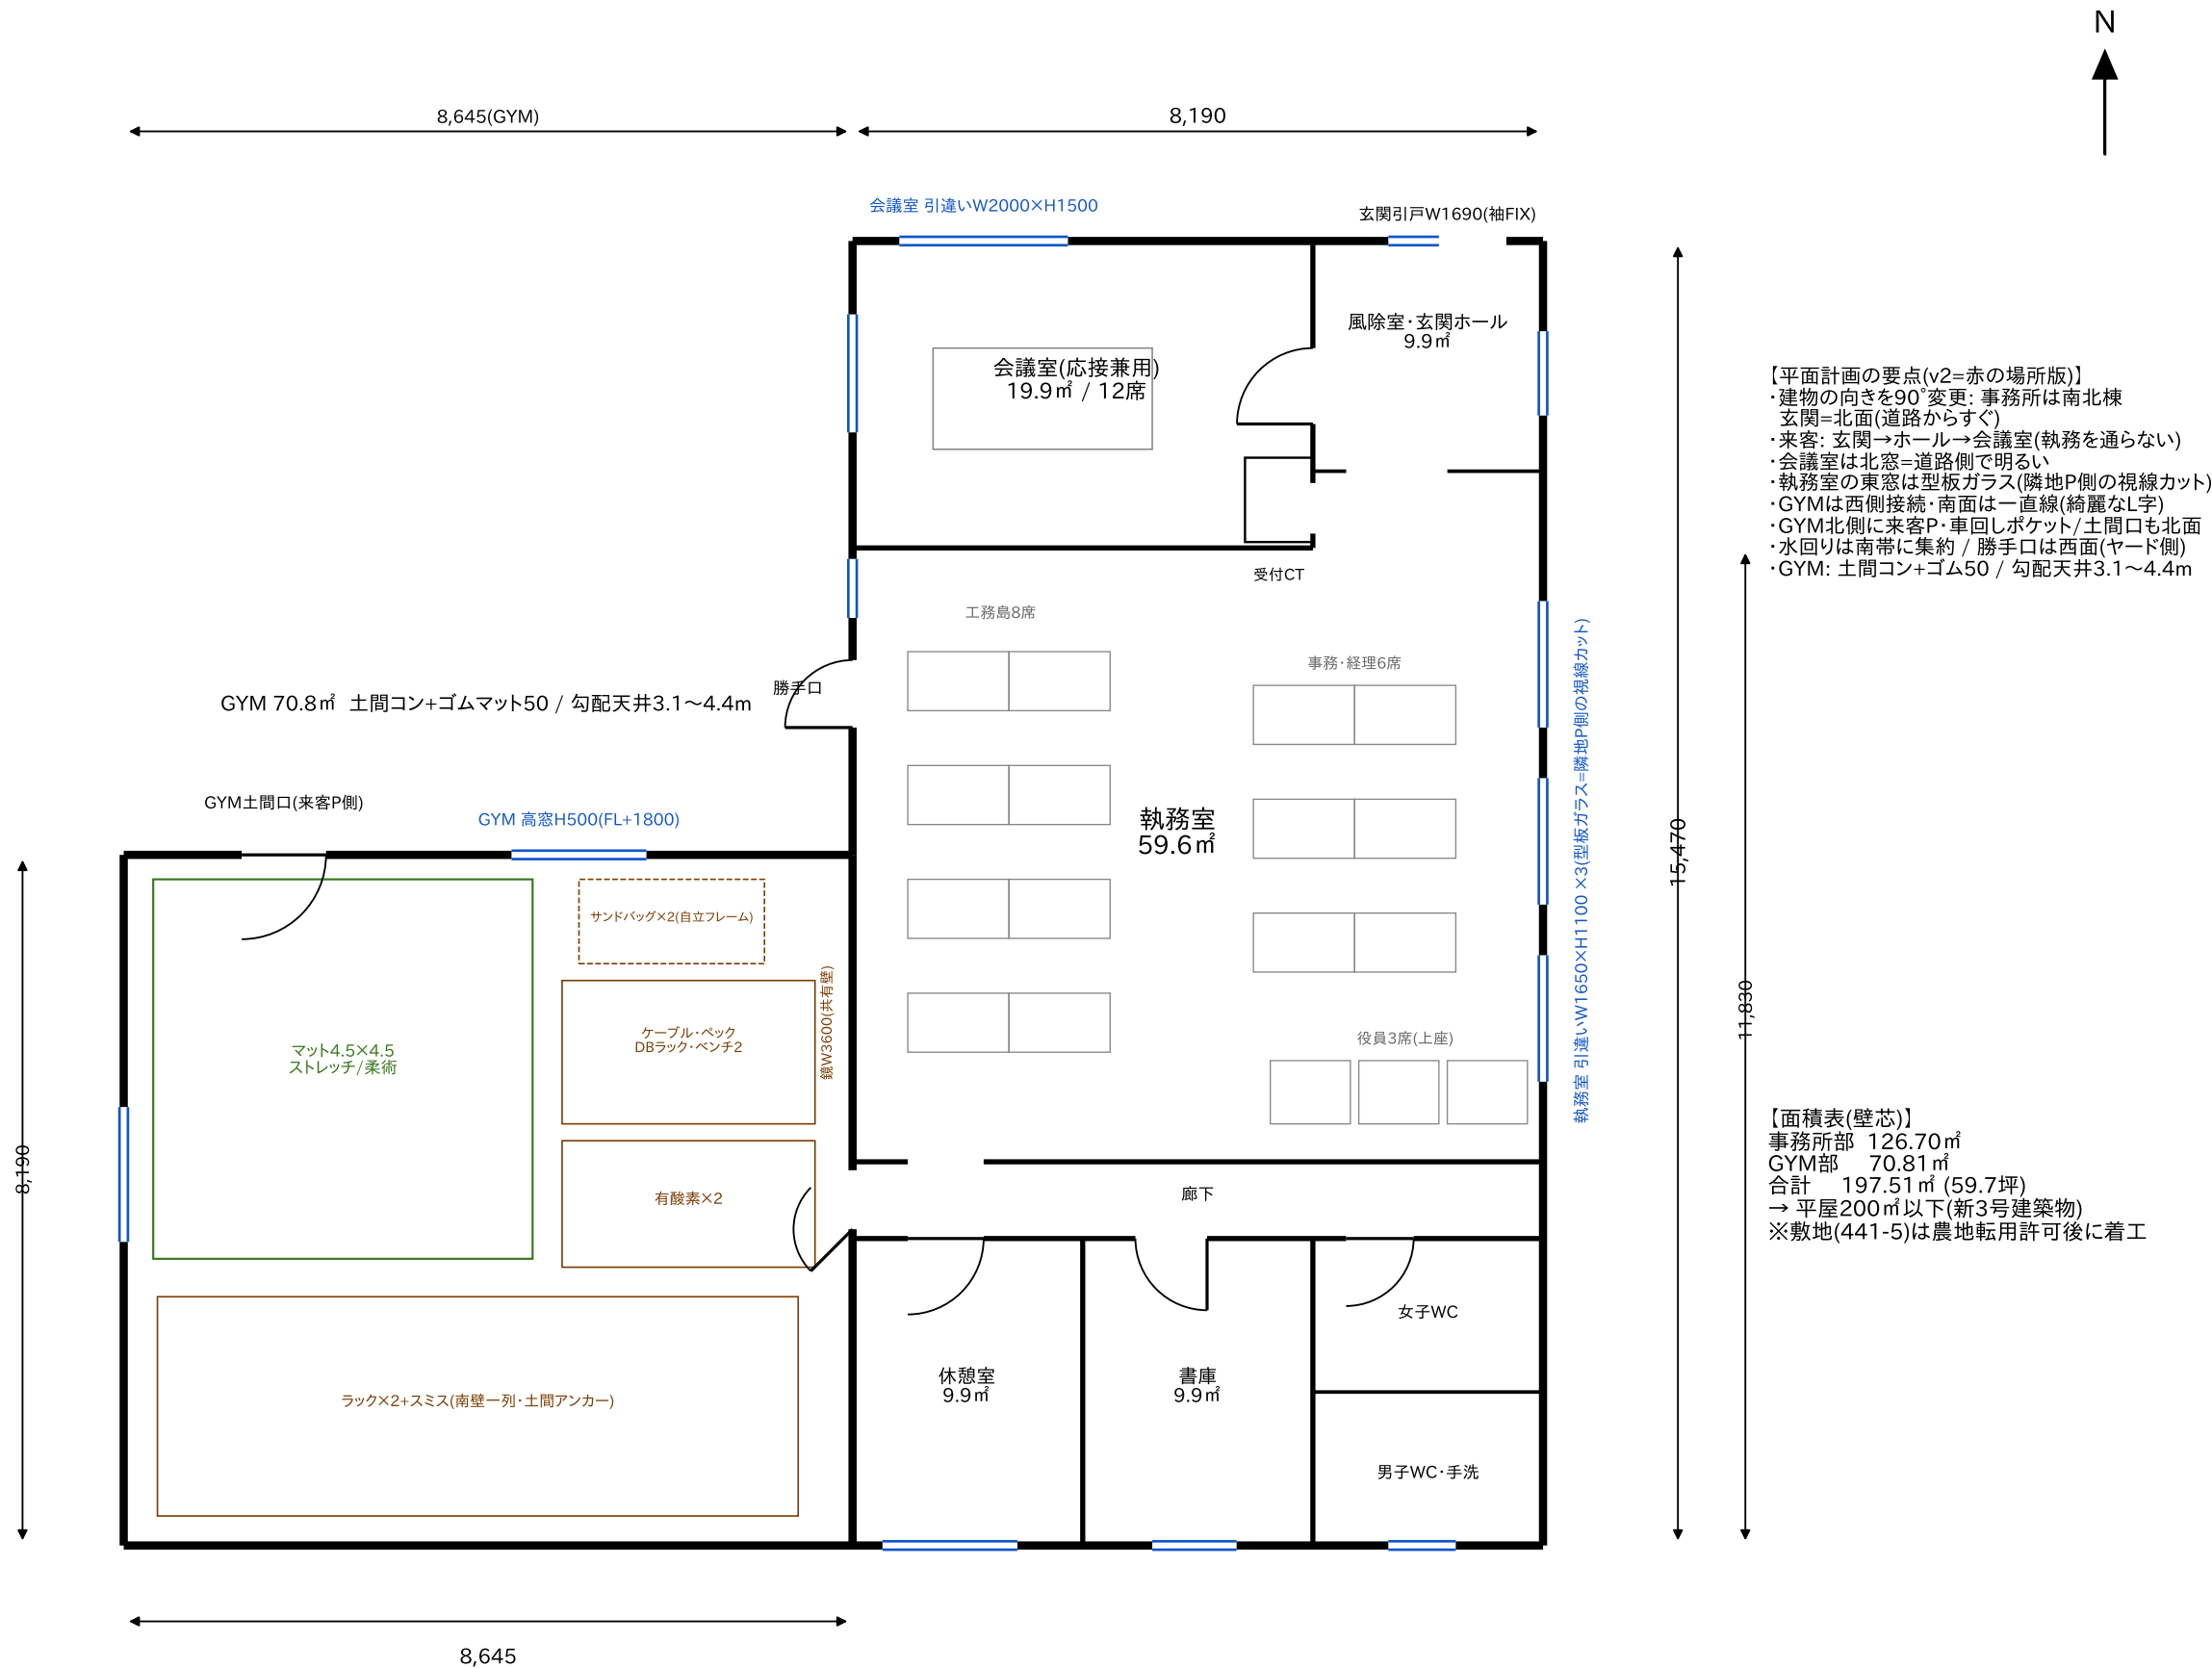


樋口工業有限会社 新社屋(事務所・GYM棟)新築工事	
図面名: 平面図	A-02
縮尺 1/100・2026-08-19・計画案v3(たたき台)	

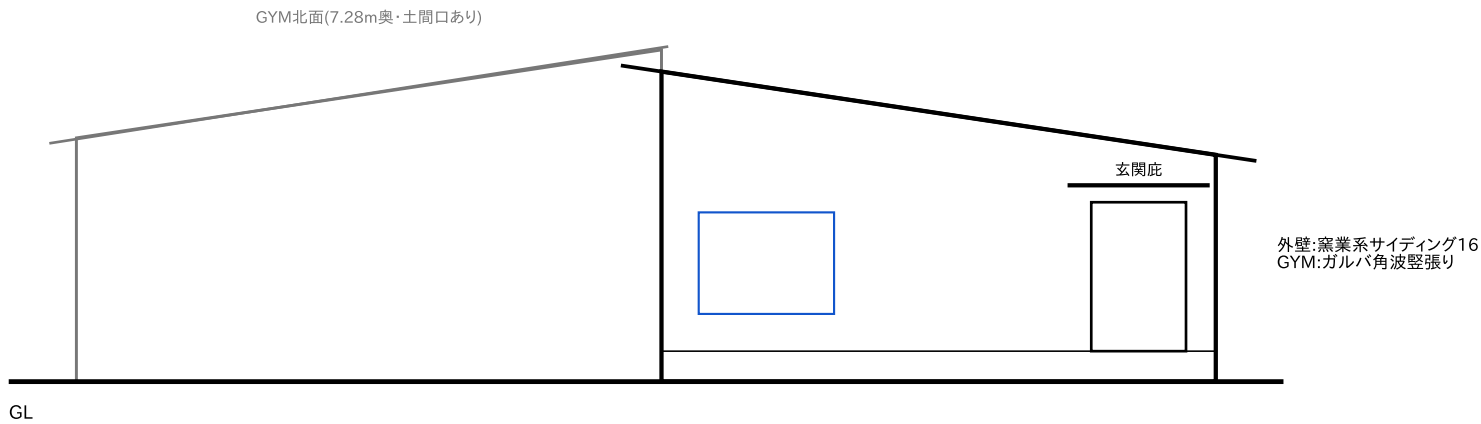


北立面図(道路側) 1/150

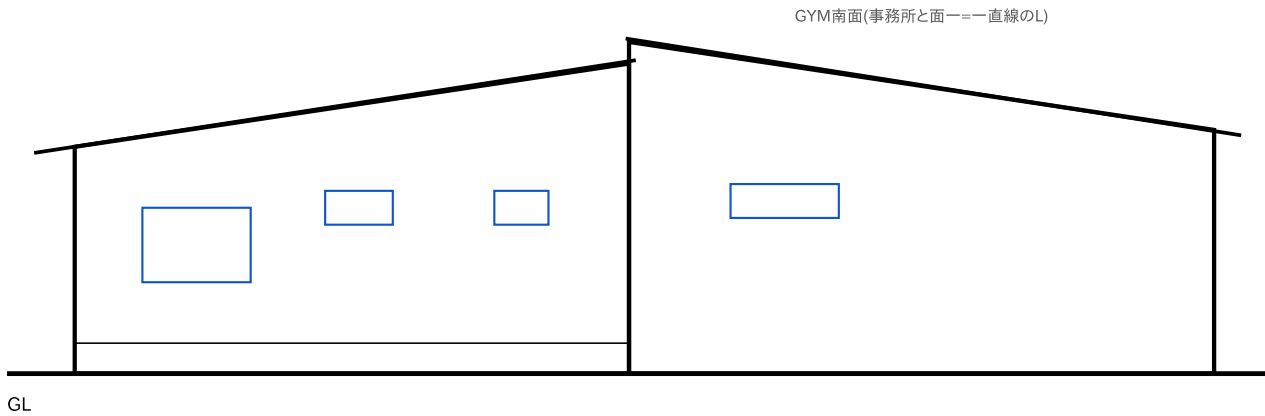

南立面図 1/150

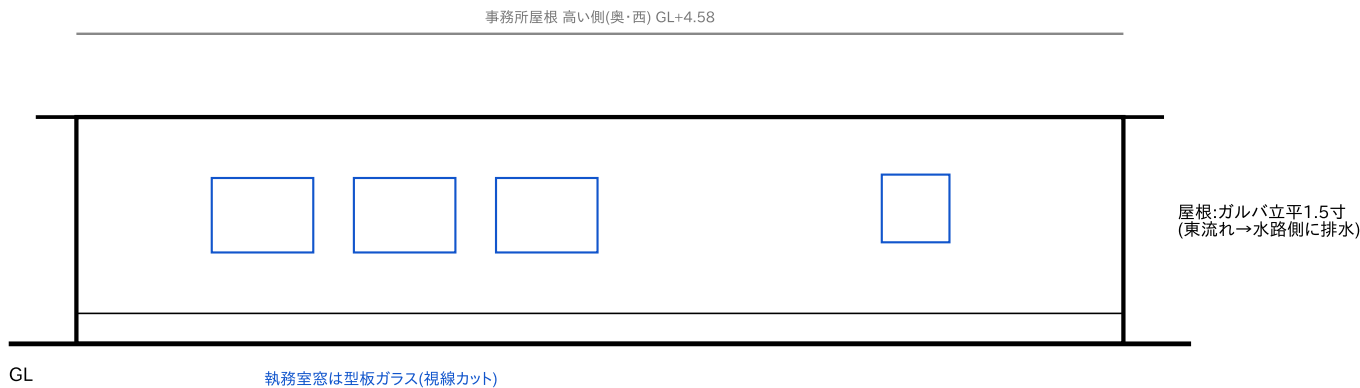


東立面図(隣地駐車場側) 1/150

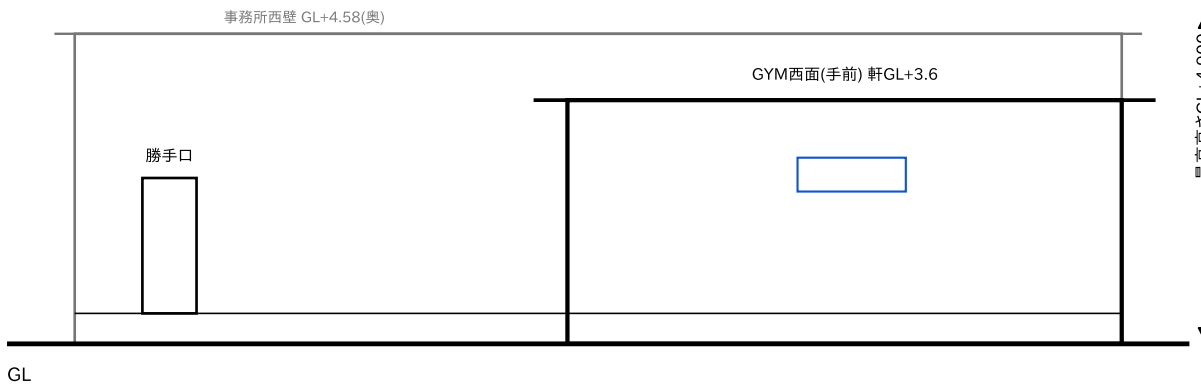

西立面図(ヤード側) 1/150

樋口工業有限会社 新社屋(事務所・GYM棟)新築工事	
図面名: 立面図(4面)	A-03
縮尺 1/150・2026-08-19・計画案v3(たたき台)	

樋口工業有限会社 新社屋(事務所・GYM棟)新築工事	
図面名: 断面図・仕様概要	A-04
縮尺 1/60・2026-08-19・計画案v3(たたき台)	

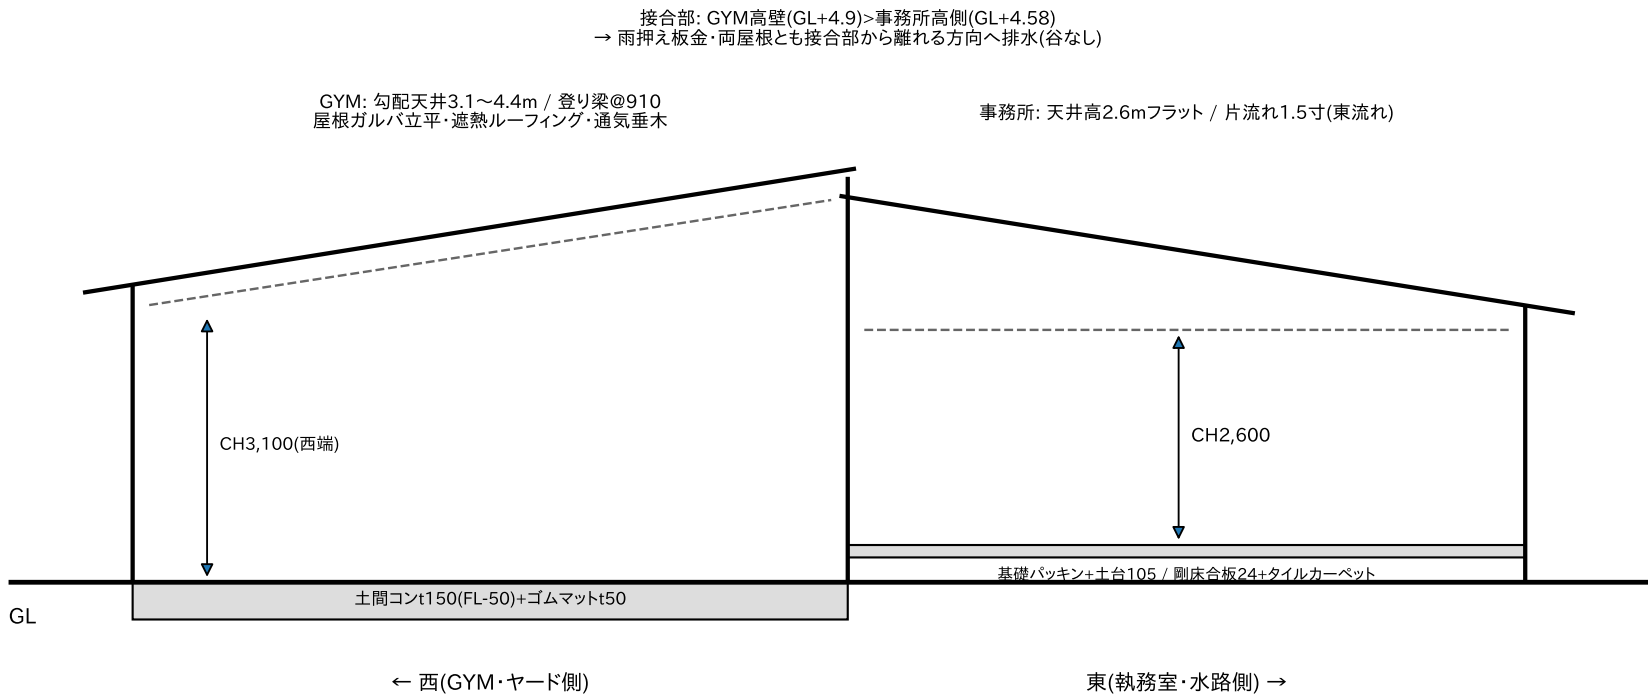

A-A断面図(東西) 1/60

【構造・仕上概要(たたき台)】

構造: 木造在来軸組・平屋 / 基礎: ベタ基礎(GYM部は土間一体・機材アンカー対応配筋)
壁量: 2025年改正基準による壁量計算(構造用合板9mm N50@150 外周耐力壁)
屋根: ガルバリウム鋼板立平葺き1.5寸 / 軒の出600 / 事務所=東流れ・GYM=西流れ
外壁: 窯業系サイディング16(事務所)+ガルバ角波縦張り(GYM)・通気工法
断熱: 屋根HGW16K155×2層 / 壁HGW16K105 / 基礎・土間XPS50 / サッシ アルミ樹脂複合Low-E
内装: 事務所 PB12.5+塗装(AEP)・タイルカーペット / GYM 腰壁合板12現し+PB・ゴムマット50
設備: 24h換気(3種)+GYM換気強化 / エアコン執務2・会議1・GYM1 / LAN Cat6A / 照明LED
※建設地(441-5)は農地転用許可が着工の前提。※本図は実施設計前の計画案。最終確認は設計者(建築士)による。