


町道(道路敷=広川町名義) ※42条認定確認中 ― 北面は道路際・出入口なし(窓+サイン帯)

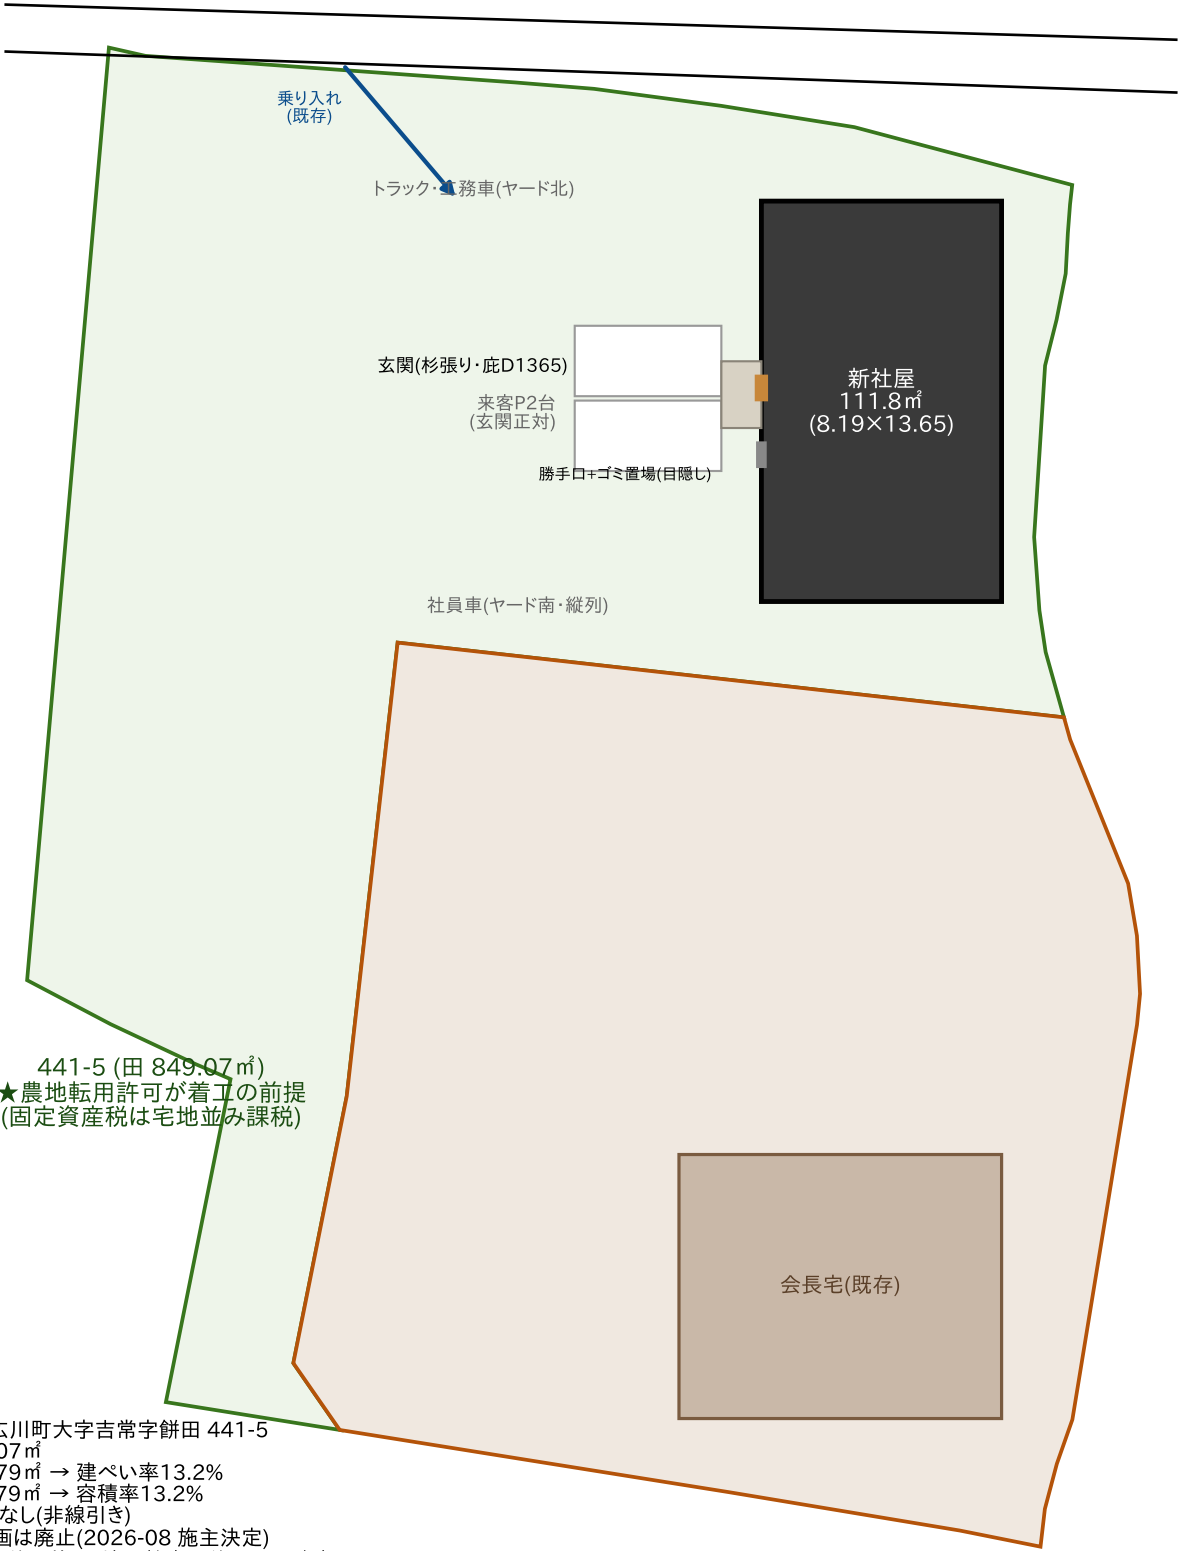

生垣・水路 → 隣地(友野氏・駐車場)


441-5 (田 849.07㎡)
★農地転用許可が着工の前提
(固定資産税は宅地並み課税)

【敷地】八女郡広川町大字吉常字餅田 441-5
敷地面積 849.07㎡
建築面積 111.79㎡ → 建ぺい率13.2%
延べ面積 111.79㎡ → 容積率13.2%
用途地域: 指定なし(非線引き)
※GYM増築計画は廃止(2026-08 施主決定)
※農地転用許可後に着工/境界杭実測後に配置確定

10m

樋口工業有限会社 新社屋新築工事(木造平屋・事務所 111.8㎡)	
図面名: 配置図	A-01
縮尺 1/250・2026-08-20・計画案v12(動線是正・プレゼン版)	

【v12 動線是正(プレゼン版)】
・ホールから南へ共用廊下W910を新設し、WC・SKを「中立ゾーン」に
ー 来客も工務も事務も、他部門の部屋を通らずにトイレへ行ける
(旧案はWCが事務室内からのみ=部門分室と矛盾 → 解消)
・事務室⇄廊下にも引戸：経理・役員WC動線は最短5m
・工務倉庫をL字7.7㎡に拡大(工務室から直接出入り・現場ボックス対応)
・男WC=大1小1+手洗/女WC=1+手洗/SK・掃除・設備室を明記
・勝手口は引戸に変更(机との干渉解消)。機器は全て扉の軌跡外に配置
・部屋割り：会議室19.9/工務室24.8/事務室28.2(7席+予備・1人4.0㎡)
・席名：会長・社長・常務(南窓)/彩加・恵理子(金庫2m)/丸山+予備(受付)/
江刈+予備・隈部・古賀・末永+予備(工務室・将来8席化可)
・複合機は工務室①・事務室②の2台(工務室はプロッタも)

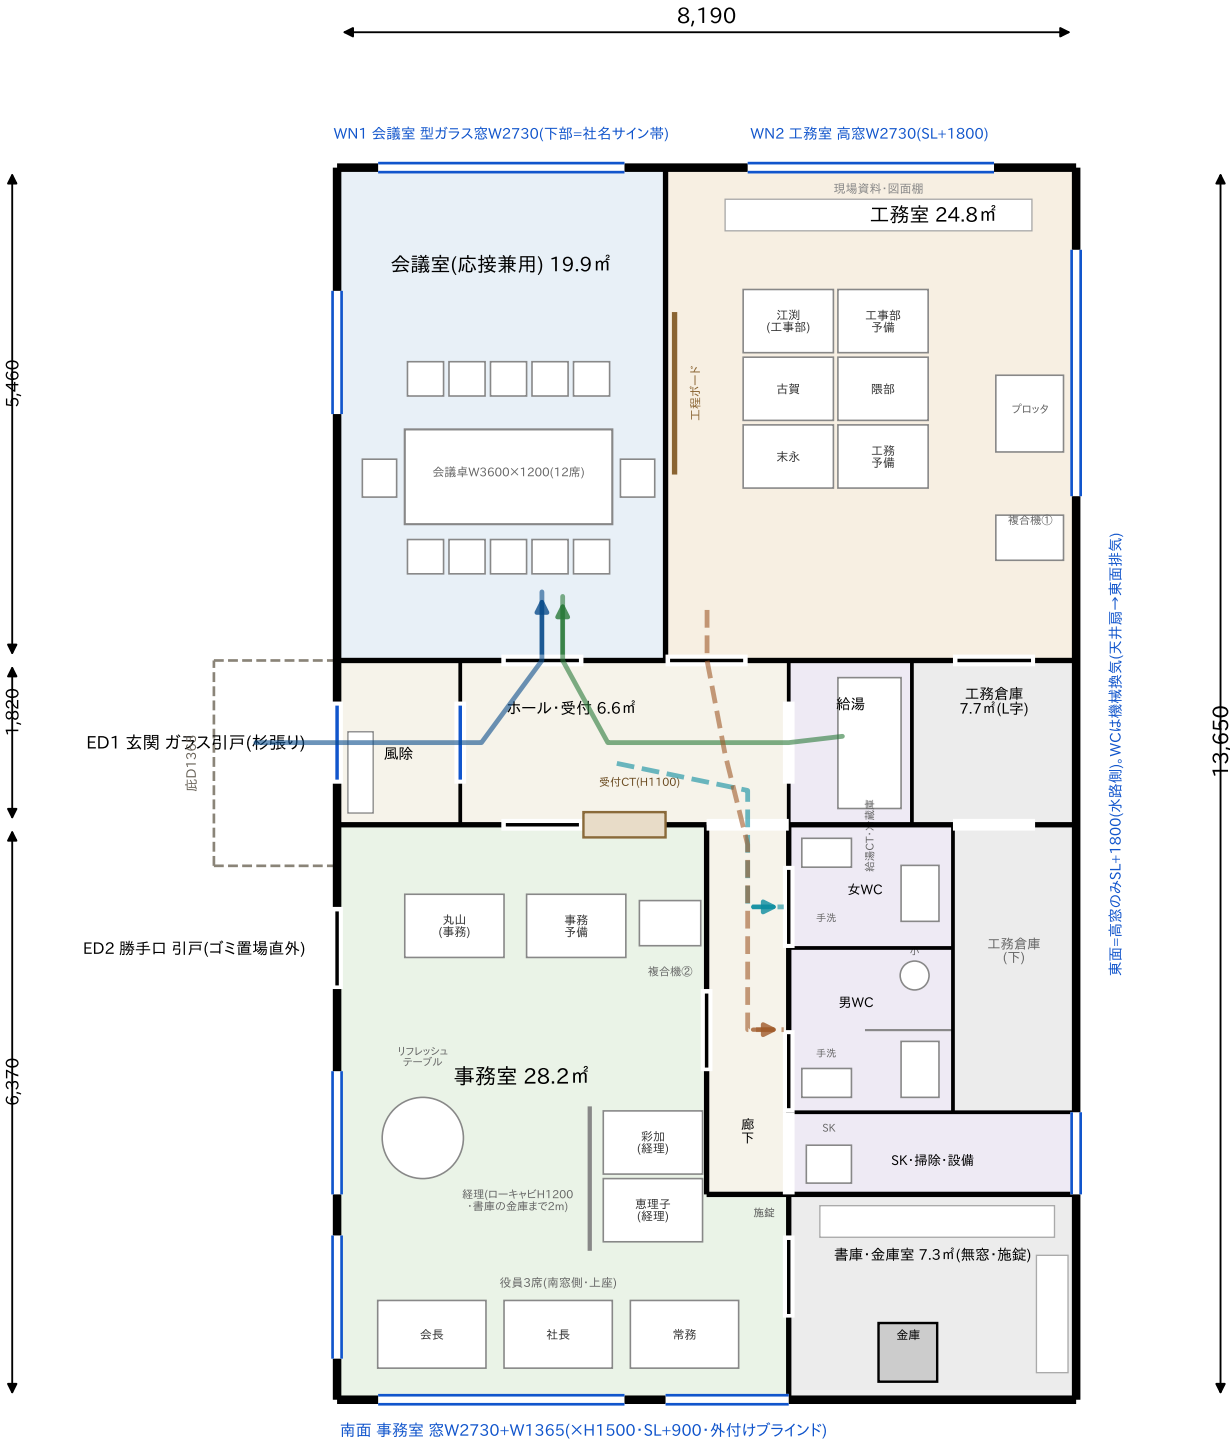

- 来客: 玄関→ホール→会議室(扉2枚・執務エリアに入らない)
- 来客WC: ホール→共用廊下→女WC(=どの部屋も通らない)
- お茶出し: 給湯→ホール→会議室(扉1枚・約5m)
- 工務のWC: 工務室→ホール→共用廊下(事務室を通らない)


- | | | |
|-----------------|-----------------|----------------|
| ■ 接遇(会議・応接) | ■ 工務(執務・倉庫) | ■ 事務(役員・経理・事務) |
| ■ 共用(風除・ホール・廊下) | ■ 水回り(給湯・WC・SK) | ■ 保管(書庫・金庫) |

【面積表(壁芯)111.79㎡=33.8坪】
会議室19.87/工務室24.84/風除2.48/ホール・受付6.63/給湯2.48
工務倉庫7.66(上3.31+下4.35)/廊下3.73/女WC2.48/男WC3.31
SK・設備2.90/書庫・金庫室7.25/事務室28.16
※FL=GL+450(風除のみ土間)/WCは機械換気(天井扇→東面排気)
※席：現12名+予備3(計15席)/敷地(441-5)は農地転用許可後に着工

樋口工業有限会社 新社屋新築工事(木造平屋・事務所 111.8㎡)

図面名: 平面図 A-02


縮尺 1/100・2026-08-20・計画案v12(動線是正・プレゼン版)

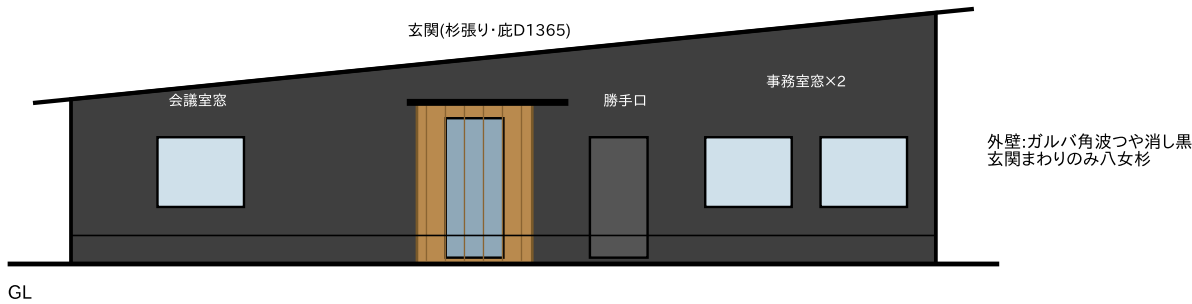


西立面図(ヤード・駐車場側=入口の顔) 1/150



北立面図(道路の顔・出入口なし) 1/150

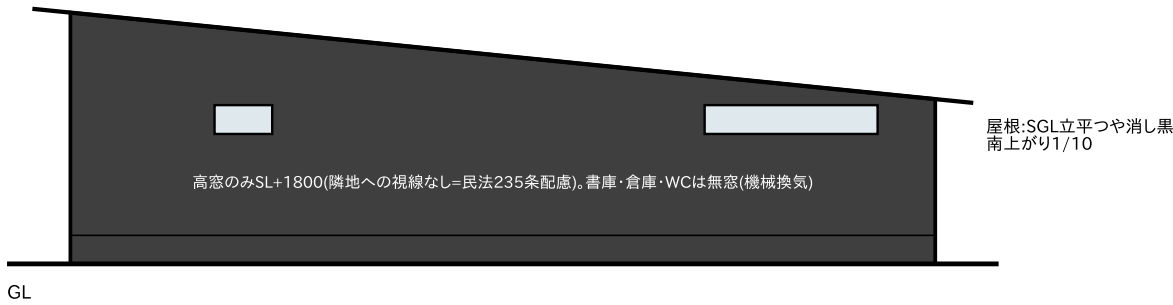

東立面図(生垣・水路側) 1/150

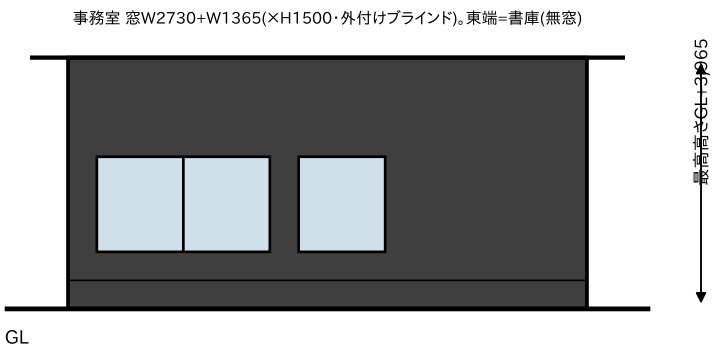


南立面図(採光面) 1/150

樋口工業有限会社 新社屋新築工事(木造平屋・事務所 111.8㎡)

図面名: 断面図・仕様概要A-04

縮尺 1/60・2026-08-20・計画案v12(動線是正・プレゼン版)

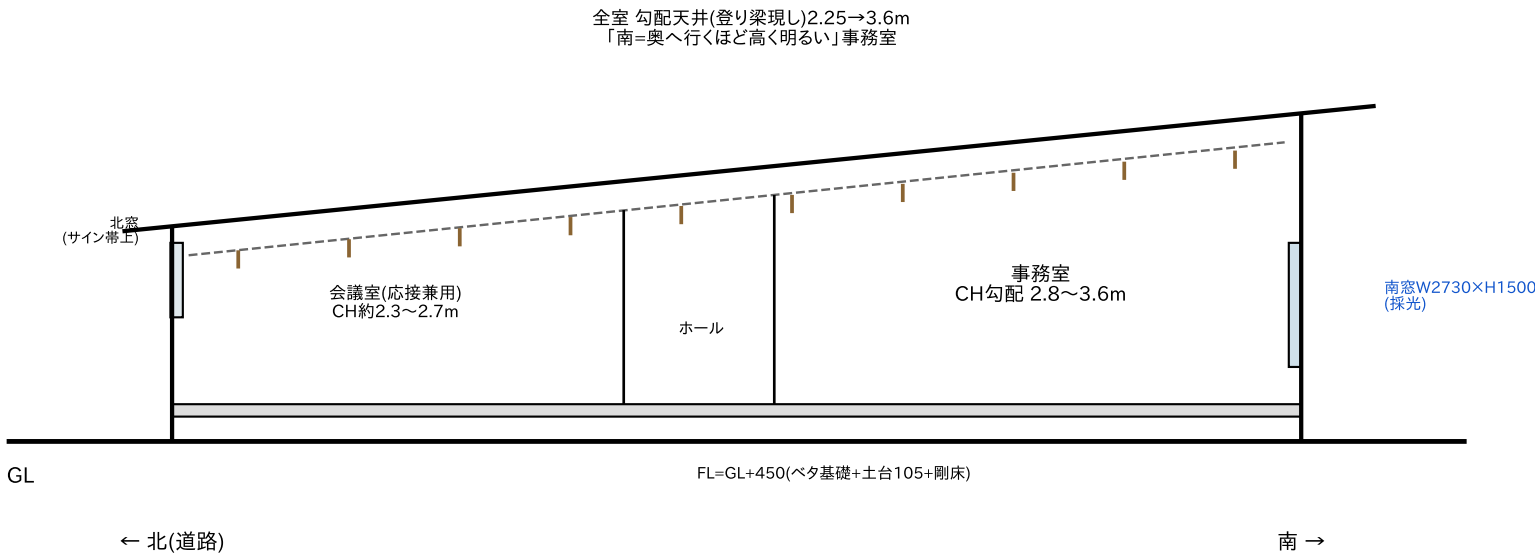

A-A断面図(南北・x=2.3 会議室～ホール～事務室) 1/60


【構造・仕上概要(v12)】

構造: 木造在来・平屋(8.19×13.65m) / 基礎: ベタ基礎 / 壁量: 2025年改正基準(要壁量計算。部門間の間仕切壁・廊下壁を耐力壁に活用)
屋根: SGLガルバ立平つや消し黒・南上がり1/10(北軒GL+2.6→南壁GL+3.97) / 外壁: ガルバ角波つや消し黒+玄関まわりのみ八女杉
サッシ: アルミ樹脂複合 黒 / 断熱: 屋根HGW16K155×2・壁HGW16K105・基礎XPS50 / 天窓なし
内装: 事務・工務=登り梁現し+タイルカーペット / 会議室=杉板1面壁 / ホール・廊下=モルタル金鏝+受付CT / 書庫=可動棚・無窓・施錠
換気: 24h換気3種。WC・SKは天井扇→東面ダクト排気(内部化のため機械換気) / エアコン: 事務1・工務1・会議1 / LAN Cat6A
水回り集約: WC・SK・給湯を廊下まわりの1系統に=配管最短 / 南・西窓は外付けブラインド / 外構(自社施工): 舗装+白線・来客P2台・社名サイン
※GYM増築計画は廃止 ※屋根北流れ=太陽光不向き ※建設地(441-5)は農地転用許可が前提 ※最終確認は設計者(建築士)による

外観イメージ(北西=道路・ヤード側から)

「黒い箱に、八女杉の玄関」

- ・つや消し黒のガルバの箱。玄関まわりだけ八女杉=樋口工業の顔
- ・玄関に庇D1365: 来客Pから2〜3歩、雨に濡れずに入れる
- ・道路側(左)は会議室の型ガラス窓+工務室の高窓+社名サイン帯
- ・屋根は南へ登る片流れ: 事務室の奥ほど天井が高く明るい
- ・白線の駐車場・舗装は自社施工=施工品質がそのまま名刺になる
- ・夜は電球色2700Kでポーチとサインだけ照らす

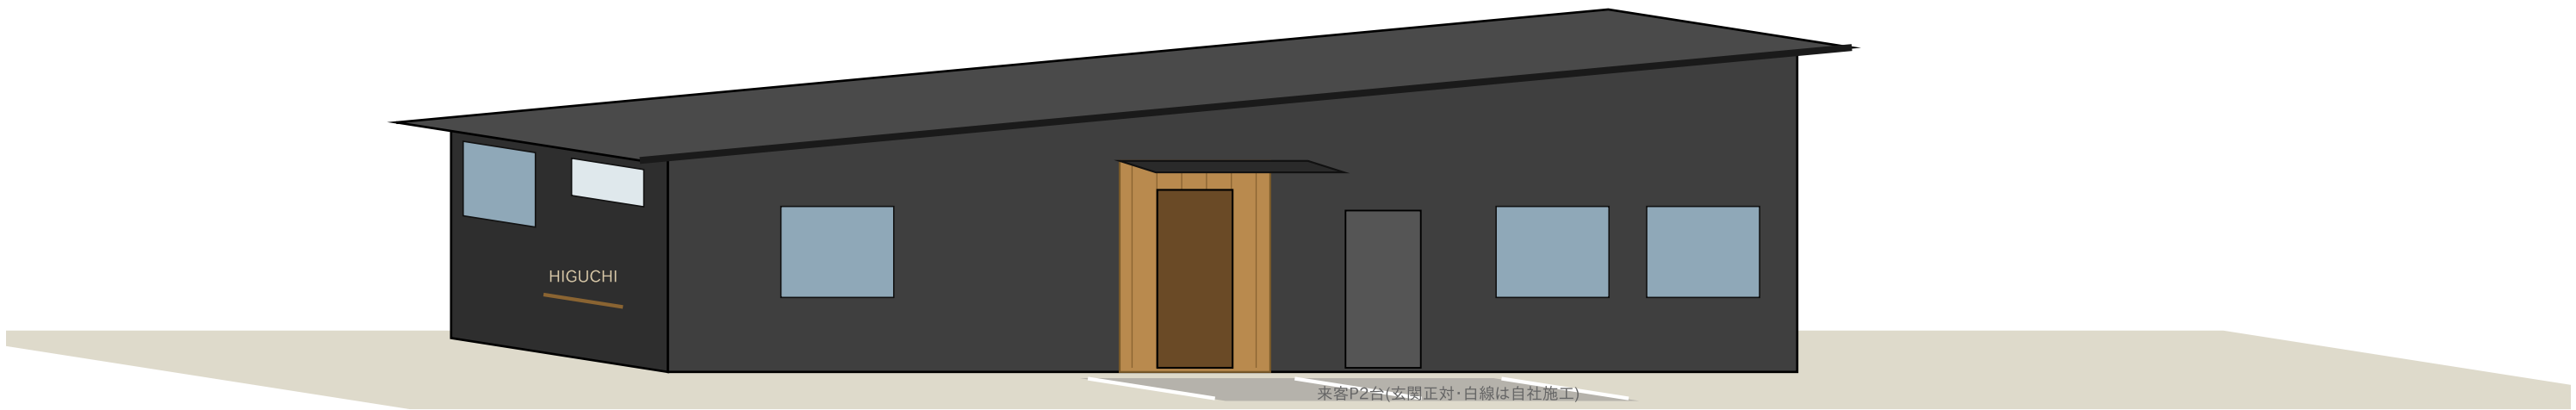

樋口工業有限会社 新社屋新築工事(木造平屋・事務所 111.8㎡)

図面名: 外観イメージ A-05

縮尺 NTS・2026-08-20・計画案v12(動線是正・プレゼン版)