

新社屋新築計画

樋口工業有限会社

福岡県八女郡広川町大字吉常字餅田 441-5

「黒い箱に、八女杉の玄関」

つや消し黒のガルバリウム製の箱に、
玄関まわりだけ八女杉。
舗装も白線も基礎も、自社の手で。
施工品質がそのまま名刺になる社屋。

計画案 v13(事務室拡大・会議室8席)

2026年8月20日

樋口工業有限会社(特定建設業 福岡県知事 許可(特-5)第91945号)

計画概要


用途	事務所(自社社屋)
構造・階数	木造在来軸組・平屋
延べ面積	111.79㎡(33.8坪) 8.19m×13.65m
主要室	会議室16.6㎡(8席・応接兼用)/工務室24.8㎡+倉庫7.7㎡/事務室31.5㎡
在籍	現12名+予備3席=15席(会長・社長・常務・経理2・事務・工事部・工務)
外装	屋根・外壁=ガルバリウムつや消し黒/玄関=八女杉・庇D1365
高さ	片流れ 南上がり1/10(北軒GL+2.6m→最高GL+3.97m)
敷地	441-5(849.07㎡)建ぺい率13.2%・容積率13.2%(指定なし・非線引き)
概算工事費	約1,050～1,550万円(自社施工原価・詳細はA-06)
完成目標	2027年 夏～秋(農地転用許可→確認申請→着工)

図面リスト


A-01	配置図 1/250
A-02	平面図 1/100(ゾーン・動線・席名入り)
A-03	立面図4面 1/150
A-04	断面図・仕様概要 1/60
A-05	外観イメージ
A-06	計画概要・概算工事費・スケジュール

※本図書は実施設計前の計画案。寸法・構造・法適合の最終確認と確認申請図書の作成は設計者(建築士)による。

※建設地(441-5)は農地転用許可が着工の前提。境界杭実測後に配置確定。

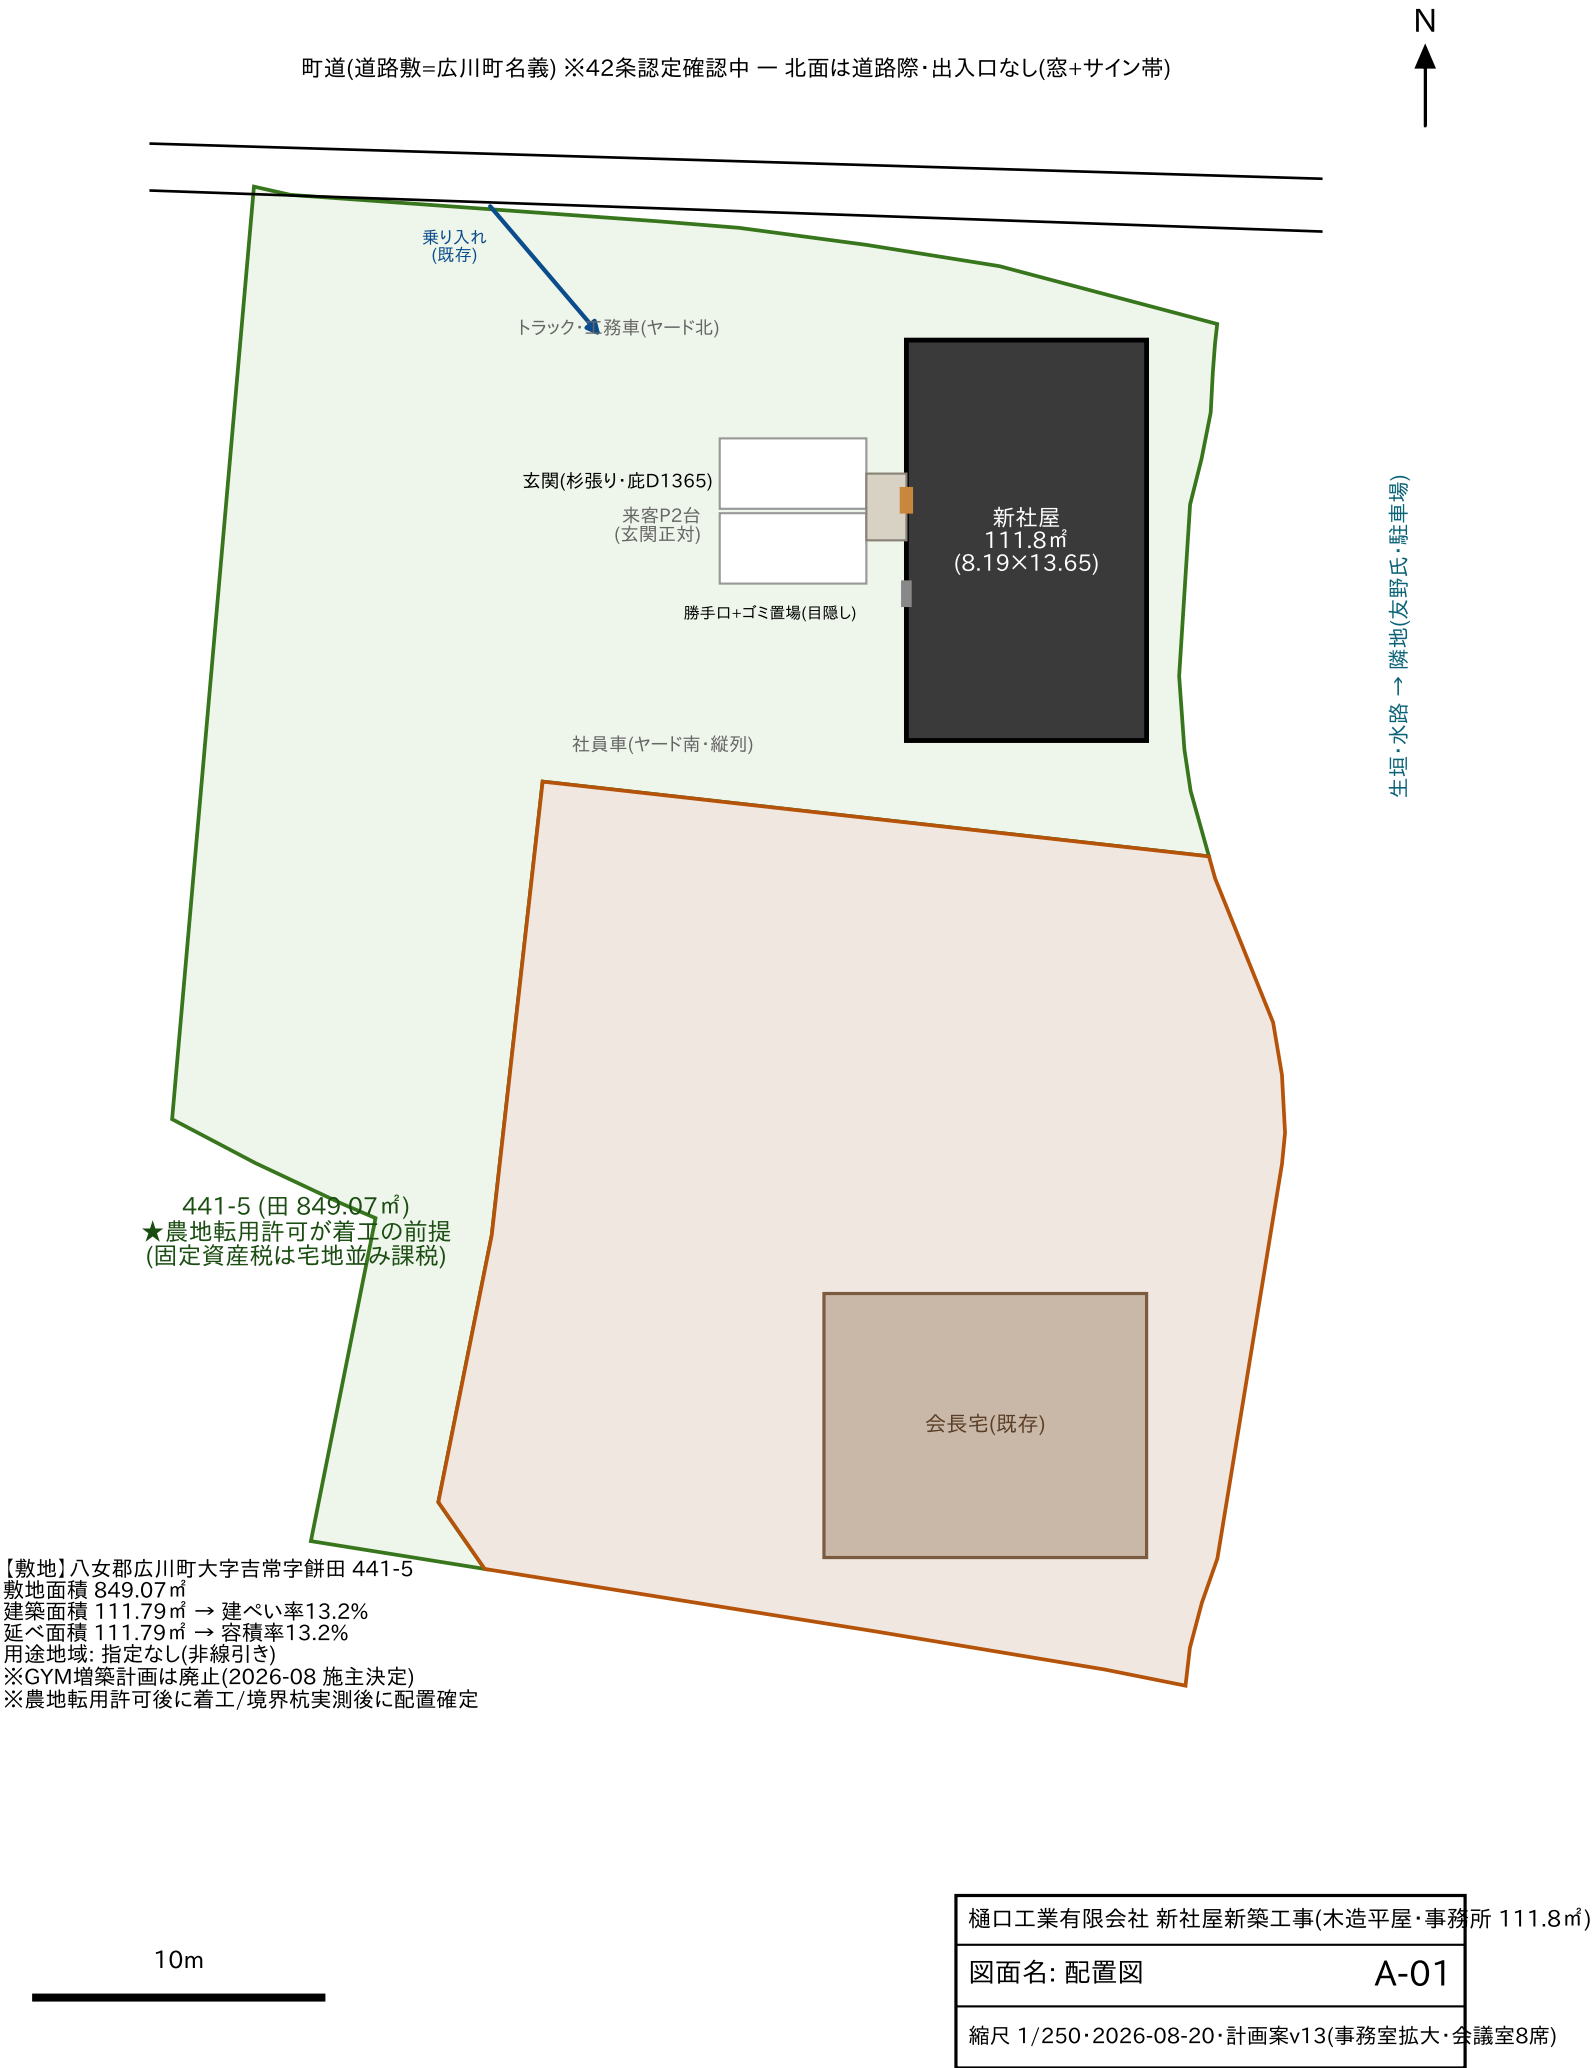

[v13 事務室拡大・会議室8席(施主指示)]
・会議室を8人サイズ(19.9→16.6㎡・卓W2400×1200)に。玄関・ホール帯を0.91m北へ寄せ、浮いた分を全て事務室へ: 28.2→31.5㎡(7席+予備で1人4.5㎡)
・工務室24.8㎡は不変(戸は西壁=ホール正面に。動線はむしろ短縮)
・玄関→会議室が最短に(風除→ホール→すぐ北の会議室戸)
・共用廊下によるWC中立化・書庫・給湯・倉庫L字はv12を継承
・席名: 会長・社長・常務(南窓)/彩加・恵理子(金庫2m)/丸山+予備(受付)/江洸+予備・隈部・古賀・末永+予備(工務室・将来8席化可)
・複合機は工務室①・事務室②の2台(工務室はプロッタも)
・事務室に西窓を1本追加(WW4=事務席の手元光)

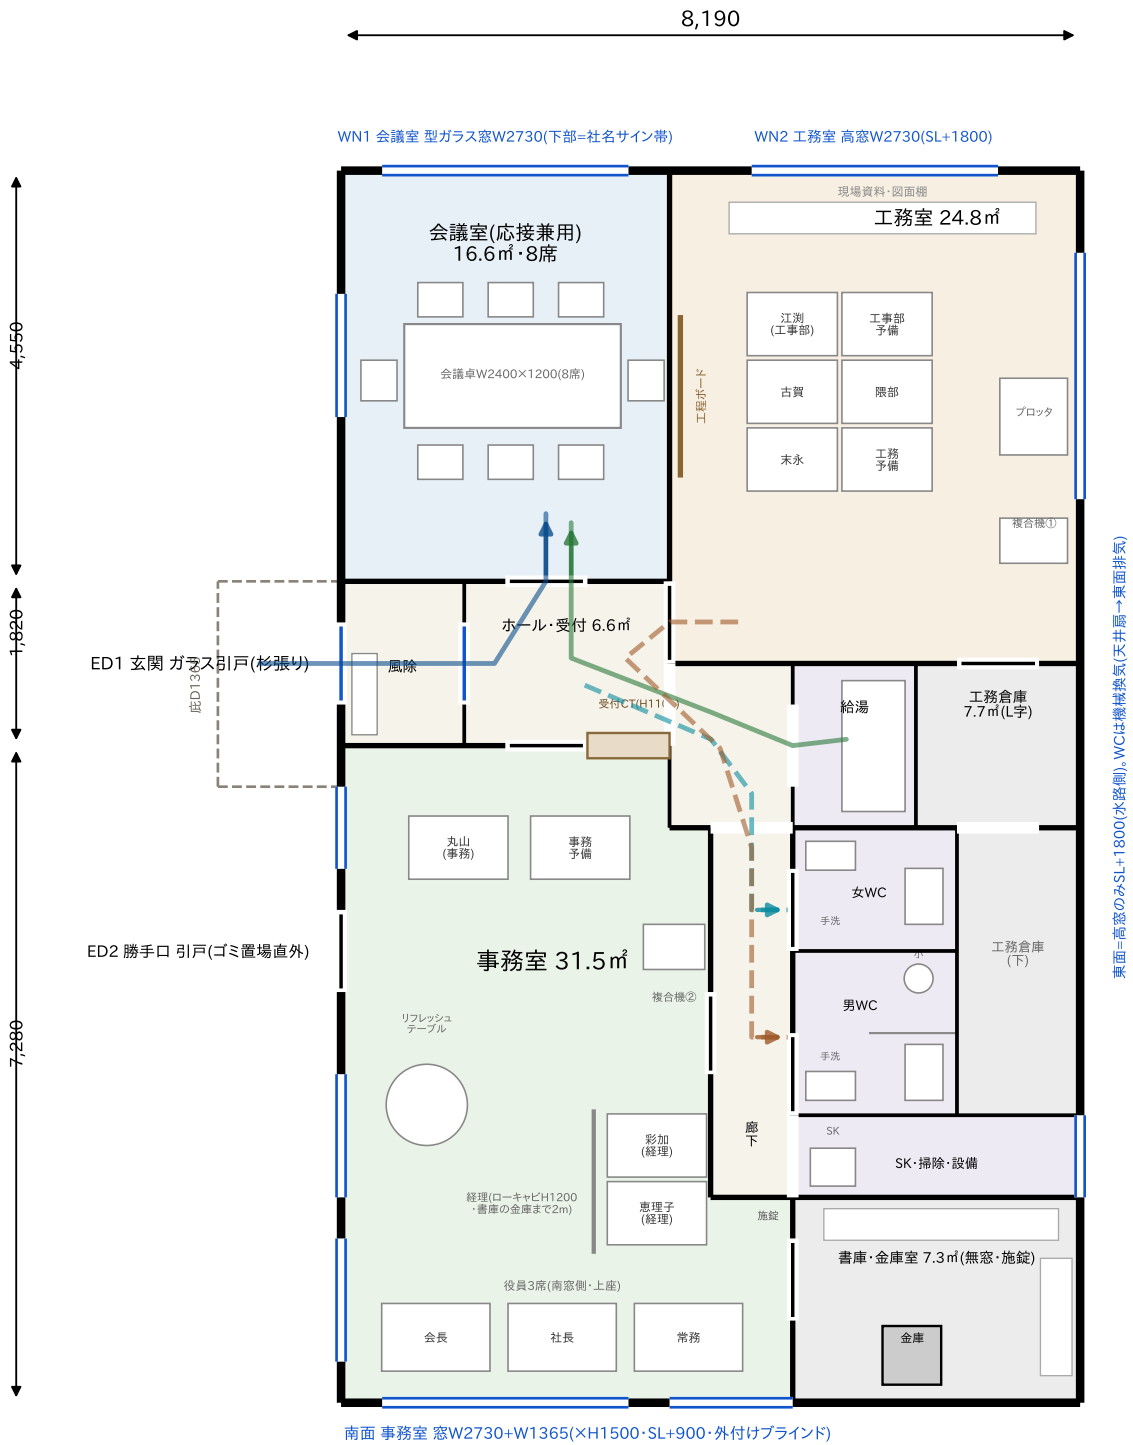

- 来客: 玄関→ホール→会議室(扉2枚・執務エリアに入らない)
- 来客WC: ホール→共用廊下→女WC(=どの部屋も通らない)
- お茶出し: 給湯→ホール→会議室(扉1枚・約5m)
- 工務のWC: 工務室→ホール→共用廊下(事務室を通らない)


- | | | |
|-----------------|-----------------|----------------|
| ■ 接遇(会議・応接) | ■ 工務(執務・倉庫) | ■ 事務(役員・経理・事務) |
| ■ 共用(風除・ホール・廊下) | ■ 水回り(給湯・WC・SK) | ■ 保管(書庫・金庫) |

【面積表(壁芯)111.79㎡=33.8坪】
会議室16.56/工務室24.84/風除2.48/ホール・受付6.62/給湯2.48
工務倉庫7.66(上3.31+下4.35)/廊下3.73/女WC2.48/男WC3.31
SK・設備2.90/書庫・金庫室7.25/事務室31.47
※FL=GL+450(風除のみ土間)/WCは機械換気(天井扇→東面排気)
※席: 現12名+予備3(計15席)/敷地(441-5)は農地転用許可後に着工

樋口工業有限会社 新社屋新築工事(木造平屋・事務所 111.8㎡)

図面名: 平面図 A-02

縮尺 1/100・2026-08-20・計画案v13(事務室拡大・会議室8席)

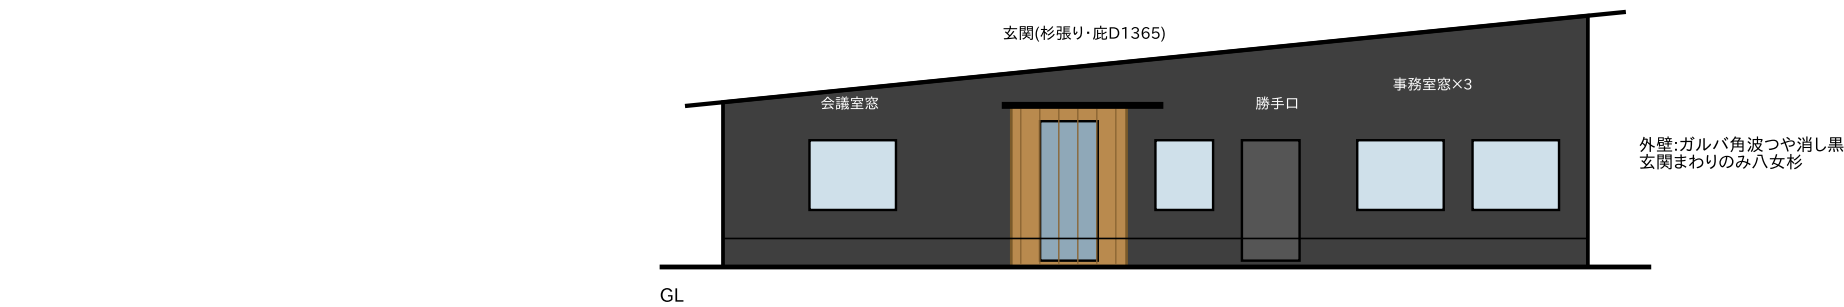


西立面図(ヤード・駐車場側=入口の顔) 1/150



北立面図(道路の顔・出入口なし) 1/150



東立面図(生垣・水路側) 1/150

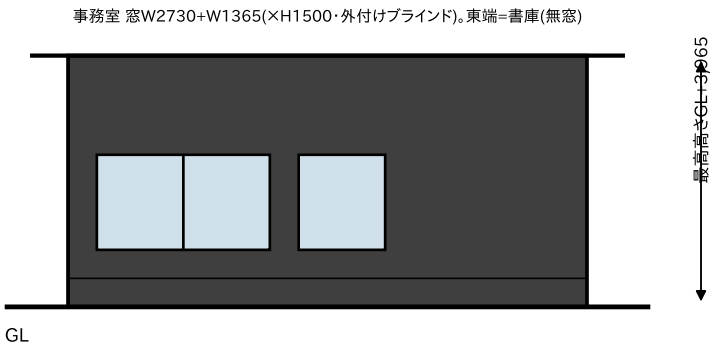


南立面図(採光面) 1/150

樋口工業有限公司 新社屋新築工事(木造平屋・事務所 11)	
図面名: 立面図(4面)	A-03
縮尺 1/150・2026-08-20・計画案v13(事務室拡大・会議室8)	

樋口工業有限会社 新社屋新築工事(木造平屋・事務所 111.8㎡)

図面名: 断面図・仕様概要A-04

縮尺 1/60・2026-08-20・計画案v13(事務室拡大・会議室8席)

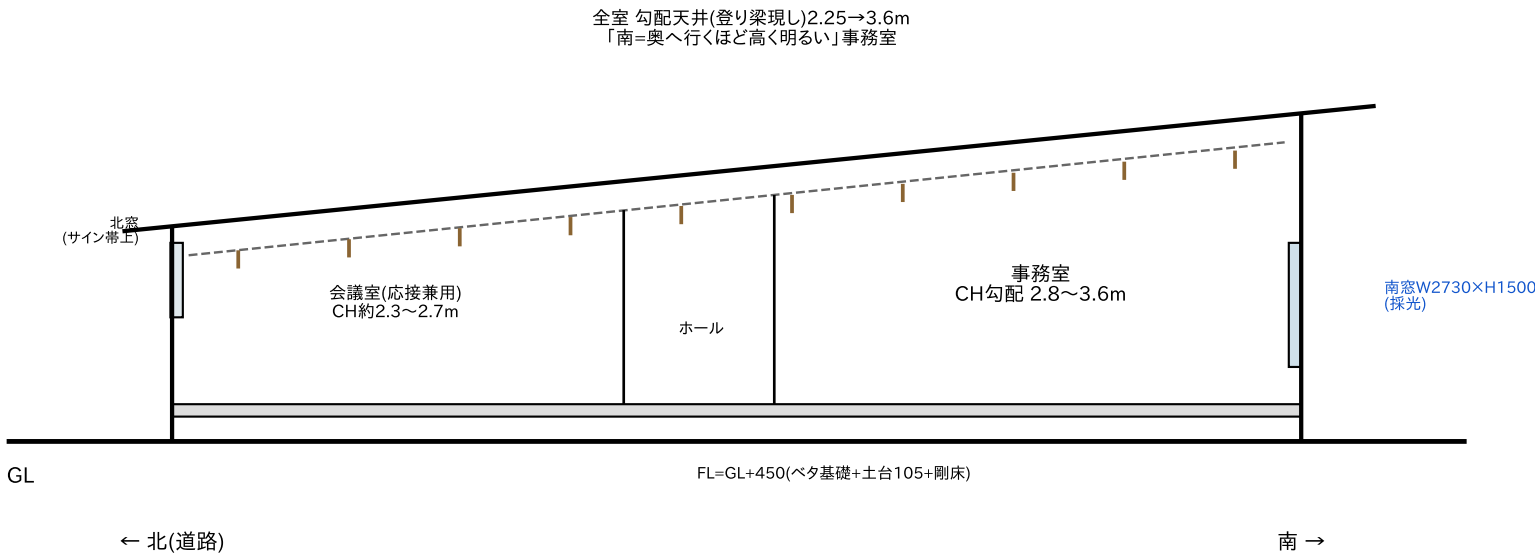

A-A断面図(南北・x=2.3 会議室～ホール～事務室) 1/60


【構造・仕上概要(v12)】

構造: 木造在来・平屋(8.19×13.65m) / 基礎: ベタ基礎 / 壁量: 2025年改正基準(要壁量計算。部門間の間仕切壁・廊下壁を耐力壁に活用)
屋根: SGLガルバ立平つや消し黒・南上がり1/10(北軒GL+2.6→南壁GL+3.97) / 外壁: ガルバ角波つや消し黒+玄関まわりのみ八女杉
サッシ: アルミ樹脂複合 黒 / 断熱: 屋根HGW16K155×2・壁HGW16K105・基礎XPS50 / 天窓なし
内装: 事務・工務=登り梁現し+タイルカーペット / 会議室=杉板1面壁 / ホール・廊下=モルタル金鍍+受付CT / 書庫=可動棚・無窓・施錠
換気: 24h換気3種。WC・SKは天井扇→東面ダクト排気(内部化のため機械換気) / エアコン: 事務1・工務1・会議1 / LAN Cat6A
水回り集約: WC・SK・給湯を廊下まわりの1系統に=配管最短 / 南・西窓は外付けブラインド / 外構(自社施工): 舗装+白線・来客P2台・社名サイン
※GYM増築計画は廃止 ※屋根北流れ=太陽光不向き ※建設地(441-5)は農地転用許可が前提 ※最終確認は設計者(建築士)による

外観イメージ(北西=道路・ヤード側から)

「黒い箱に、八女杉の玄関」

- ・つや消し黒のガルバの箱。玄関まわりだけ八女杉=樋口工業の顔
- ・玄関に庇D1365: 来客Pから2〜3歩、雨に濡れずに入れる
- ・道路側(左)は会議室の型ガラス窓+工務室の高窓+社名サイン帯
- ・屋根は南へ登る片流れ: 事務室の奥ほど天井が高く明るい
- ・白線の駐車場・舗装は自社施工=施工品質がそのまま名刺になる
- ・夜は電球色2700Kでポーチとサインだけ照らす

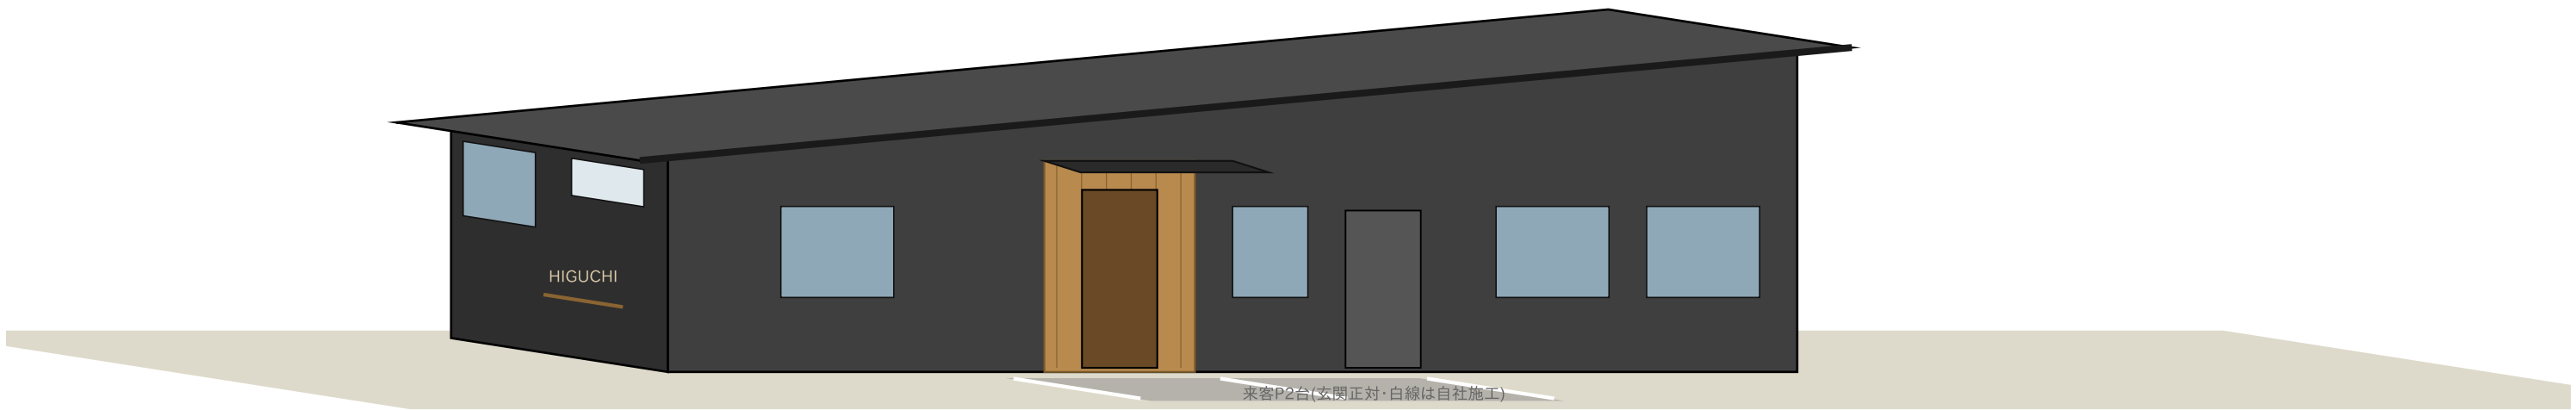

樋口工業有限会社 新社屋新築工事(木造平屋・事務所 111.8㎡)

図面名: 外観イメージ A-05

縮尺 NTS・2026-08-20・計画案v13(事務室拡大・会議室8席)

計画概要・概算工事費・スケジュール

概算工事費内訳(自社施工原価ベース)

仮設工事(足場・養生・仮設電気)	20 ～ 40
基礎工事(ベタ基礎・自社施工=材工原価)	80 ～ 120
木工事(構造材・プレカット・金物・造作)	260 ～ 350
屋根・板金(SGL立平・雨樋)	55 ～ 80
外壁(ガルバ角波・八女杉・防水)	75 ～ 110
サッシ・玄関建具(アルミ樹脂複合)	65 ～ 95
断熱(屋根155×2・壁105・基礎XPS50)	35 ～ 55
内装(PB・仕上・タイルカーペット)	80 ～ 115
内部建具・受付CT等造作	45 ～ 70
電気設備(外注・照明・LAN)	85 ～ 120
給排水衛生(外注・指定工事店・器具)	85 ～ 120
空調・換気(エアコン3台・24h換気)	55 ～ 80
外構(舗装・白線・サイン=自社原価)	35 ～ 70
設計・申請・地盤調査・登記(農転含む)	45 ～ 80
諸経費・予備費	30 ～ 55
合計(万円)	約 1,050 ～ 1,550

※自社施工(基礎・外構・多能工)と協力会社の原価協力を織り込んだ目安。
※実施設計後の相見積(木造 vs 軽量鉄骨 →「08」)とVEで確定する。
※机・椅子・複合機等の什器・備品、外部給排水引込の負担金は別途。

樋口工業有限会社 新社屋新築工事(木造平屋・事務所 111.8㎡)
図面名: 計画概要・概算 A-06
縮尺 ・・2026-08-20・計画案v13(事務室拡大・会議室8席)

部門と席(現12名+予備3=15席)

役員	会長・社長・常務	事務室(南窓側・上座)
経理	彩加・恵理子	事務室(書庫・金庫の正面2m)
事務	丸山(+予備1)	事務室(受付CTの内側)
工事部	江渕(+予備1)	工務室(島)
工務	隈部・古賀・末永(+予備1)	工務室(島・将来8席化可)

使い勝手の要点

- ・来客: 玄関→ホール→すぐ北の会議室(8席)で完結。執務エリアに入らない
- ・トイレは共用廊下から: 来客も工務も事務も、他部門の部屋を通らない
- ・お茶出し: 給湯→ホール→会議室=扉1枚・約5m
- ・受付: 事務席が玄関すぐ内側。カウンター開口越しに着席のまま応対
- ・経理: 施錠書庫内の金庫まで2m。手元はローキャビで遮蔽
- ・工務: 専用室+倉庫7.7㎡直結(現場ボックス・プロッタ・工程ボード)

スケジュール(目標: 2027年 夏～秋 竣工)

2026年 9月～	広川町農業委員会に相談・農地転用許可申請(課税明細持参)
並行	実施設計(社内建築士)・相見積(木造 vs 軽量鉄骨)・地盤調査
2027年 1～2月	建築確認申請 → 確認済証
2027年 3月	着工(基礎=自社)
2027年 4月	上棟 → 屋根・外装
2027年 5～7月	内装・設備・外構(自社)
2027年 8月～	完了検査・検査済証 → 引越し・使用開始

※農地転用許可が全体のクリティカルパス(詳細は「10_全体工程表」)。