


町道(道路敷=広川町名義) ※42条認定確認中 ― 北面は道路際・出入口なし(窓+サイン帯)

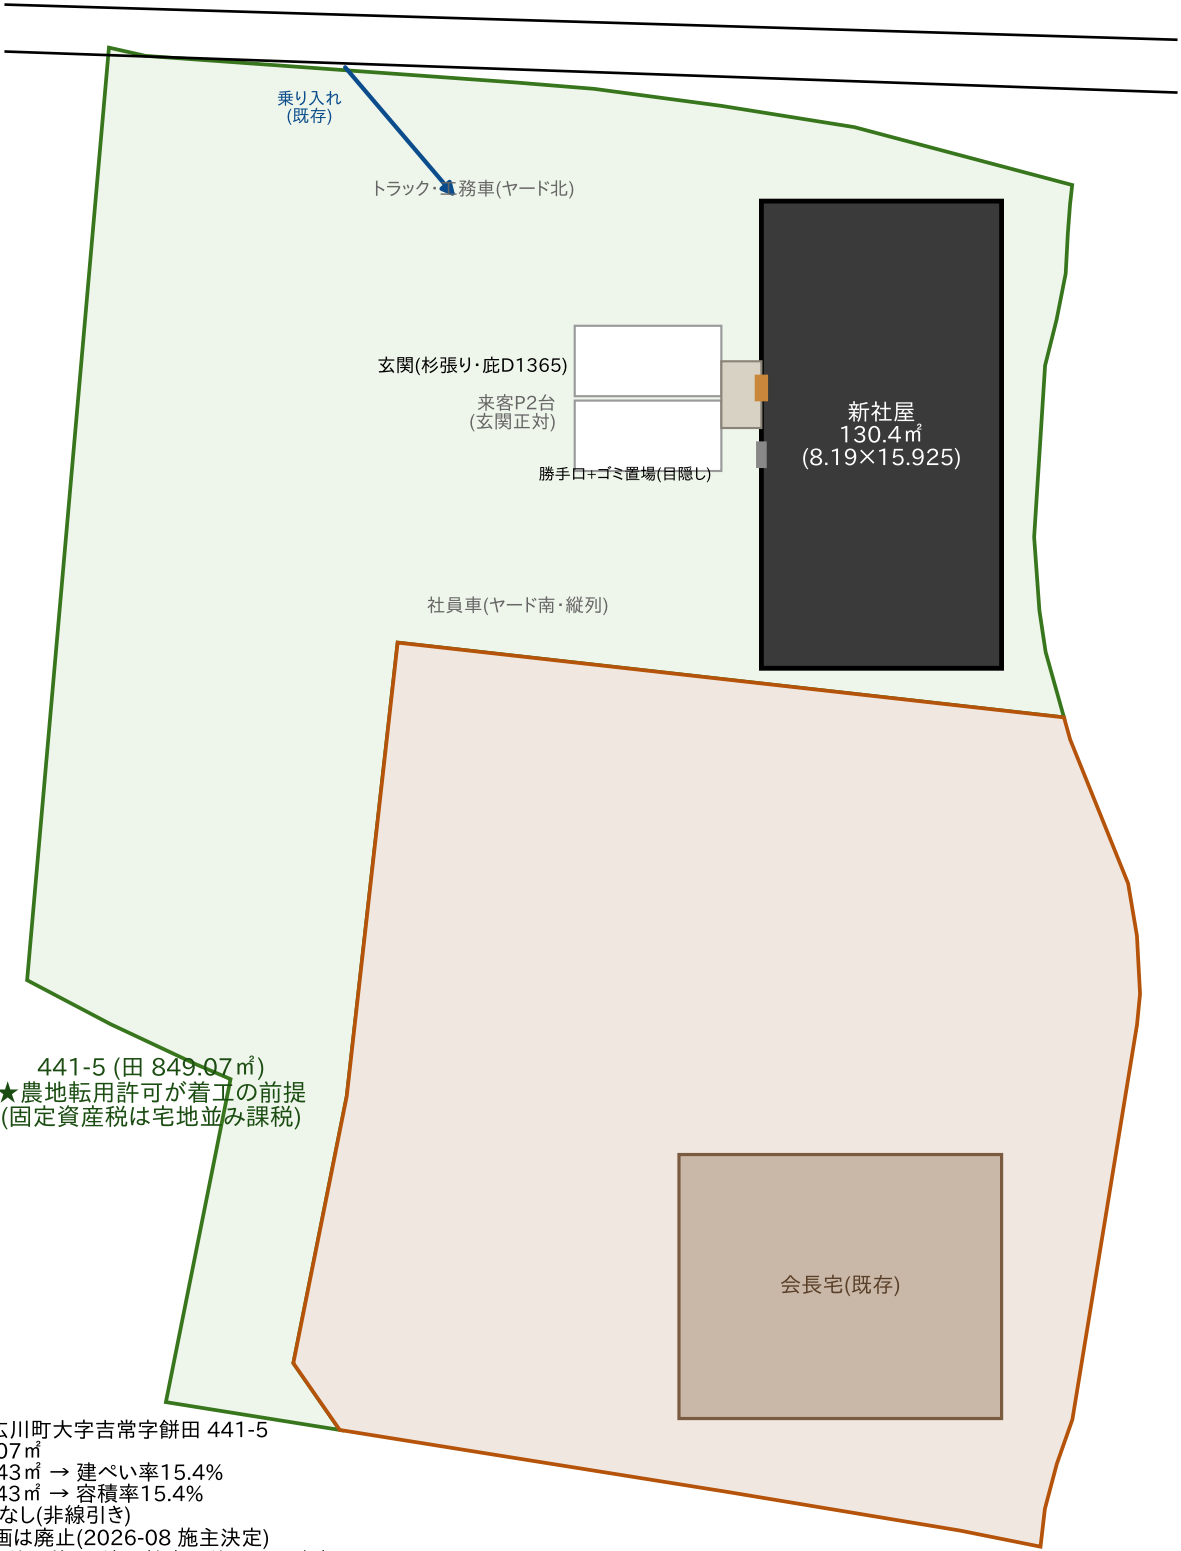

生垣・水路 → 隣地(友野氏・駐車場)

【敷地】八女郡広川町大字吉常字餅田 441-5
敷地面積 849.07㎡
建築面積 130.43㎡ → 建ぺい率15.4%
延べ面積 130.43㎡ → 容積率15.4%
用途地域: 指定なし(非線引き)
※GYM増築計画は廃止(2026-08 施主決定)
※農地転用許可後に着工/境界杭実測後に配置確定


10m

樋口工業有限会社 新社屋新築工事(木造平屋・事務所)

図面名: 配置図

A-01


縮尺 1/250・2026-08-20・計画案v10(部門分室・席名入り)

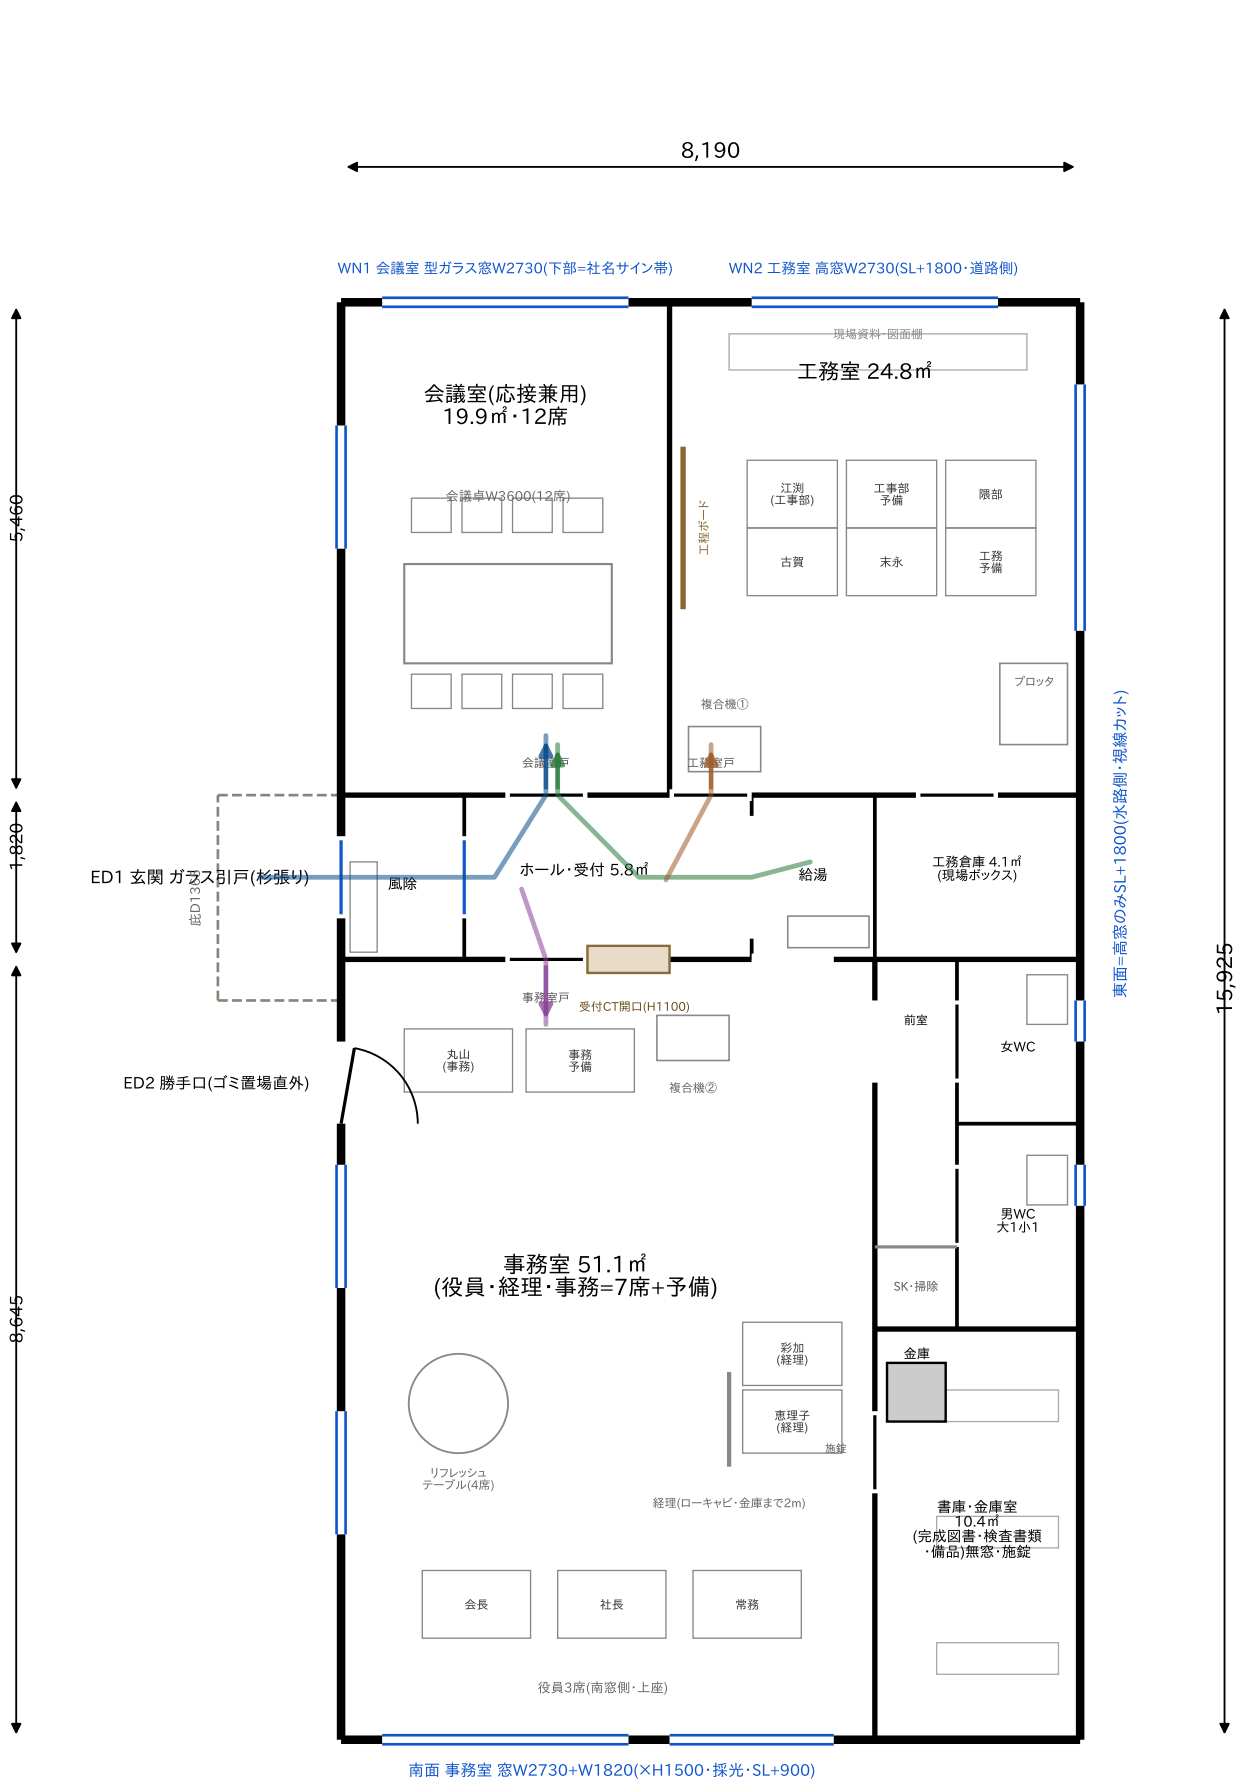


【v10 部門分室(施主指示)】
・会議室/工務室/事務室(役員・経理・事務)をホール受付から別々に分けた
ー 各室に専用の戸。他部門の部屋を通らずに出入りできる
・複合機は工務室と事務室に1台ずつ(①工務=プロッタも同室/②事務)
・席名入り: 会長・社長・常務(南窓側)/経理=彩加・恵理子(金庫まで2m)/
事務=丸山+予備(受付CTの内側)/工務部=江洙+予備・工務=隈部・古賀・
末永+予備(工務室の島6席)
・工務室24.8㎡: 島6席+現場資料棚+工程ボード+工務倉庫4.1㎡直結。
将来増員時は島を8席化できる広さ
・事務室51.1㎡: 7席+予備で1人5.7㎡のゆとり+リフレッシュテーブル
・来客はホール(受付CT)で完結。お茶出しは給湯→ホール→会議室=扉1枚
・WCは事務室側から。書庫・金庫室は経理席の目の前(施錠・無窓)

- 来客動線: 玄関→ホール→会議室(どの部屋にも入らず完結)
 - お茶出し: 給湯→ホール→会議室(扉1枚)
 - 事務室へ: ホールから事務室戸(受付CT開口で着席対応)
 - 工務室へ: ホールから工務室戸(朝夕の出入りが他室を通らない)
- 【面積表(壁芯)130.43㎡=39.5坪】
会議室(応接兼用)19.87/工務室24.84/風除2.48/ホール・受付5.80
給湯2.48/工務倉庫4.14/WC前室(SK)3.73/女WC2.48/男WC3.11
書庫・金庫室10.35/事務室51.14
※FL=GL+450(風除のみ土間)/席: 現12名+予備3(計15席・最大17対応)
※敷地(441-5)は農地転用許可後に着工


樋口工業有限会社 新社屋新築工事(木造平屋・事務所)	
図面名: 平面図	A-02
縮尺 1/100・2026-08-20・計画案v10(部門分室・席名入り)	

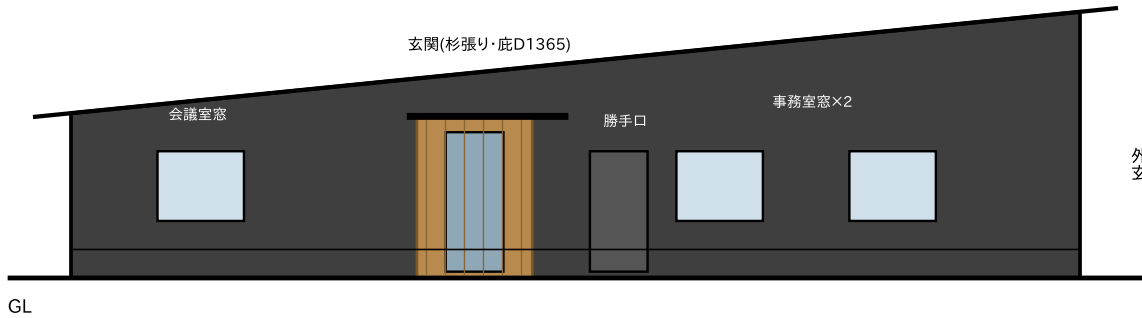


西立面図(ヤード・駐車場側=入口の顔) 1/150

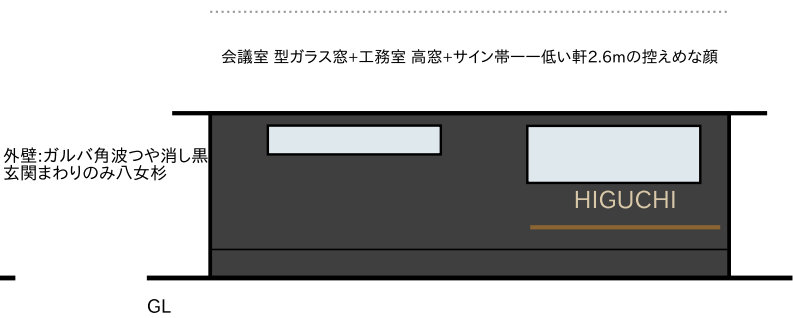

北立面図(道路の顔・出入口なし) 1/150

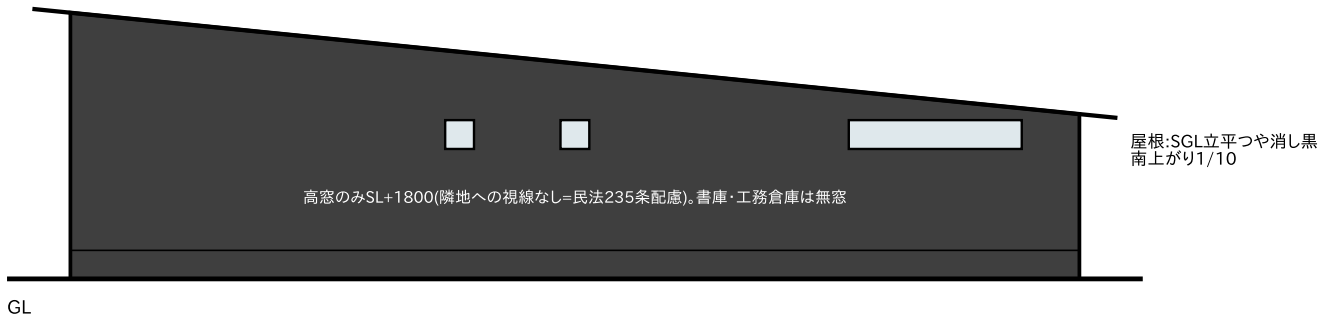


東立面図(生垣・水路側) 1/150

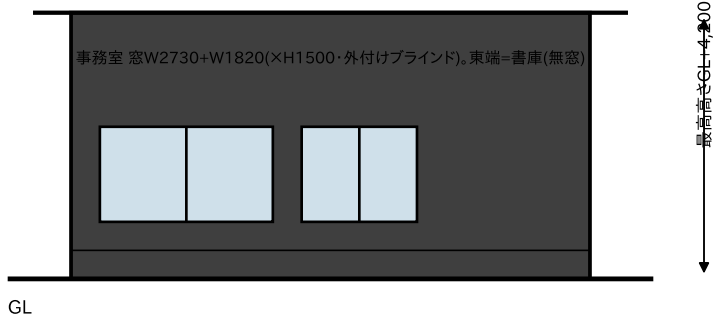

南立面図(採光面) 1/150

樋口工業有限公司 新社屋新築工事(木造平屋・事務所)	
図面名: 立面図(4面)	A-03
縮尺 1/150・2026-08-20・計画案v10(部門分室・席名入り)	

樋口工業有限会社 新社屋新築工事(木造平屋・事務所)	
図面名: 断面図・仕様概要	A-04
縮尺 1/60・2026-08-20・計画案v10(部門分室・席名入り)	

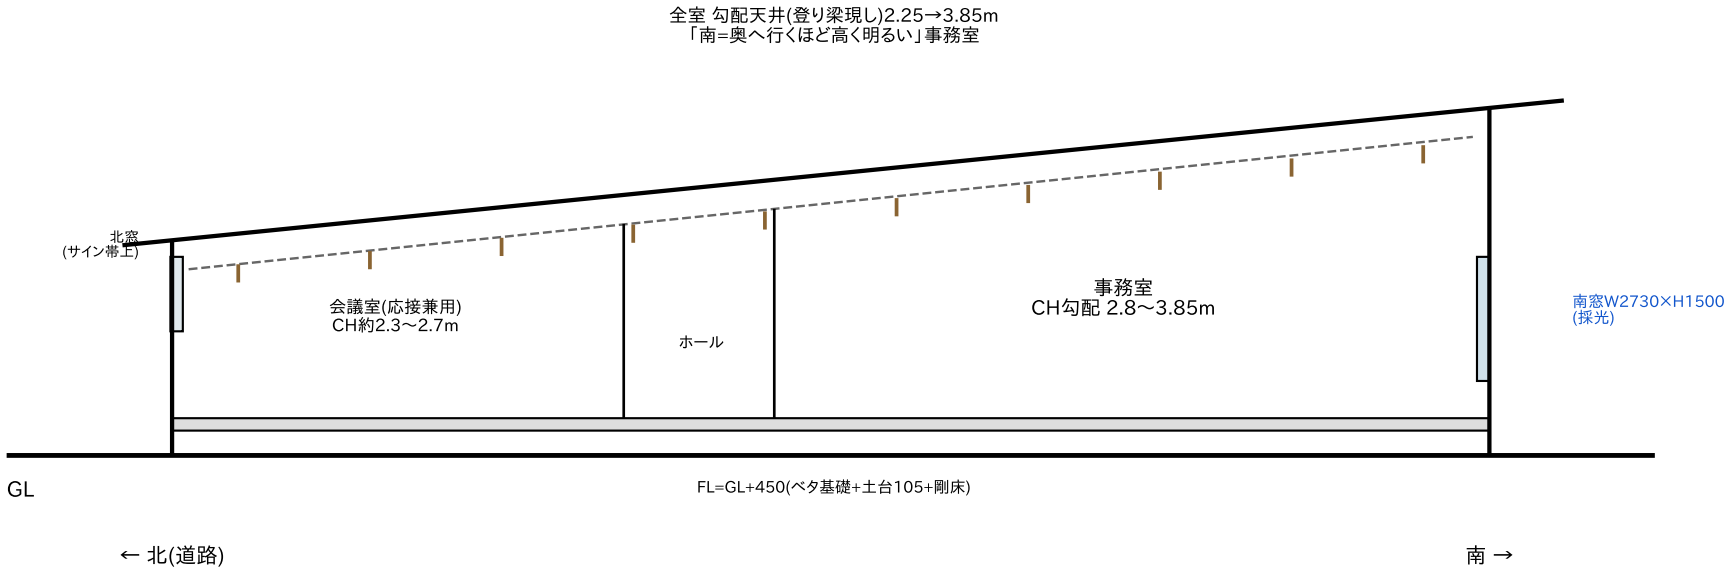


A-A断面図(南北・x=2.3 会議室～ホール～事務室) 1/60

【構造・仕上概要(v10)】
構造: 木造在来・平屋(8.19×15.925m) / 基礎: ベタ基礎 / 壁量: 2025年改正基準(要壁量計算。部門間の間仕切壁を耐力壁に活用=分室化は耐震にも有利)
屋根: SGLガルバ立平つや消し黒・南上がり1/10(北軒GL+2.6→南壁GL+4.2) / 外壁: ガルバ角波つや消し黒+玄関まわりのみ八女杉
サッシ: アルミ樹脂複合 黒 / 断熱: 屋根HGW16K155×2・壁HGW16K105・基礎XPS50 / 天窓なし
内装: 事務・工務=登り梁現し+タイルカーペット / 会議室=杉板1面壁 / ホール=モルタル金鏝+受付CT / 書庫=可動棚・無窓・施錠
外構(自社施工=原価): 舗装+白線・来客P2台・社名サイン・電球色2700K / 設備: 24h換気3種・エアコン(事務1・工務1・会議1)・LAN Cat6A
水回り集約: WCブロック+給湯を中央の1系統に=配管最短・コスト減 / 南・西窓は外付けブラインドで日射対策
※GYM増築計画は廃止 ※屋根北流れ=太陽光不向き ※建設地(441-5)は農地転用許可が前提 ※最終確認は設計者(建築士)による

外観イメージ(北西=道路・ヤード側から)

「黒い箱に、八女杉の玄関」

- ・つや消し黒のガルバの箱。玄関まわりだけ八女杉=樋口工業の顔
- ・玄関に庇D1365: 来客Pから2〜3歩、雨に濡れずに入れる
- ・道路側(左)は会議室の型ガラス窓+工務室の高窓+社名サイン帯
- ・屋根は南へ登る片流れ: 事務室の奥ほど天井が高く明るい
- ・白線の駐車場・舗装は自社施工=施工品質がそのまま名刺になる
- ・夜は電球色2700Kでポーチとサインだけ照らす

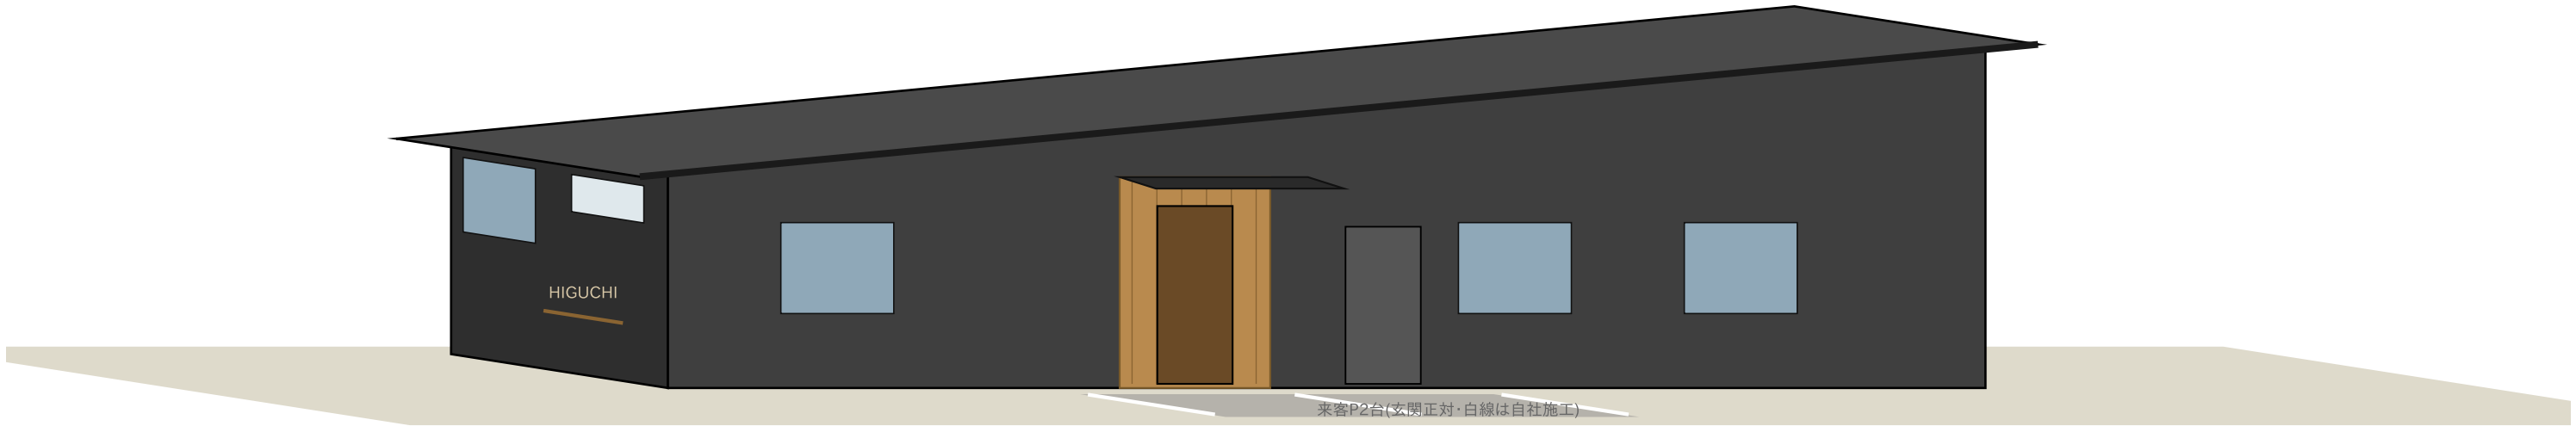

樋口工業有限会社 新社屋新築工事(木造平屋・事務所)

図面名: 外観イメージ

A-05

縮尺 NTS・2026-08-20・計画案v10(部門分室・席名入り)