



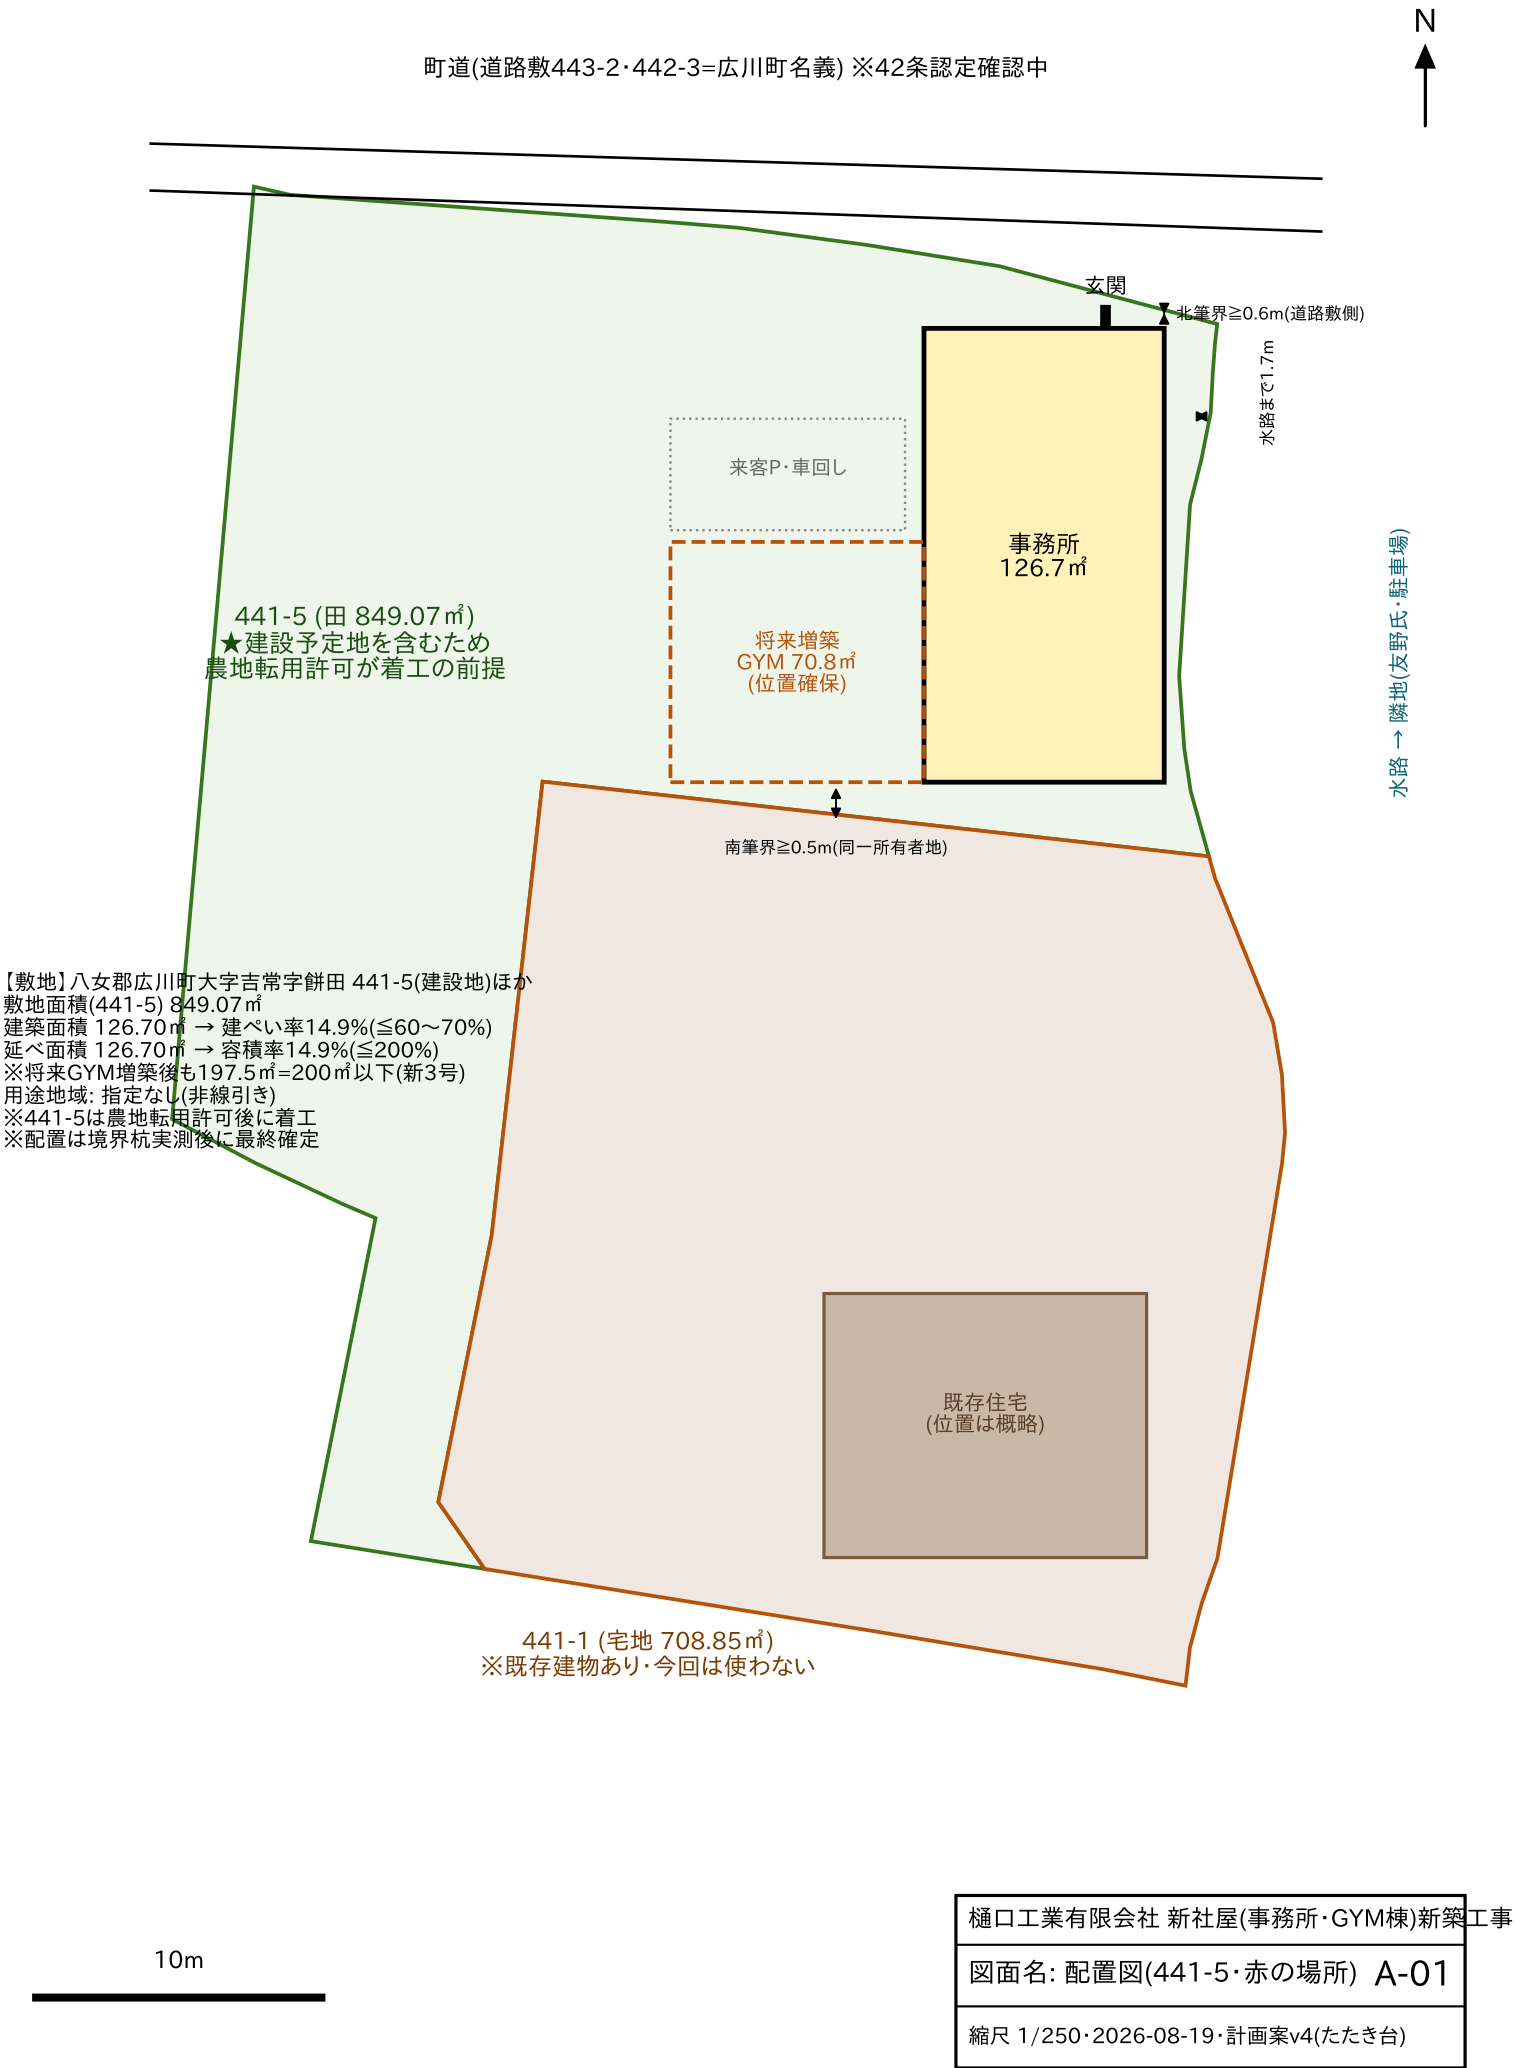

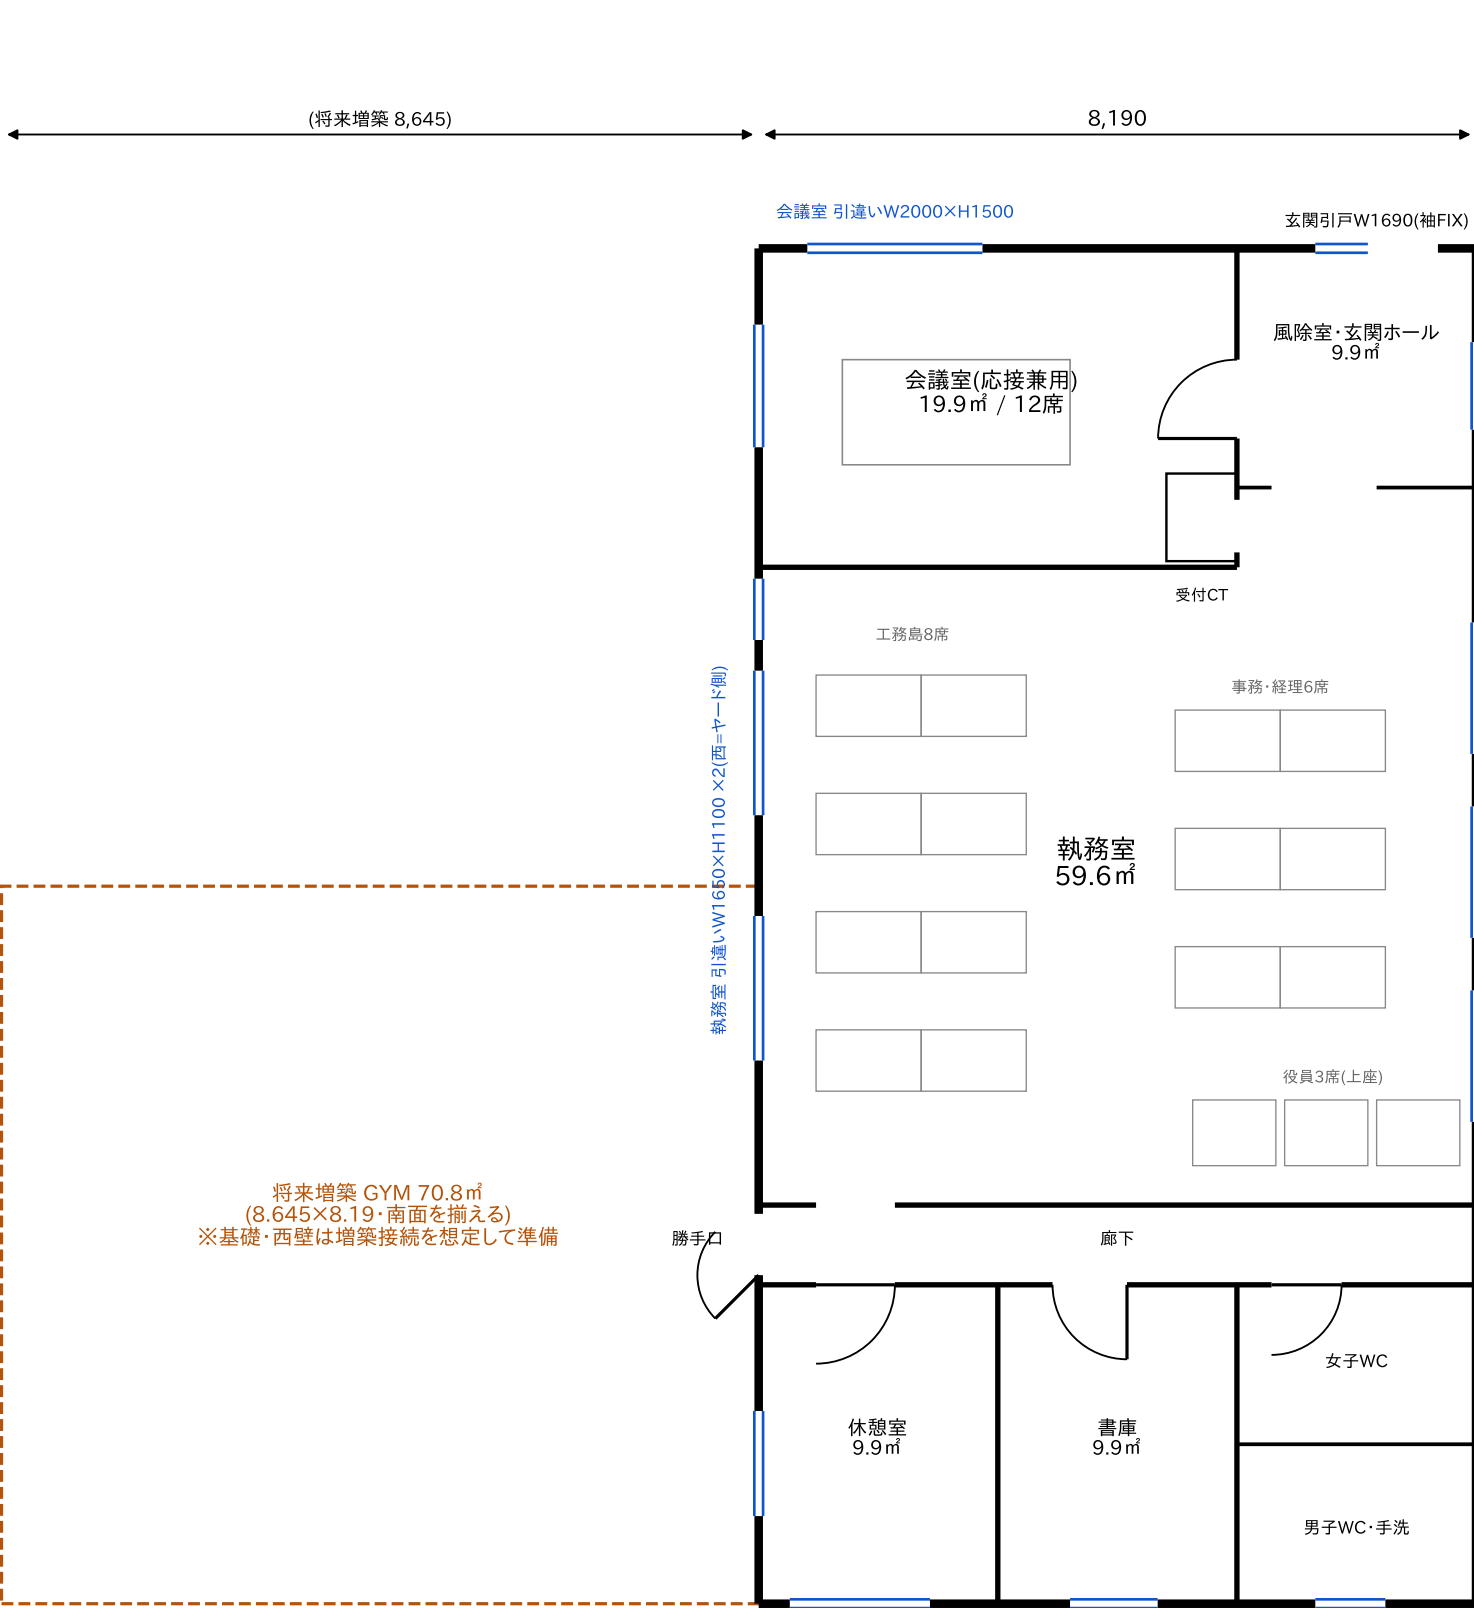

N

【平面計画の要点(v4=事務所単独先行)】


- ・単純な長方形1棟(8.19×15.47m)=施工・雨仕舞い最简单
- ・玄関=北面(道路からすぐ)
- ・来客: 玄関→ホール→会議室(執務を通らない)
- ・会議室は北窓=道路側で明るい
- ・執務室: 東窓は型板ガラス(隣地P側)/西窓はヤード側で明るい
- ・水回りは南帯に集約 / 勝手口=廊下西端
- ・GYM(70.8㎡)は将来増築: 西側に位置確保、基礎・西壁下地・電気容量を増築前提で準備

【面積表(壁芯)】


事務所 126.70㎡ (38.3坪)

(将来GYM増築後 197.51㎡=200㎡以下・新3号維持)


※敷地(441-5)は農地転用許可後に着工

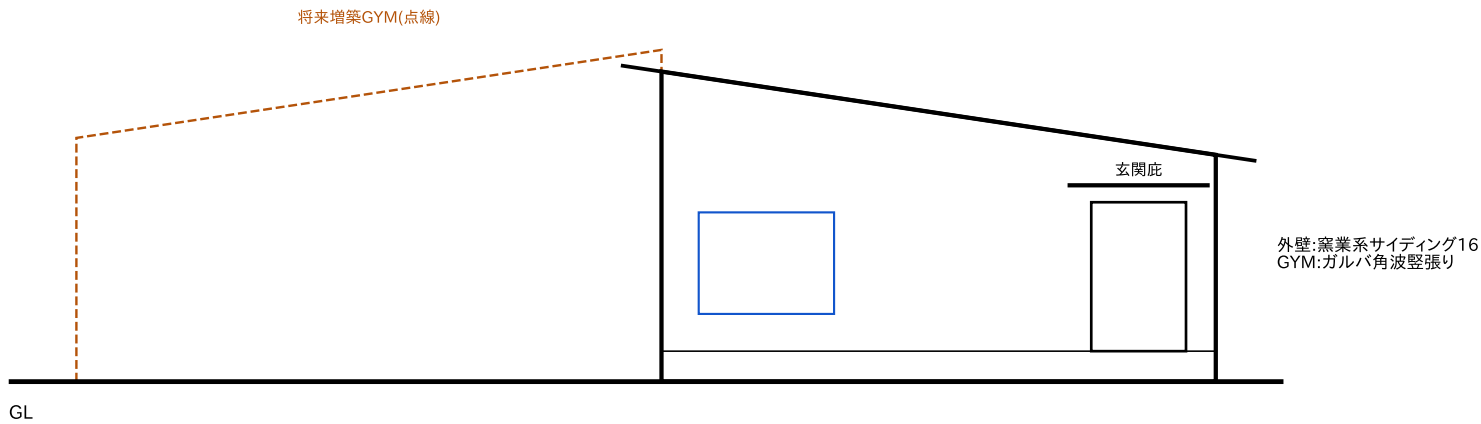


北立面図(道路側) 1/150

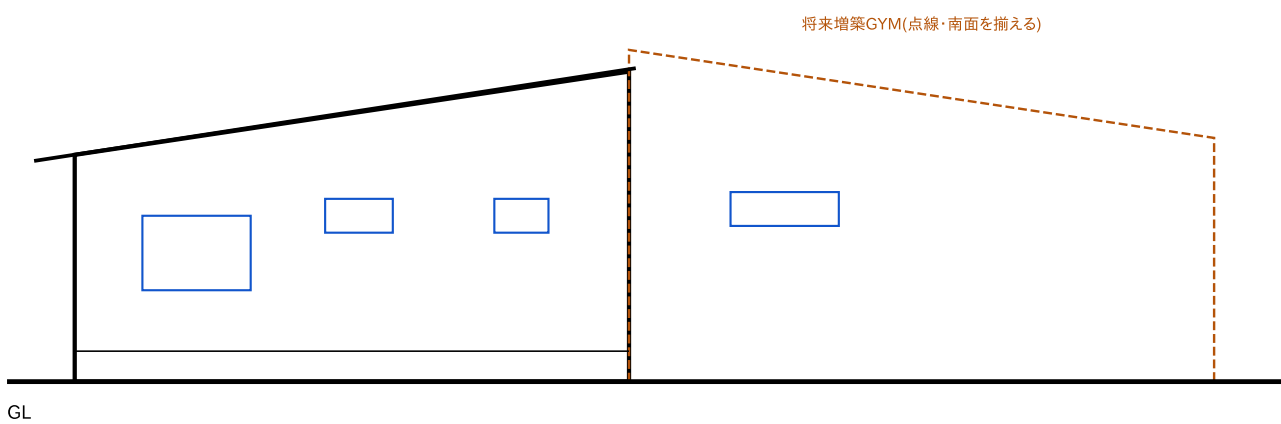

南立面図 1/150

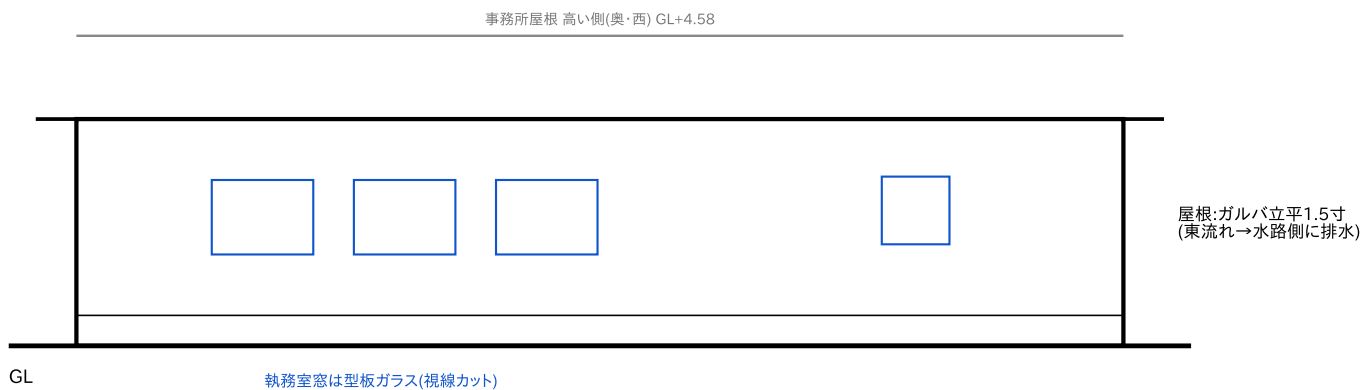


東立面図(隣地駐車場側) 1/150

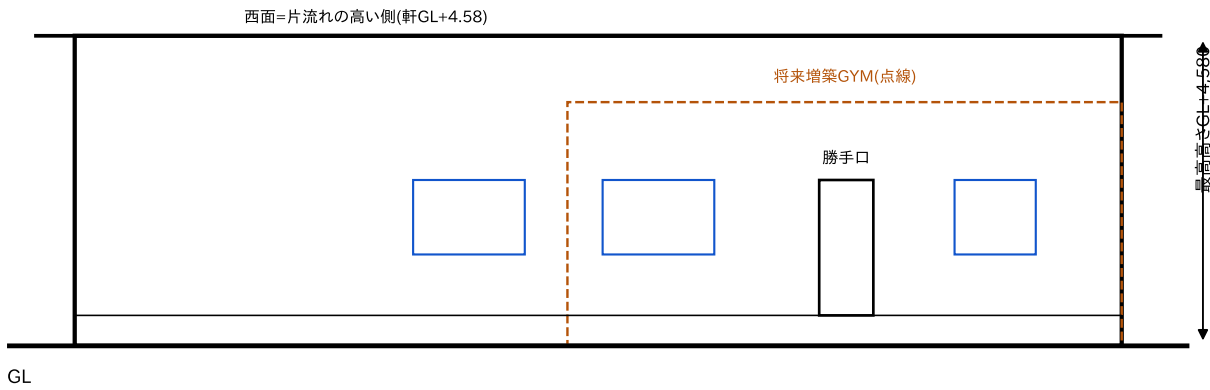

西立面図(ヤード側) 1/150

樋口工業有限会社 新社屋(事務所・GYM棟)新築工事	
図面名: 断面図・仕様概要	A-04
縮尺 1/60・2026-08-19・計画案v4(たたき台)	

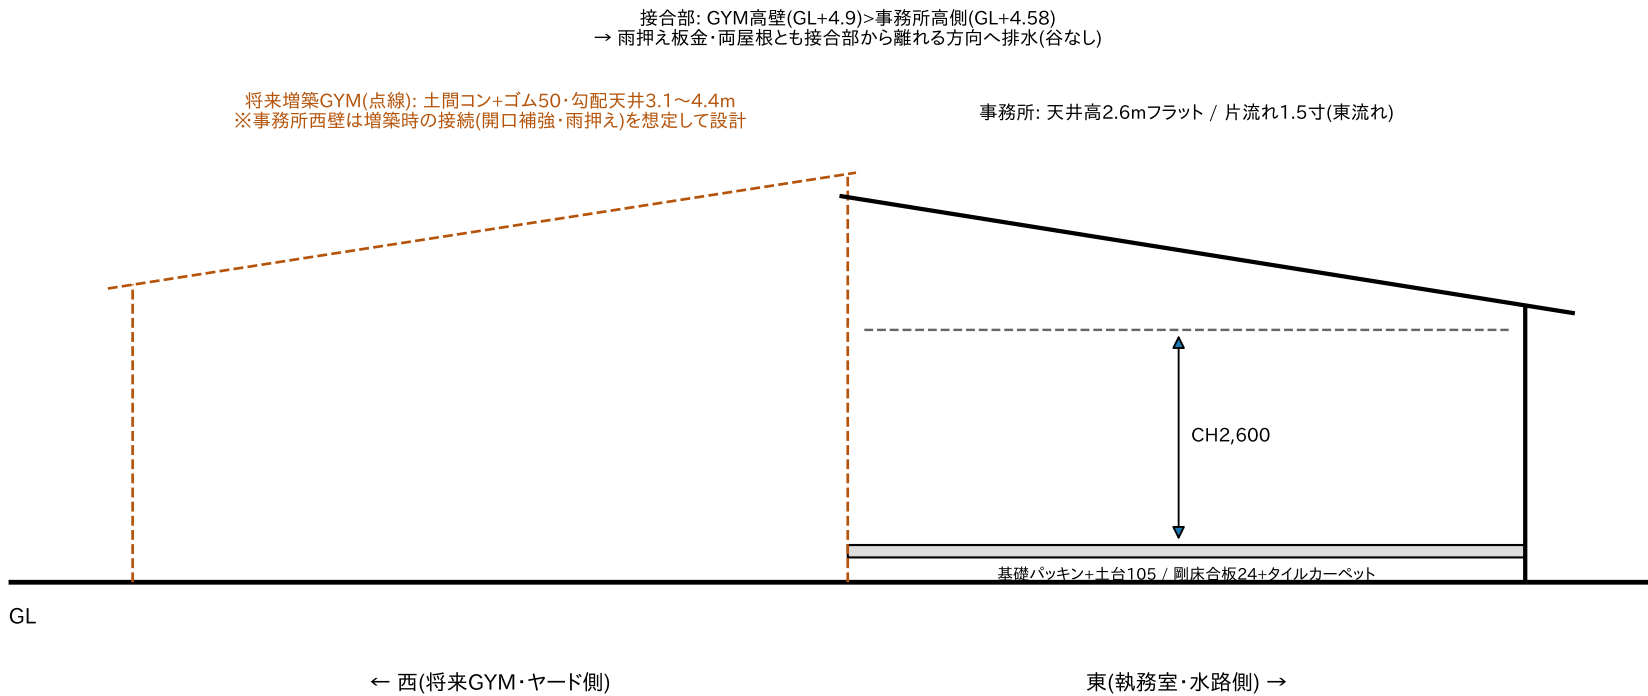

A-A断面図(東西) 1/60

【構造・仕上概要(たたき台)】

構造: 木造在来軸組・平屋 / 基礎: ベタ基礎(GYM部は土間一体・機材アンカー対応配筋)
壁量: 2025年改正基準による壁量計算(構造用合板9mm N50@150 外周耐力壁)
屋根: ガルバリウム鋼板立平葺き1.5寸 / 軒の出600 / 事務所=東流れ・GYM=西流れ
外壁: 窯業系サイディング16(事務所)+ガルバ角波縦張り(GYM)・通気工法
断熱: 屋根HGW16K155×2層 / 壁HGW16K105 / 基礎・土間XPS50 / サッシ アルミ樹脂複合Low-E
内装: PB12.5+塗装(AEP)・タイルカーペット(執務)
設備: 24h換気(3種) / エアコン執務2・会議1 / LAN Cat6A / 照明LED / 分電盤・給排水は将来GYM増築分の容量を確保
※建設地(441-5)は農地転用許可が着工の前提。※本図は実施設計前の計画案。最終確認は設計者(建築士)による。