



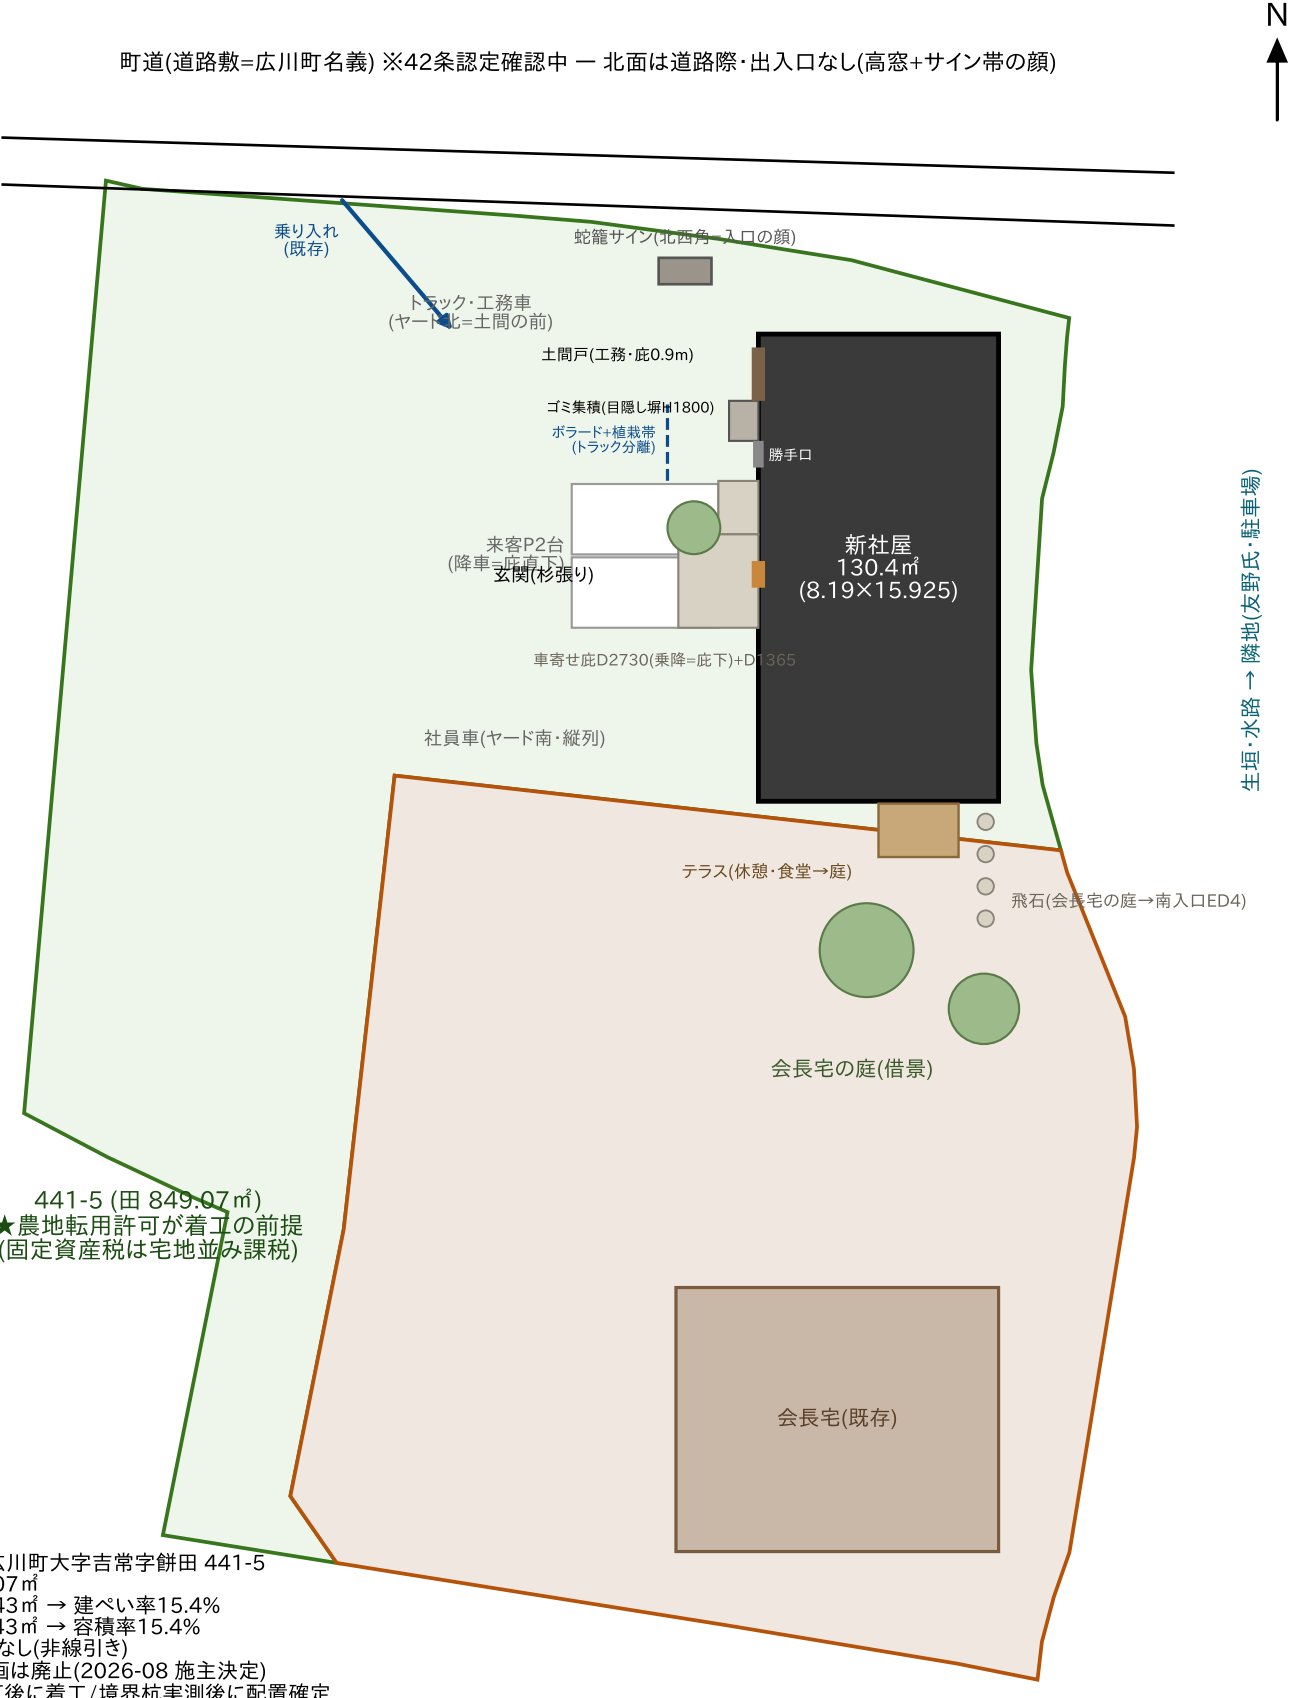

【敷地】八女郡広川町大字吉常字餅田 441-5
敷地面積 849.07㎡
建築面積 130.43㎡ → 建ぺい率15.4%
延べ面積 130.43㎡ → 容積率15.4%
用途地域: 指定なし(非線引き)
※GYM増築計画は廃止(2026-08 施主決定)
※農地転用許可後に着工/境界杭実測後に配置確定

樋口工業有限会社 新社屋新築工事「泥・紙・もてなしの三層」	
図面名: 配置図	A-01
縮尺 1/250・2026-08-20・計画案v8.1(UX要求適合+辛口批評反映)	

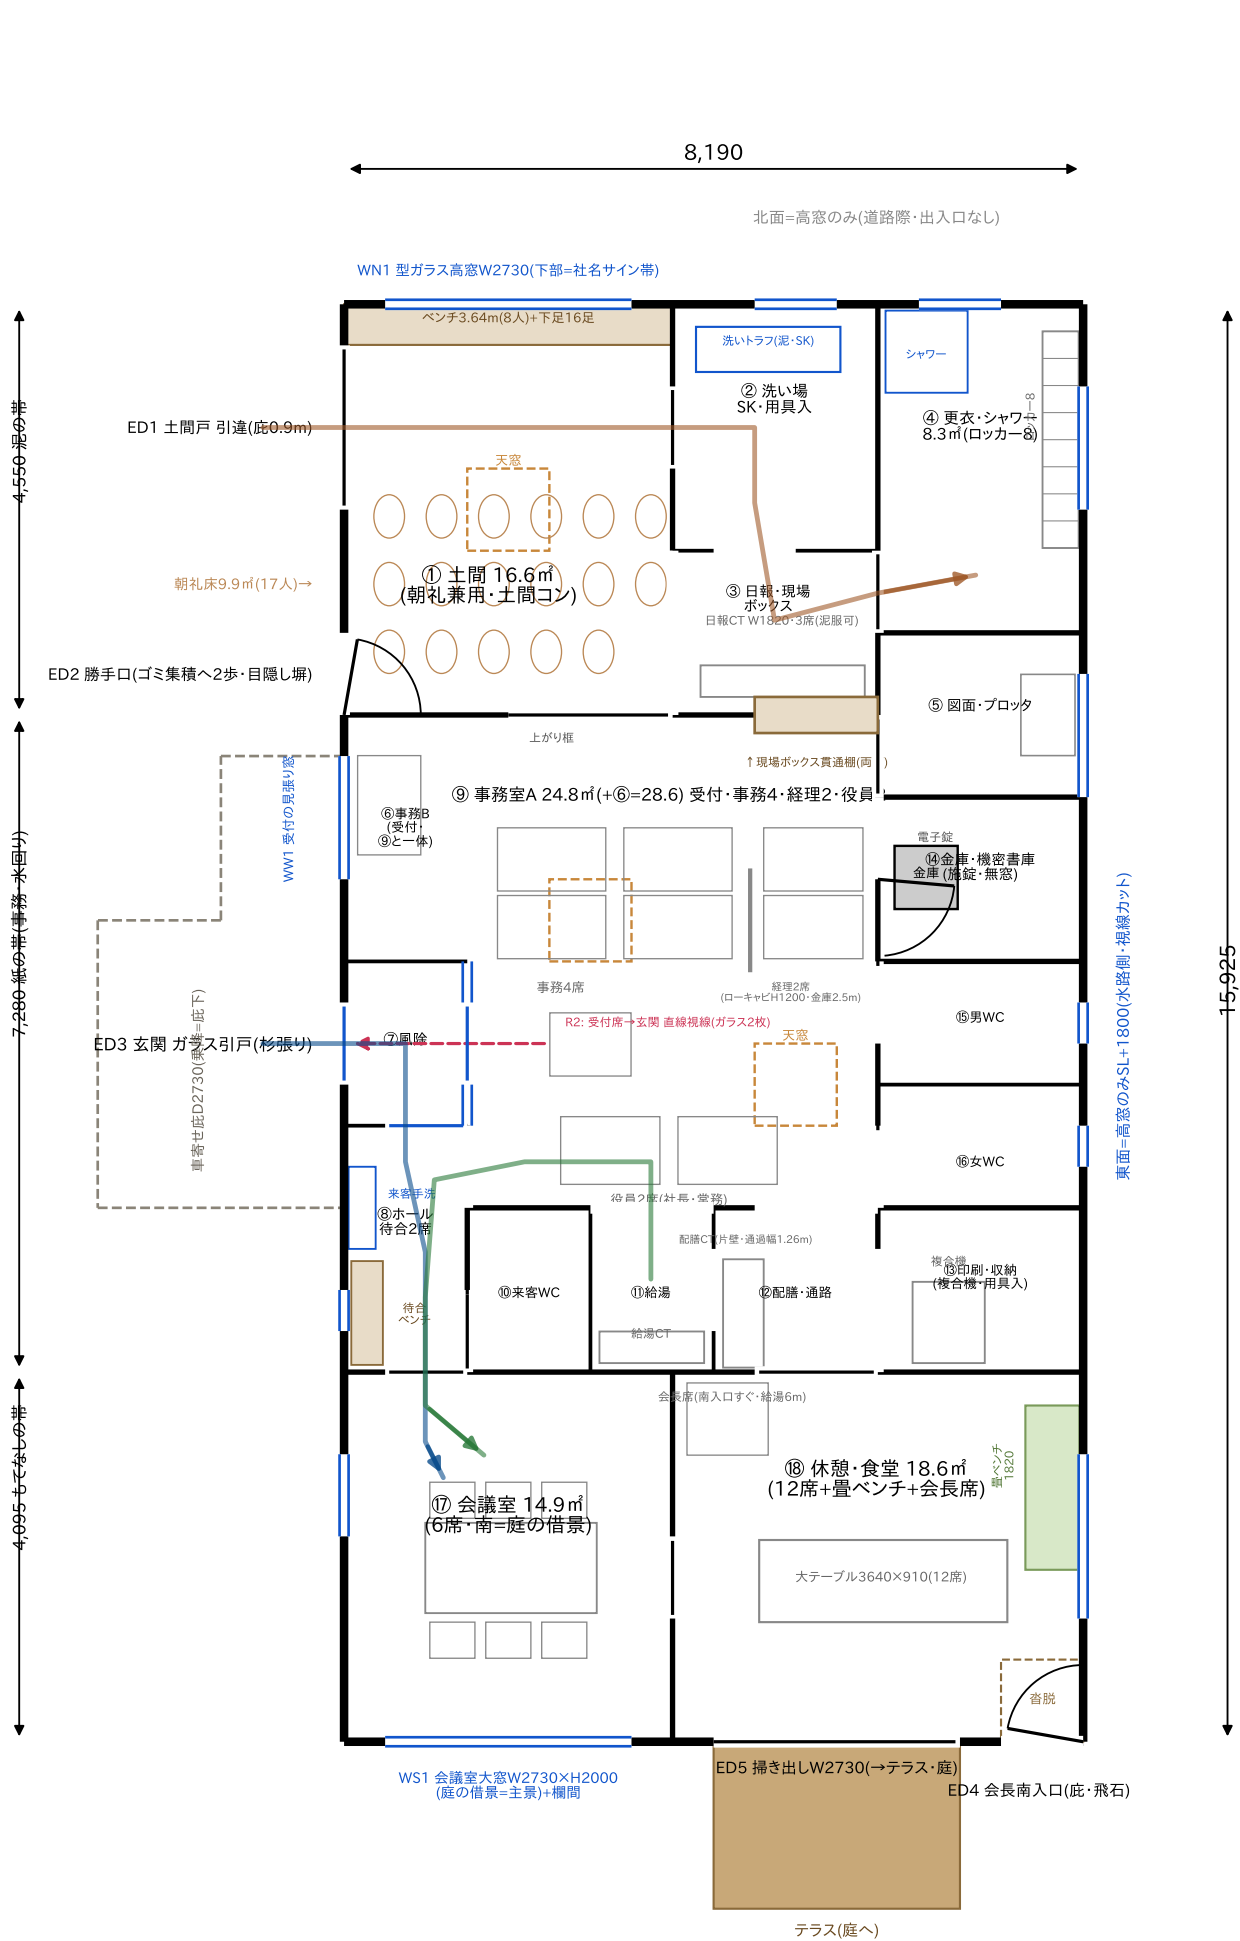

【v8「泥・紙・もてなしの三層」UX要求R1～R25適合】

- ・北端=泥(土間・洗い場・日報・更衣=現場ステーション)/中央=紙(事務・金庫)/南端=もてなし(会議・休憩=庭)
- ・名前付き廊下はホール3.73㎡のみ(R1)。廊下Bは存在しない
- ・受付席から玄関へガラス2枚越しの直線視線2.7m(R2)+西窓で車の接近も見える
- ・来客WC: 会議室から曲がり1回・ホールから戸が見える(R3)
- ・土間16.6㎡=朝礼17人(R7)+8人同時履替え(ベンチ3.64㎡・R4)
- ・泥動線: 土間→洗い場SK→日報CT→更衣を上足床0歩で完結(R5)
- ・休憩・食堂は南面=庭直結(R9)。食事席は休憩15+会議6=21席(R8)
- ・金庫は経理席から2.5m・無窓の行き止まり室(R10)
- ・会長: 南入口ED4→定位置→給湯6m。会議室へはID21で2歩(R13/R24)
- ・雨天: 車寄せ庇D2730=乗降が庇の下。風除は玄関引戸(R19)
- ・玄関と土間戸は5.46m離隔+植栽(R20)/ポストは玄関脇(R21)

【辛口批評(第三者)反映済み】ゴミ集積をED1・ED2間へ移設(来客Pから1.4m+目隠し堀)/WC引戸は戸袋位置まで確定(袖壁廃止)/⑫は配膳・通路専用(複合機は⑬へ)/⑰⑱連絡戸ID21新設/給湯⇄配膳ID22直結/ID9戸袋はホール側Y10.01～10.92=受付視線帯を塞がない

- 泥動線: 土間→洗い場→日報→更衣(上足床0歩・R5)
- 来客動線: 玄関→ホール→会議室(来客WCは右手・R3)
- お茶出し: 給湯→事務A→ホール→会議室 約7m・扉1枚(R12)

【面積表(壁芯)130.43㎡=39.5坪】

①土間16.56 ②洗い場SK6.21 ③日報4.14 ④更衣シャワー=8.28 ⑤図面4.14

⑥事務B3.73 ⑦風除2.48 ⑧ホール3.73 ⑨事務A24.84 ⑩来客WC2.48


⑪給湯2.48 ⑫配膳3.31 ⑬印刷収納4.14 ⑭金庫書庫4.14 ⑮男WC3.11

⑯女WC3.11 ⑰会議14.90 ⑱休憩食堂18.63


※床: ①～④=土間コン(FL=GL+150)/他=上足(FL=GL+450)

※敷地(441-5)は農地転用許可後に着工


樋口工業有限会社 新社屋新築工事「泥・紙・もてなしの三層」	
図面名: 平面図	A-02
縮尺 1/100・2026-08-20・計画案v8.1(UX要求適合+辛口批評反映)	

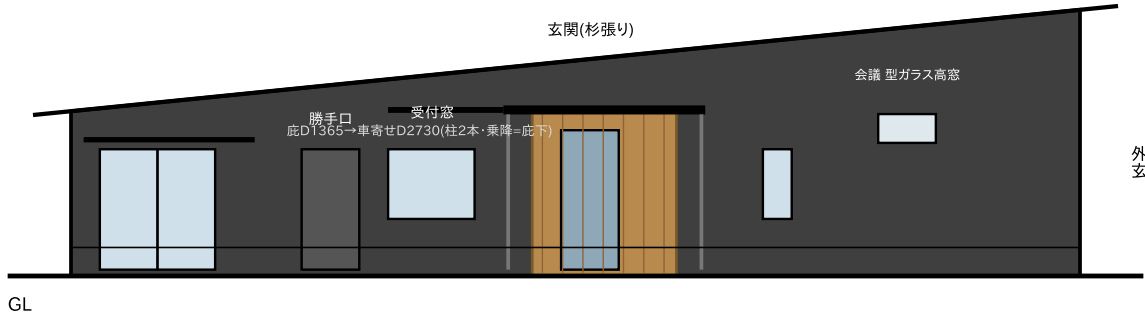


西立面図(ヤード・駐車場側=入口の顔) 1/150

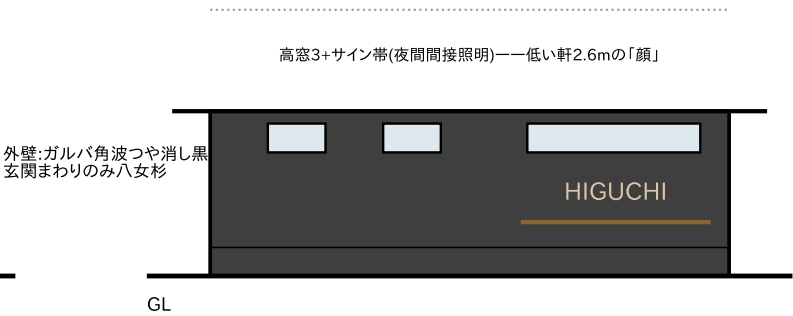

北立面図(道路の顔・出入口なし) 1/150

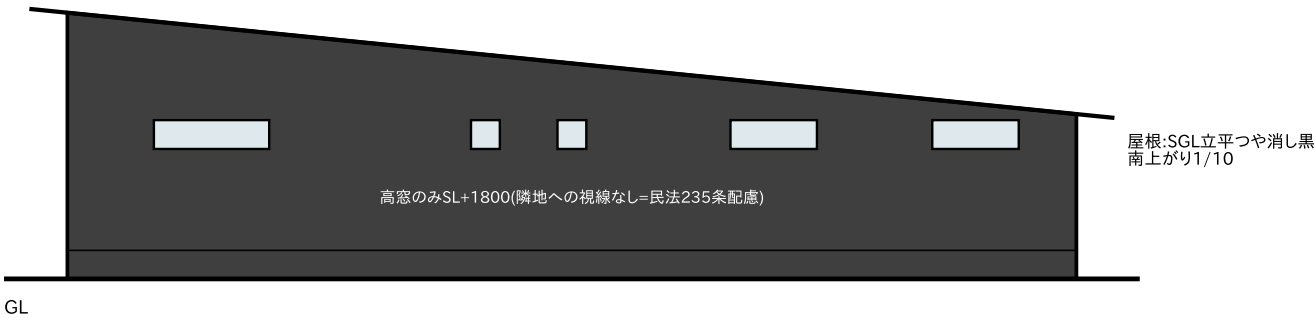


東立面図(生垣・水路側) 1/150

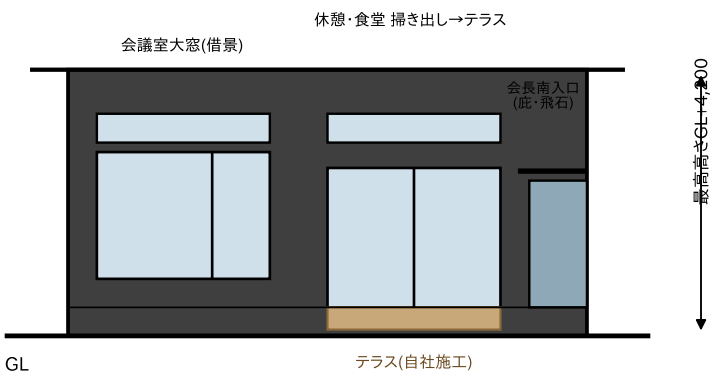

南立面図(庭・借景側) 1/150

樋口工業有限会社 新社屋新築工事「泥・紙・もてなしの三層」	
図面名: 立面図(4面)	A-03
縮尺 1/150・2026-08-20・計画案v8.1(UX要求適合+辛口批	

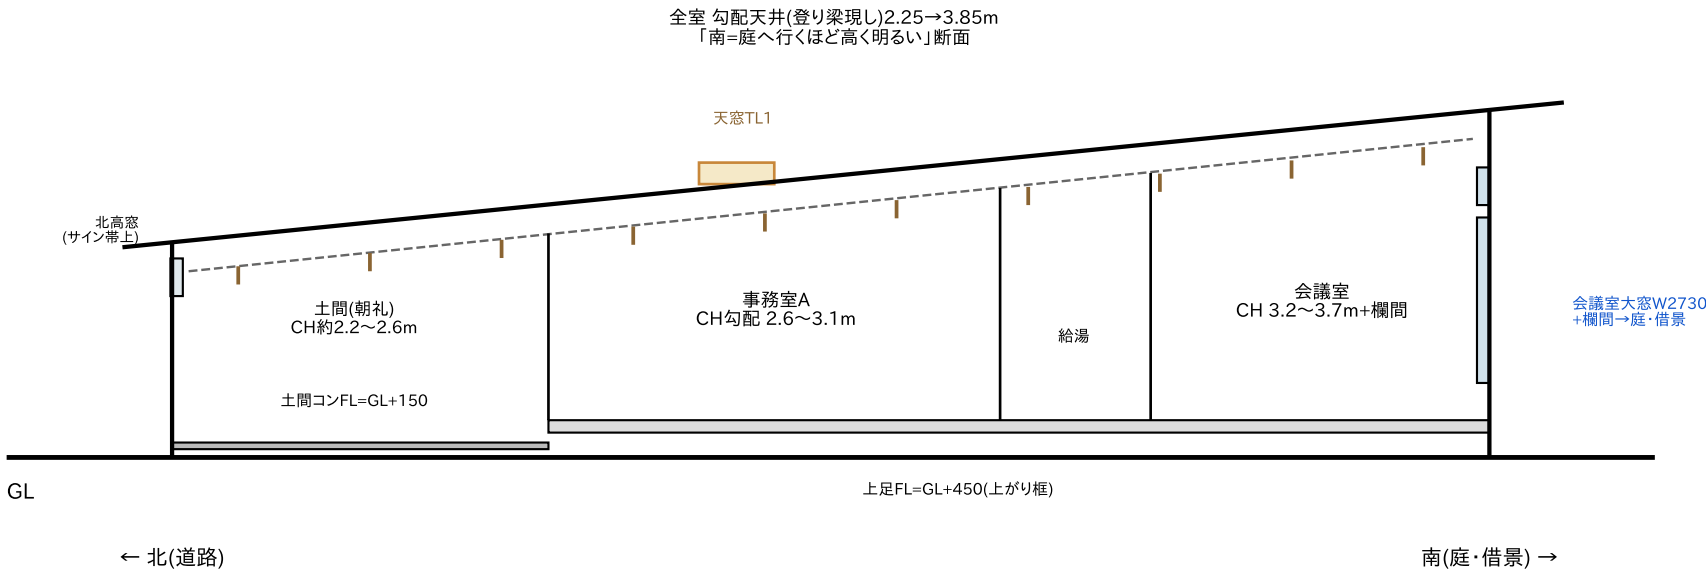

A-A断面図(南北・x=3.0 土間~事務A~給湯~会議室) 1/60

【構造・仕上概要(v8)】

構造: 木造在来・平屋(8.19×15.925m) / 基礎: ベタ基礎(土間帯は一体打ち) / 壁量: 2025年改正基準(南面大開口の耐力は金庫・WC・収納回りの耐力壁で補完・要壁量計算)

屋根: SGLガルバ立平つや消し黒・南上がり1/10(北軒GL+2.6の低い顔→南壁GL+4.2) / 外壁: ガルバ角波つや消し黒+玄関まわりのみハ女杉(3色で止める)

サッシ: アルミ樹脂複合 黒 / 断熱: 屋根HGW16K155×2・壁HGW16K105・基礎XPS50 / 天窓: FIX断熱型910角×3(事務A×2・土間×1)

内装: 事務=構造現し+腰壁合板+タイルカーペット / 土間・洗い場・日報=土間コン金鍍(泥ゾーン) / 会議=杉板1面壁 / ホール=モルタル金鍍+施工事例パネル

外構(自社施工=原価): 舗装+白線・ボラード+植栽帯(来客P/トラック分離)・蛇籠サイン(北西角)・アオダモ・南テラス・飛石・電球色2700K


設備: 24h換気(事務系=1種熱交換・泥/WC系=3種で系統分離) / エアコン事務2・会議1・休憩1 / LAN Cat6A / 給排水は泥系+WC系の2系統

※GYM増築計画は廃止(2026-08施主決定) ※屋根は北流れ=太陽光不向き ※建設地(441-5)は農地転用許可が前提 ※西面ガラスは外付け日射遮蔽・南欄間に庇D910(福岡の西日・夏対策) ※車寄せ庇D2730は建築面積算入を実施設計で確認 ※最終確認は設計者(建築士)による

外観イメージ(北西=道路・ヤード側から)

「黒い箱に、八女杉の切り欠き」

- ・車寄せ庇D2730: 降りる瞬間から頭上に屋根、杉張りの玄関へ
- ・北端(左)は工務の土間戸: トラックから3歩で土間・朝礼へ
- ・玄関と土間戸の間に受付の見張り窓: 来客の車が見える
- ・左手前=蛇籠サイン(八女石+切文字)、庇の際にアオダモ
- ・道路側(左奥)は高窓+サイン帯: 低い軒2.6mの控えめな顔
- ・屋根は南(右)へ伸び上がる: 庭に向かって開く断面
- ・白線ビシッの駐車場・ポラード+植栽帯=自社施工の名刺
- ・夜は電球色2700K: ポーチ・蛇籠・アオダモだけ照らす

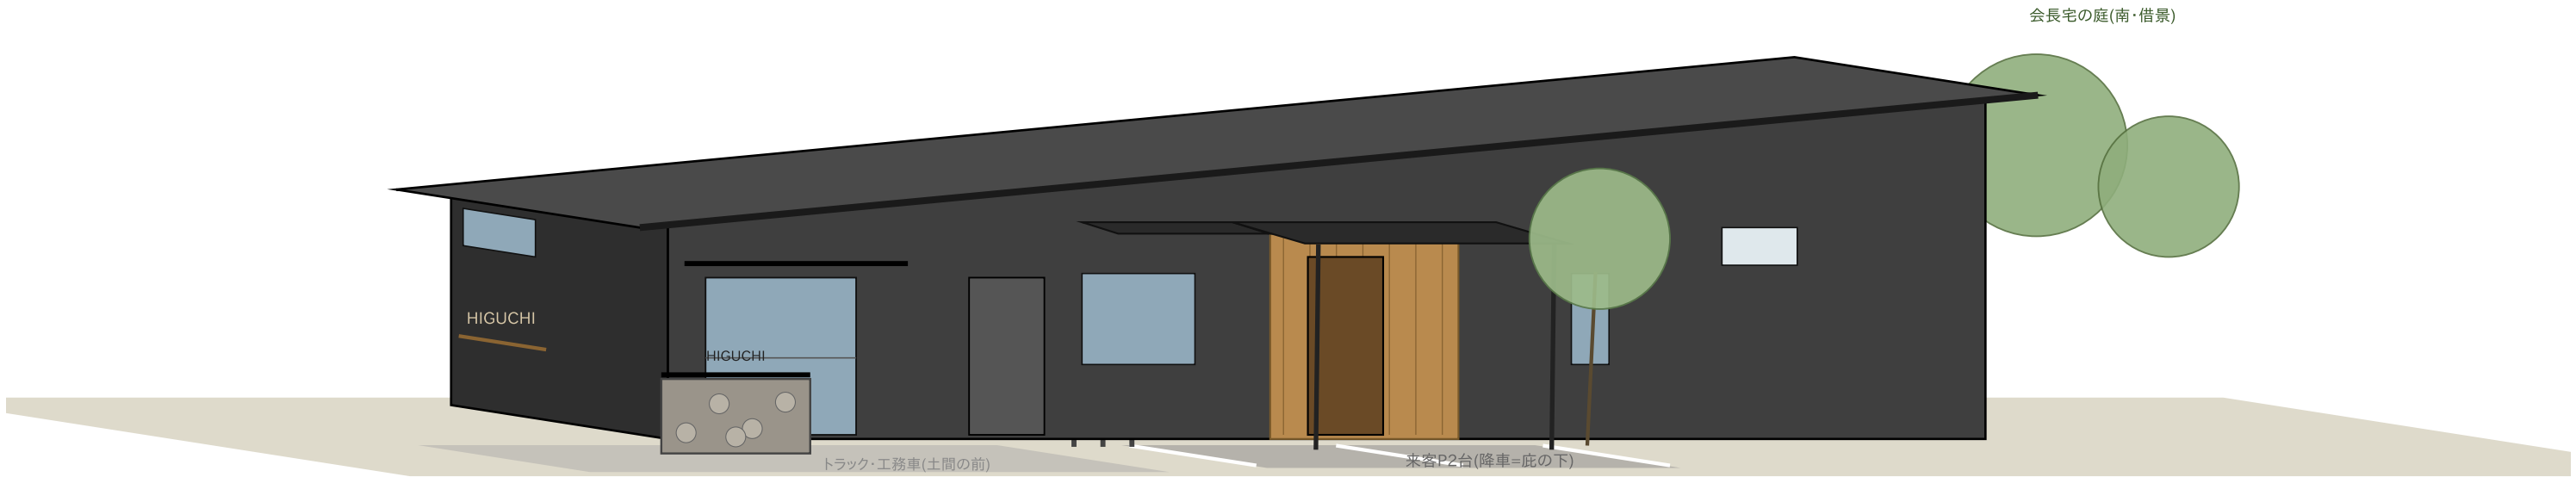

樋口工業有限会社 新社屋新築工事「泥・紙・もてなしの三層」

図面名: 外観イメージ A-05

縮尺 NTS・2026-08-20・計画案v8.1(UX要求適合+辛口批評反映)