


町道(道路敷=広川町名義) ※42条認定確認中 ― 北面は道路際・出入口なし(窓+サイン帯)

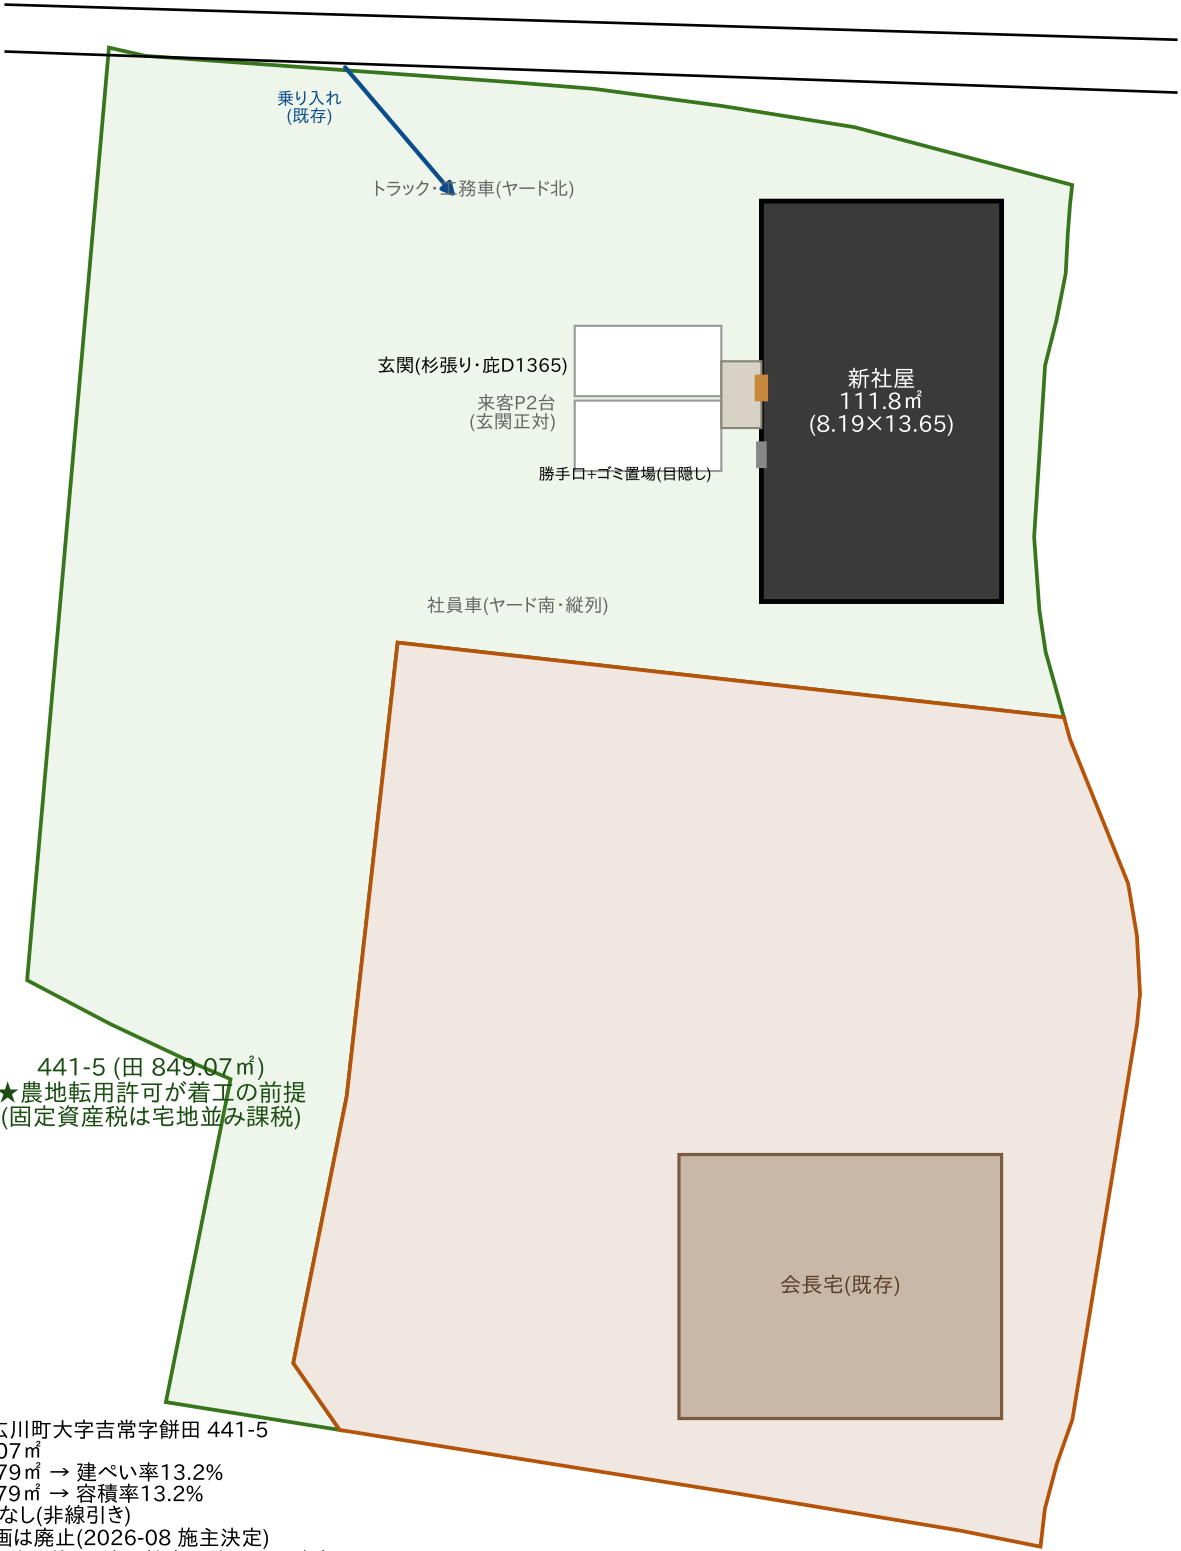

生垣・水路 → 隣地(友野氏・駐車場)

441-5 (田 849.07㎡)  
★農地転用許可が着工の前提  
(固定資産税は宅地並み課税)

【敷地】八女郡広川町大字吉常字餅田 441-5  
敷地面積 849.07㎡  
建築面積 111.79㎡ → 建ぺい率13.2%  
延べ面積 111.79㎡ → 容積率13.2%  
用途地域: 指定なし(非線引き)  
※GYM増築計画は廃止(2026-08 施主決定)  
※農地転用許可後に着工/境界杭実測後に配置確定

10m


|                                          |      |
|------------------------------------------|------|
| 樋口工業有限会社 新社屋新築工事(木造平屋・事務所)               |      |
| 図面名: 配置図                                 | A-01 |
| 縮尺 1/250・2026-08-20・計画案v11(B案=111.8㎡に縮小) |      |

N  
↑



【面積表(壁芯)111.79㎡=33.8坪】  
会議室(応接兼用)19.87/工務室24.84/風除2.48/ホール・受付5.80  
給湯2.48/倉庫4.14/WC前室(SK)3.73/女WC2.48/男WC3.11  
書庫・金庫室7.25/事務室35.61  
※FL=GL+450(風除のみ土間)/席:現12名+予備3(計15席)  
※敷地(441-5)は農地転用許可後に着工


|                                          |      |
|------------------------------------------|------|
| 樋口工業有限会社 新社屋新築工事(木造平屋・事務所)               |      |
| 図面名: 平面図                                 | A-02 |
| 縮尺 1/100・2026-08-20・計画案v11(B案=111.8㎡に縮小) |      |

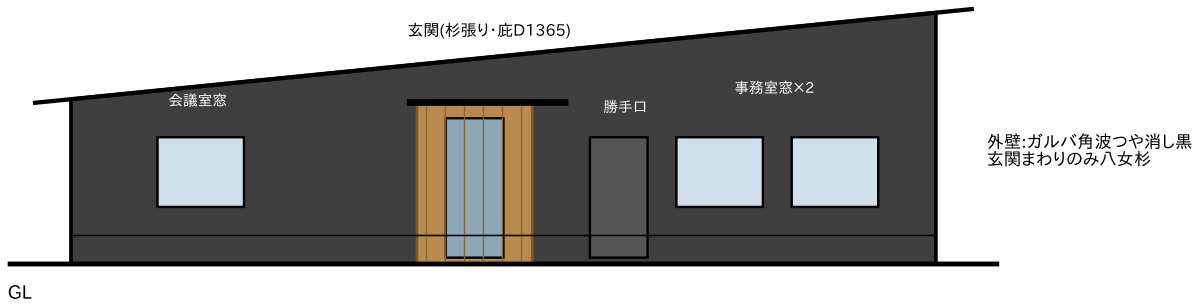


西立面図(ヤード・駐車場側=入口の顔) 1/150



北立面図(道路の顔・出入口なし) 1/150

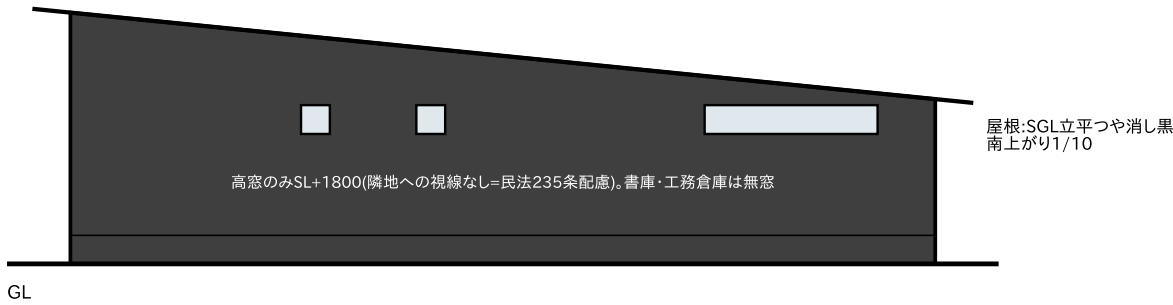

東立面図(生垣・水路側) 1/150

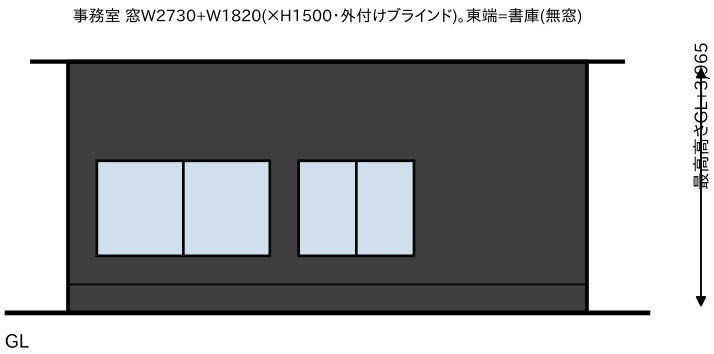


南立面図(採光面) 1/150

|                                          |      |
|------------------------------------------|------|
| 樋口工業有限会社 新社屋新築工事(木造平屋・事務所)               |      |
| 図面名: 立面図(4面)                             | A-03 |
| 縮尺 1/150・2026-08-20・計画案v11(B案=111.8㎡に縮小) |      |

樋口工業有限会社 新社屋新築工事(木造平屋・事務所)

図面名: 断面図・仕様概要A-04

縮尺 1/60・2026-08-20・計画案v11(B案=111.8㎡に縮小)

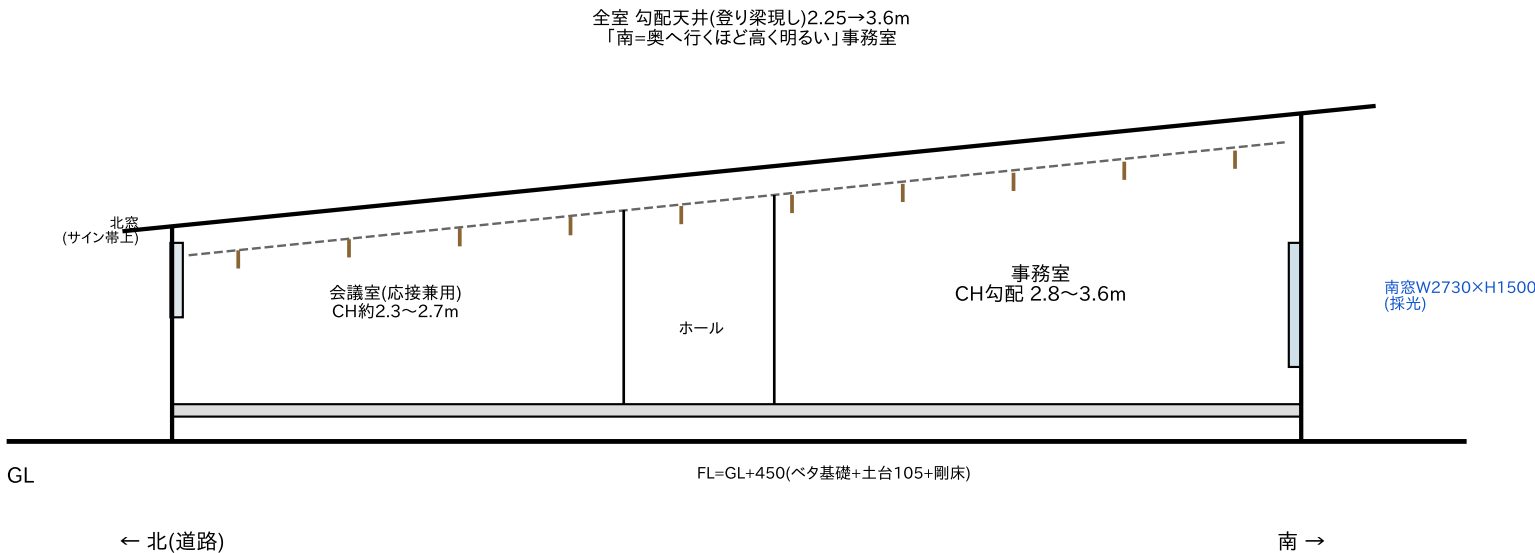

A-A断面図(南北・x=2.3 会議室～ホール～事務室) 1/60

【構造・仕上概要(v10)】

構造: 木造在来・平屋(8.19×13.65m) / 基礎: ベタ基礎 / 壁量: 2025年改正基準(要壁量計算。部門間の間仕切壁を耐力壁に活用=分室化は耐震にも有利)

屋根: SGLガルバ立平つや消し黒・南上がり1/10(北軒GL+2.6→南壁GL+3.97) / 外壁: ガルバ角波つや消し黒+玄関まわりのみ八女杉

サッシ: アルミ樹脂複合 黒 / 断熱: 屋根HGW16K155×2・壁HGW16K105・基礎XPS50 / 天窓なし

内装: 事務・工務=登り梁現し+タイルカーペット / 会議室=杉板1面壁 / ホール=モルタル金鏝+受付CT / 書庫=可動棚・無窓・施錠

外構(自社施工=原価): 舗装+白線・来客P2台・社名サイン・電球色2700K / 設備: 24h換気3種・エアコン(事務1・工務1・会議1)・LAN Cat6A


水回り集約: WCブロック+給湯を中央の1系統に=配管最短・コスト減 / 南・西窓は外付けブラインドで日射対策

※GYM増築計画は廃止 ※屋根北流れ=太陽光不向き ※建設地(441-5)は農地転用許可が前提 ※最終確認は設計者(建築士)による

外観イメージ(北西=道路・ヤード側から)

「黒い箱に、八女杉の玄関」

- ・つや消し黒のガルバの箱。玄関まわりだけ八女杉=樋口工業の顔
- ・玄関に庇D1365: 来客Pから2〜3歩、雨に濡れずに入れる
- ・道路側(左)は会議室の型ガラス窓+工務室の高窓+社名サイン帯
- ・屋根は南へ登る片流れ: 事務室の奥ほど天井が高く明るい
- ・白線の駐車場・舗装は自社施工=施工品質がそのまま名刺になる
- ・夜は電球色2700Kでポーチとサインだけ照らす

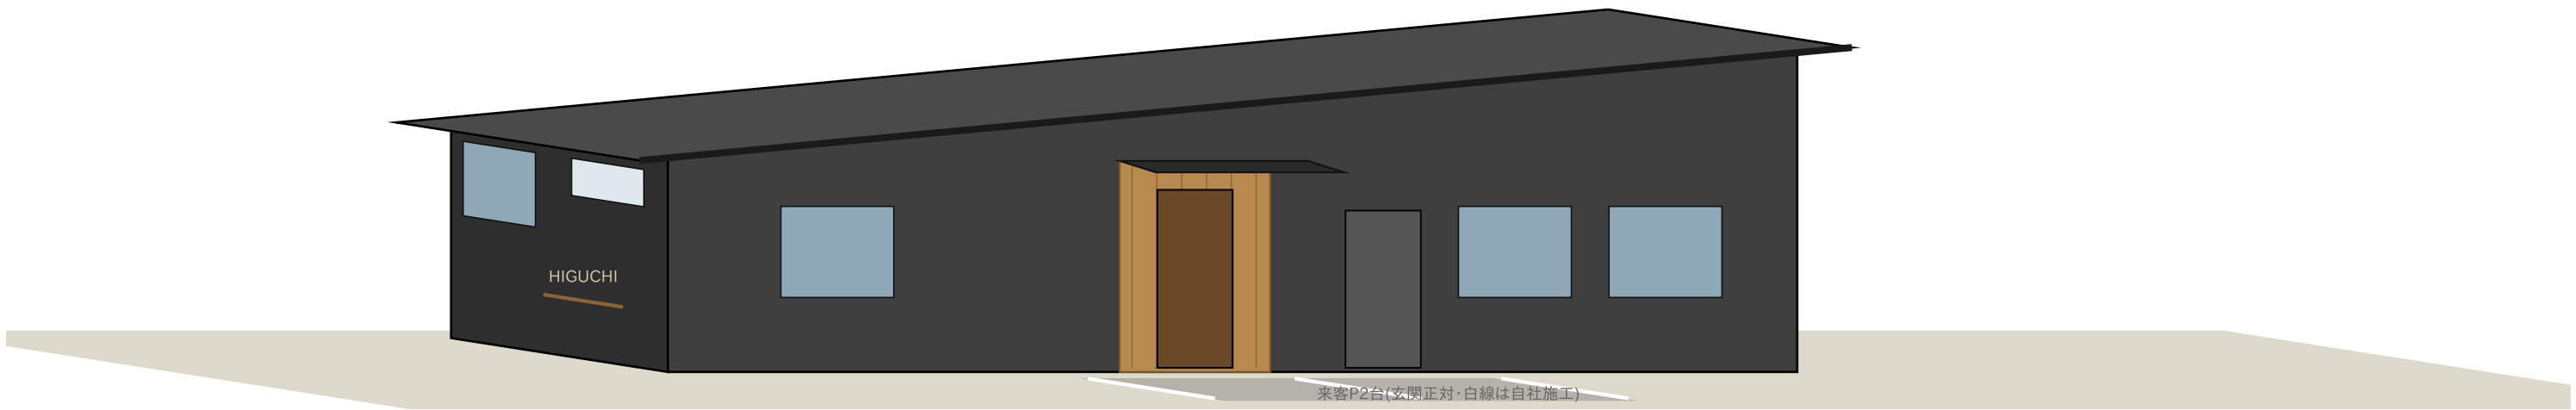

樋口工業有限会社 新社屋新築工事(木造平屋・事務所)

図面名: 外観イメージ

A-05

縮尺 NTS・2026-08-20・計画案v11(B案=111.8㎡に縮小)