




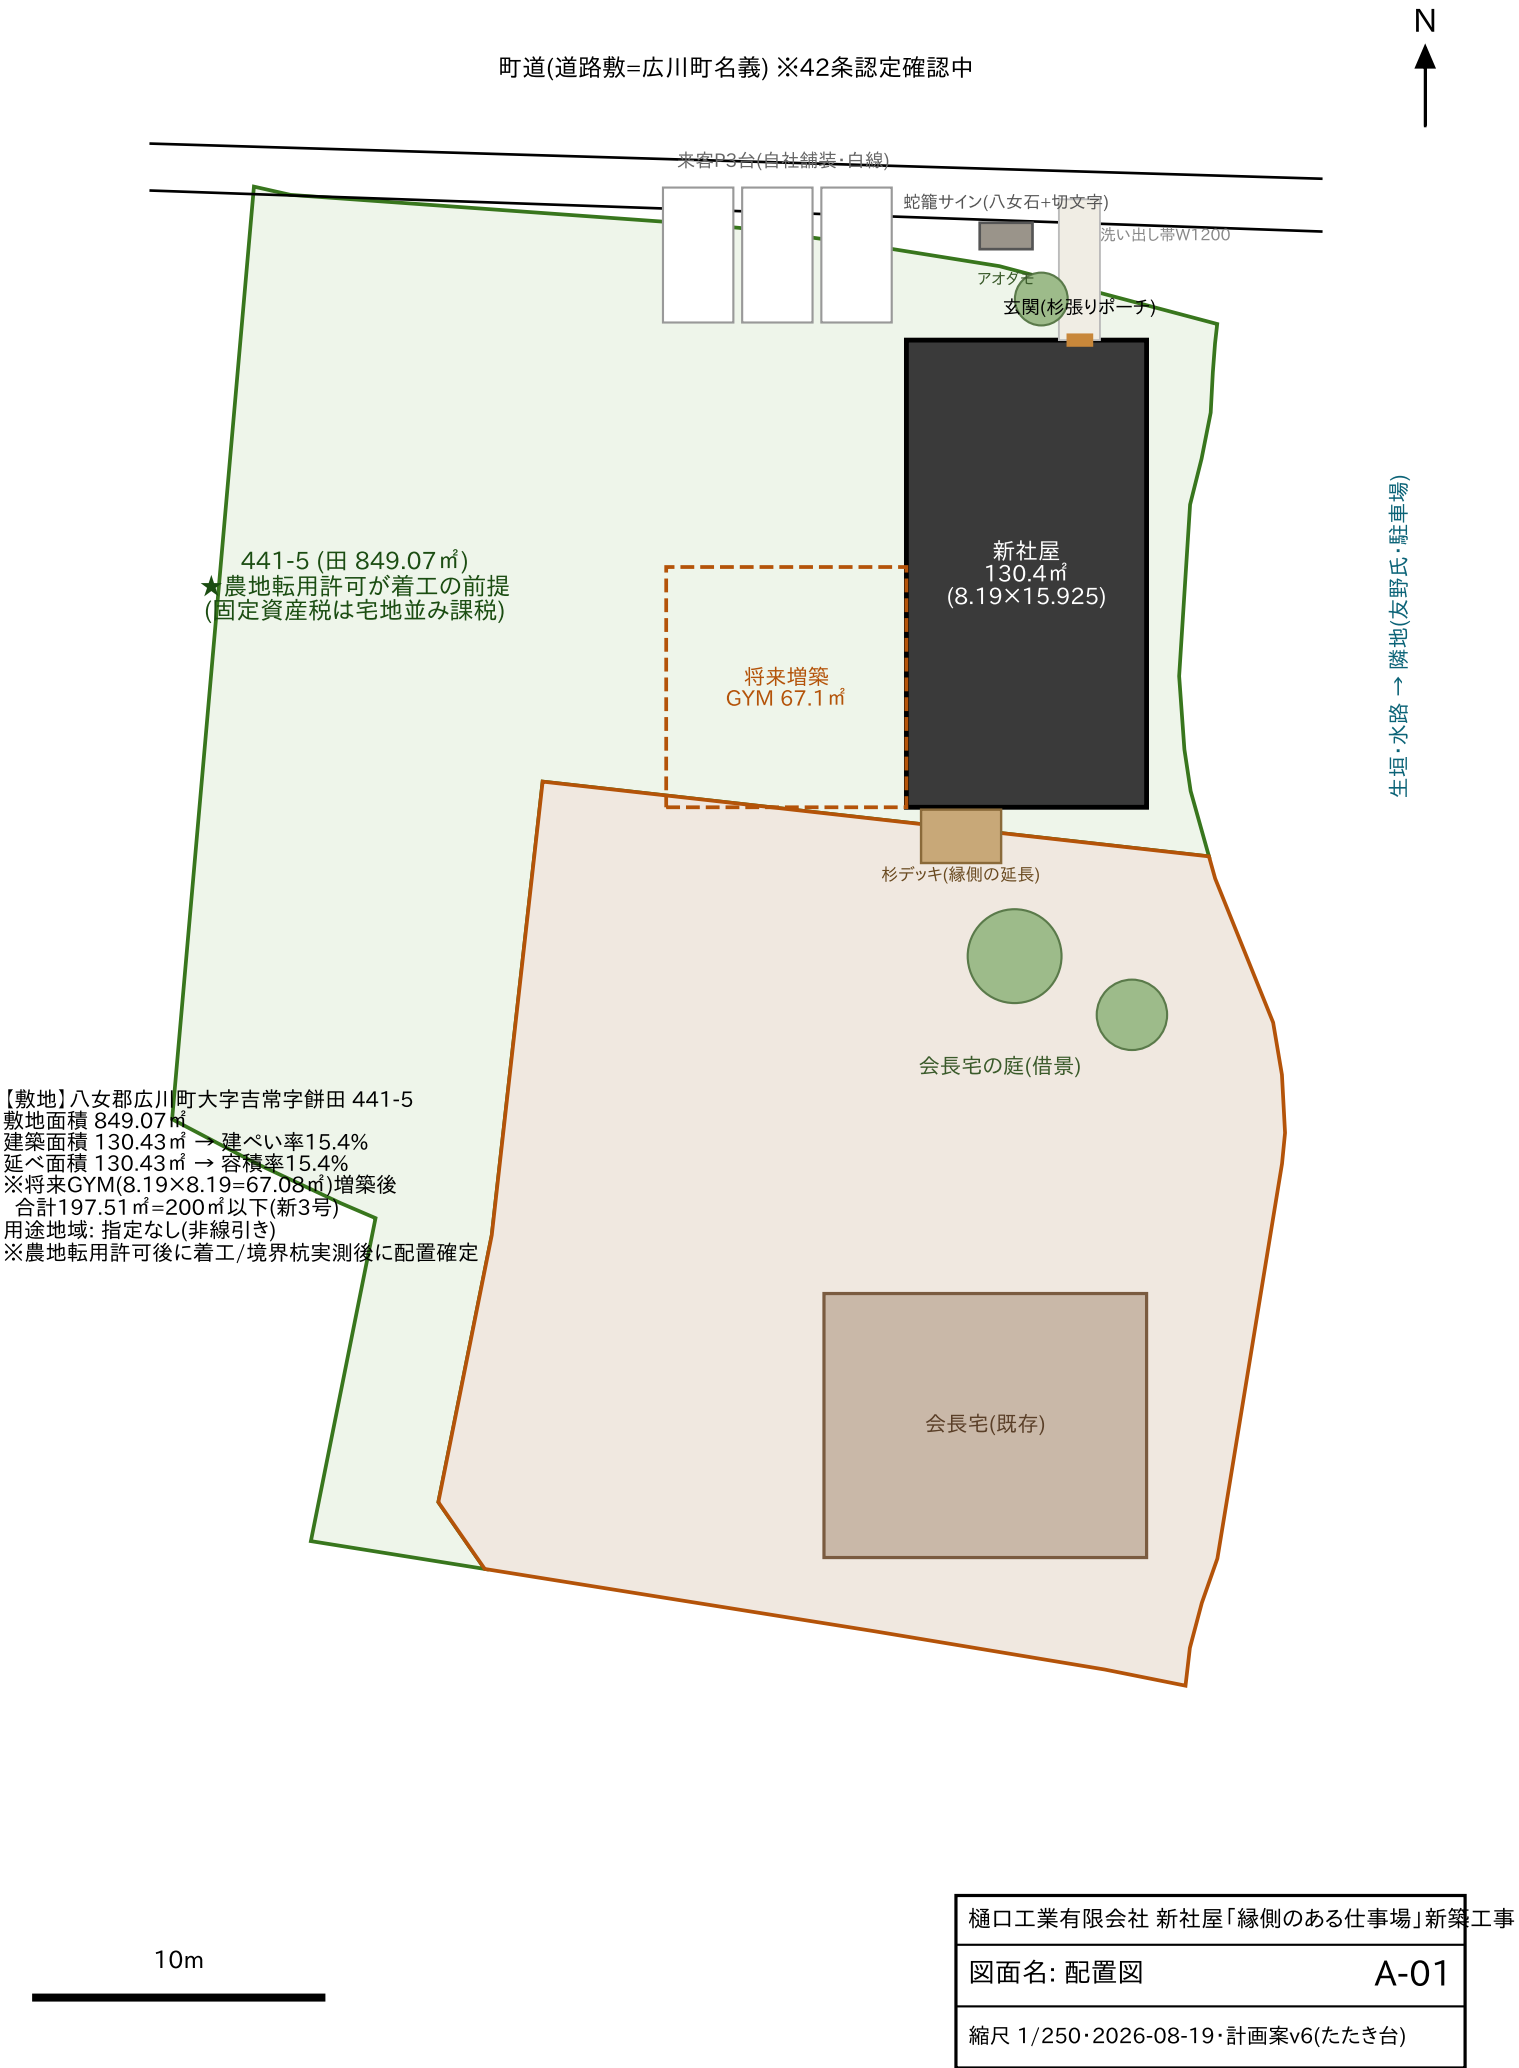


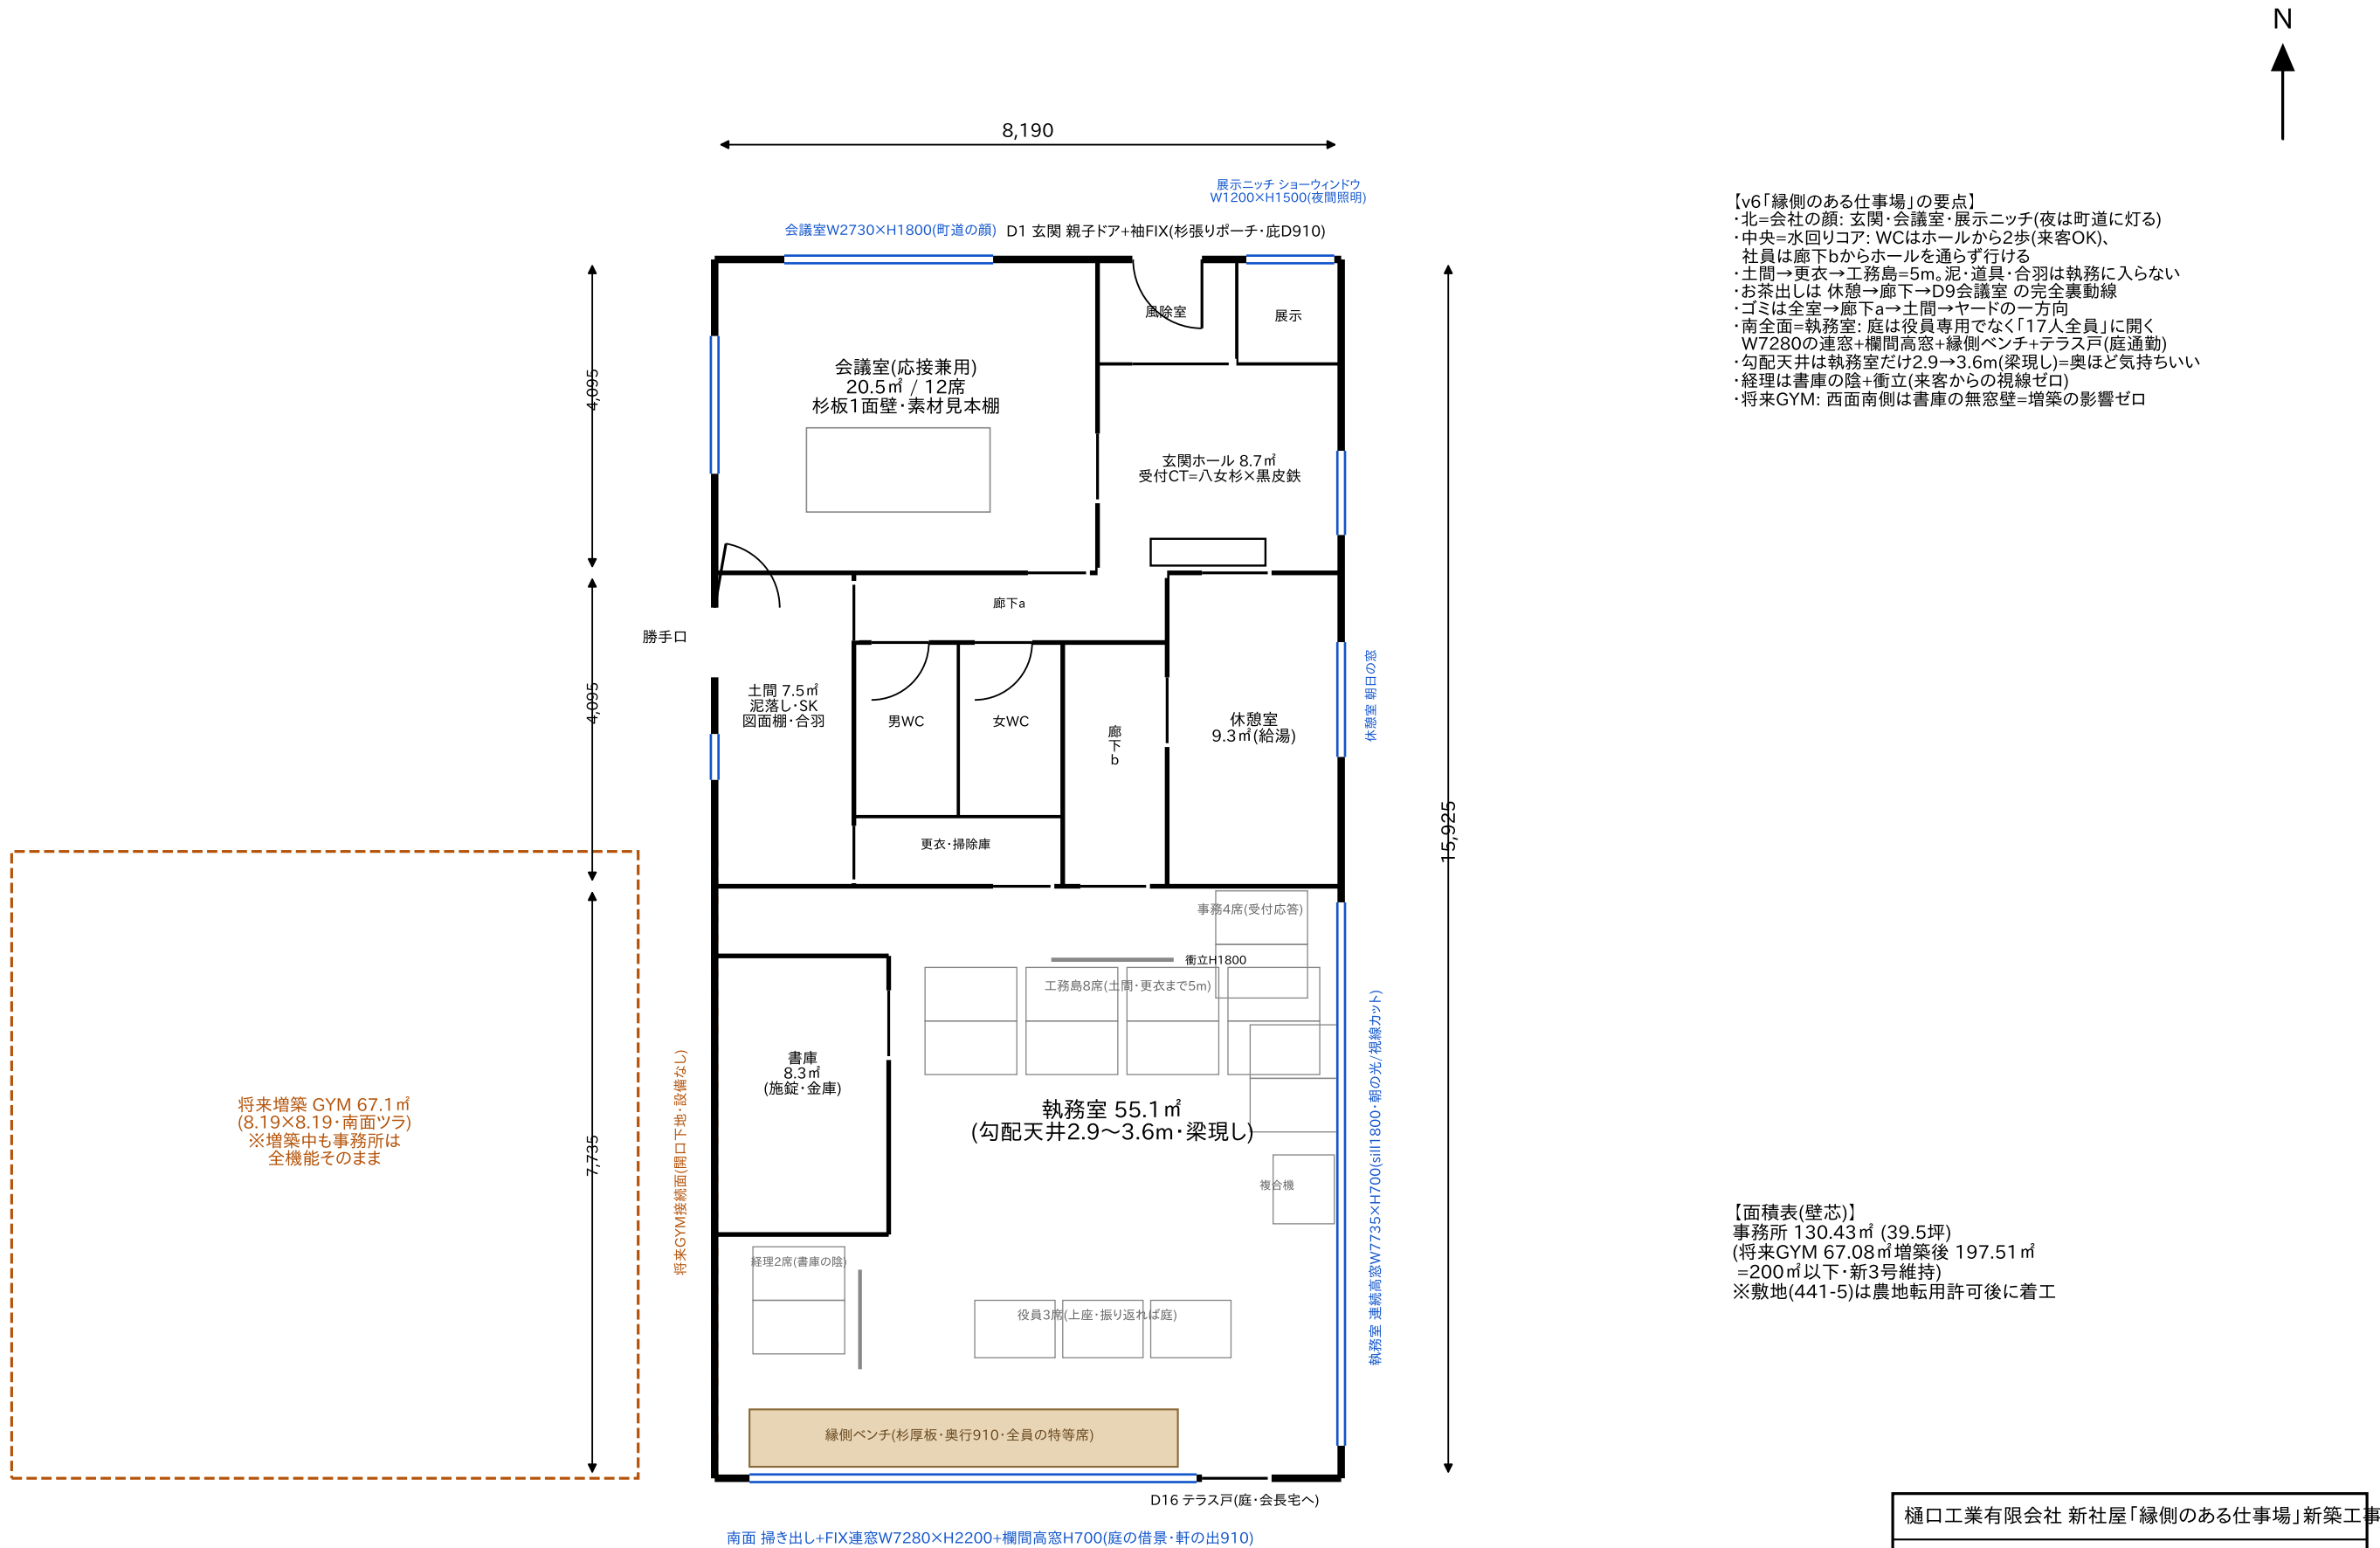


樋口工業有限会社 新社屋「緑側のある仕事場」新築工事	
図面名: 平面図	A-02
縮尺 1/100・2026-08-19・計画案v6(たたき台)	

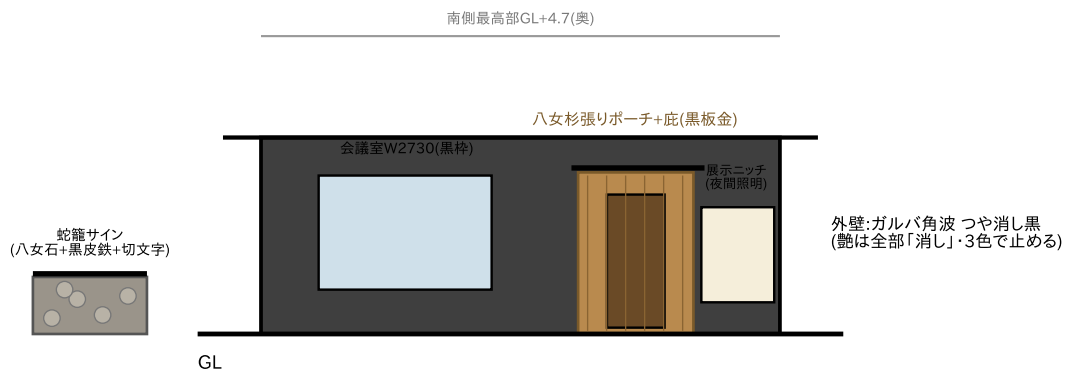


北立面図(道路の顔) 1/150

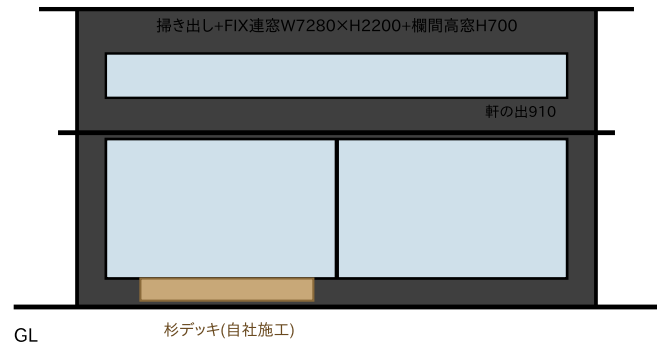

南立面図(庭・借景側) 1/150

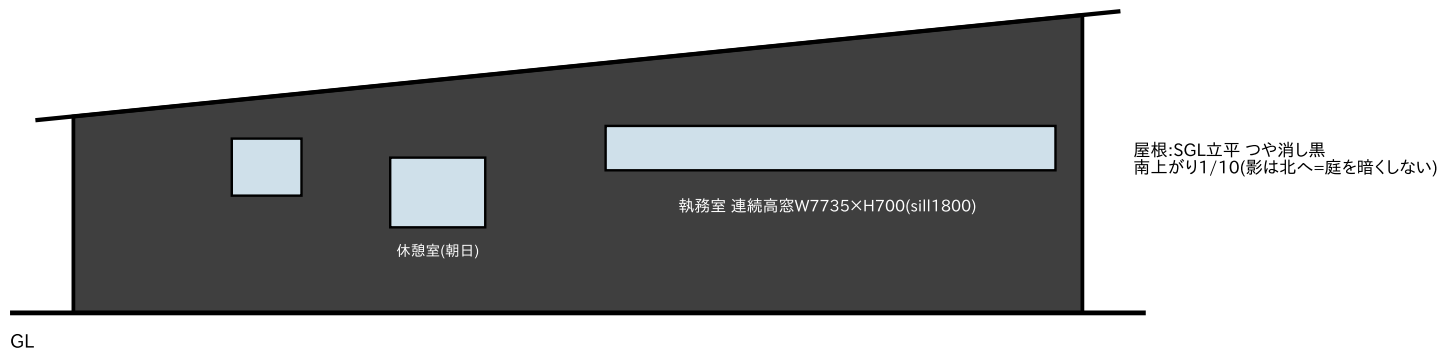


東立面図(生垣・水路側) 1/150

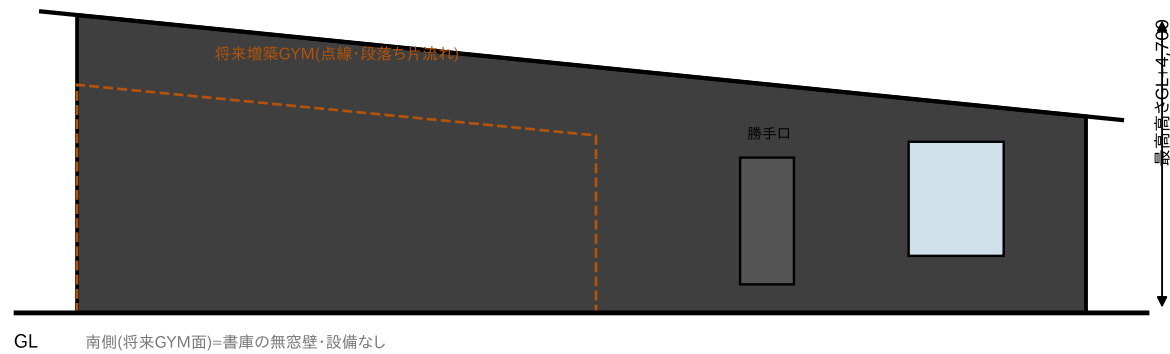

西立面図(ヤード側) 1/150

樋口工業有限会社 新社屋「縁側のある仕事場」新築工事	
図面名: 立面図(4面)	A-03
縮尺 1/150・2026-08-19・計画案v6(たたき台)	

樋口工業有限会社 新社屋「縁側のある仕事場」新築工事	
図面名: 断面図・仕様概要	A-04
縮尺 1/60・2026-08-19・計画案v6(たたき台)	

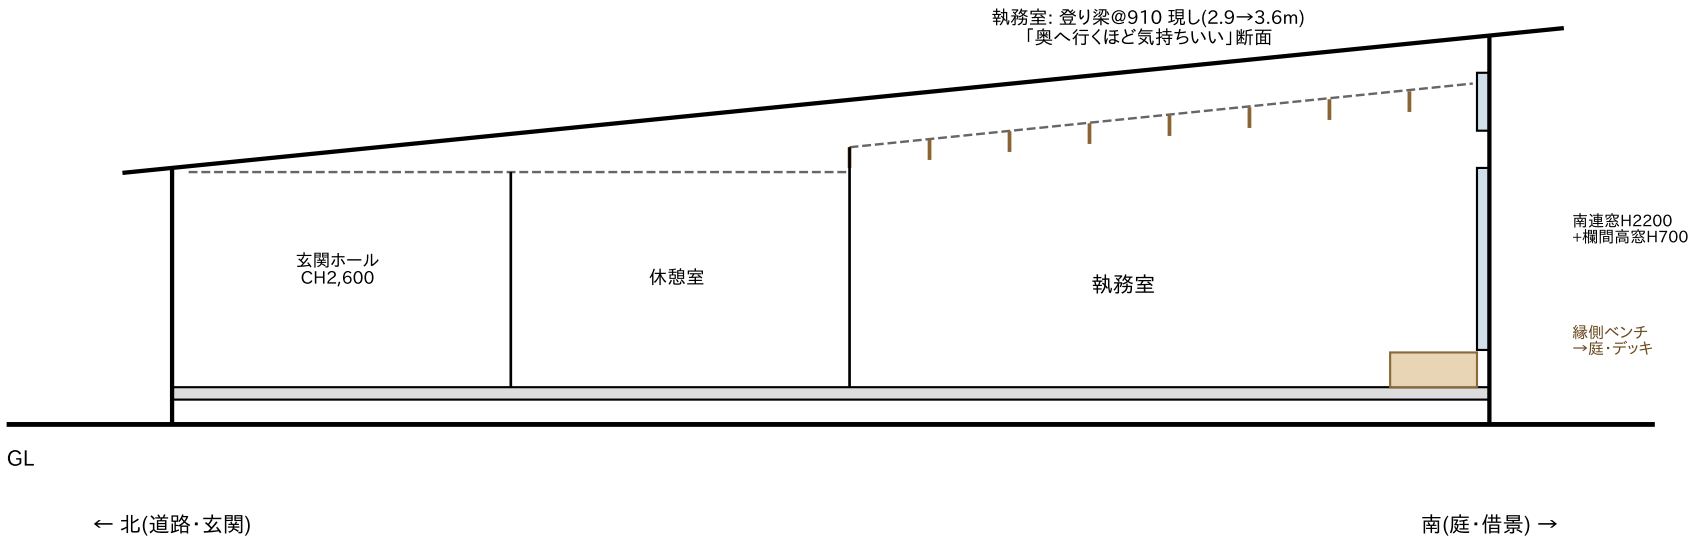


【構造・仕上概要(v6・デザイナー仕様)】
構造: 木造在来・平屋(8.19×15.925m) / 基礎: ベタ基礎 / 壁量: 2025年改正基準・南面連窓の耐力は書庫壁・間仕切で補完(要壁量計算)
屋根: SGLガルバ立平333 つや消し黒・南上がり1/10 / 外壁: ガルバ角波 つや消し黒+玄関ポーチのみ八女杉縦張り(キシラデコール)
サッシ: アルミ樹脂複合 黒・W1650×H1100に規格統一で反復 / 断熱: 屋根HGW16K155×2・壁HGW16K105・基礎XPS50
内装: 執務=構造現し+腰壁構造用合板クリア+タイルカーペット貼分け / 会議=杉板1面壁+ライン照明3000K / ホール=モルタル金鏝+八女杉受付CT(自社鉄工脚)
外構(自社施工=原価): アスファルト舗装+白線・洗い出し帯W1200・蛇籠サイン・アオダモ1本・杉デッキ・電球色2700K照明
設備: 24h換気(3種) / エアコン執務2・会議1 / LAN Cat6A / 将来GYM分の幹線・スリープ先行 / 西面南側(増築面)は無開口・無設備
※太陽光は屋根が北流れのため不向き→載せるならGYM増築屋根で再検討 ※建設地(441-5)は農地転用許可が前提 ※最終確認は設計者(建築士)による

外観イメージ(北東より・アクソメ)

「黒い箱に、八女杉の切り欠き」

- ・ガルバつや消し黒×八女杉×グレー土間の3色
- ・道路には低く水平な軒(GL+3.1)=誠実な顔
- ・南へ屋根が伸び上がる(GL+4.7)=会社の勢い
- ・玄関ポーチだけ杉張り: 触れる距離に木の質感
- ・展示ニッチが夜の町道に灯る(模型・表彰盾)
- ・蛇籠サイン=河川工事の材料で「うちは土木屋」
- ・白線ピシッの駐車場・洗い出しの白い帯=自社施工の名刺
- ・夜は電球色2700K: ポーチ・蛇籠・アオダモだけ照らす

会長宅の庭(借景・南側)

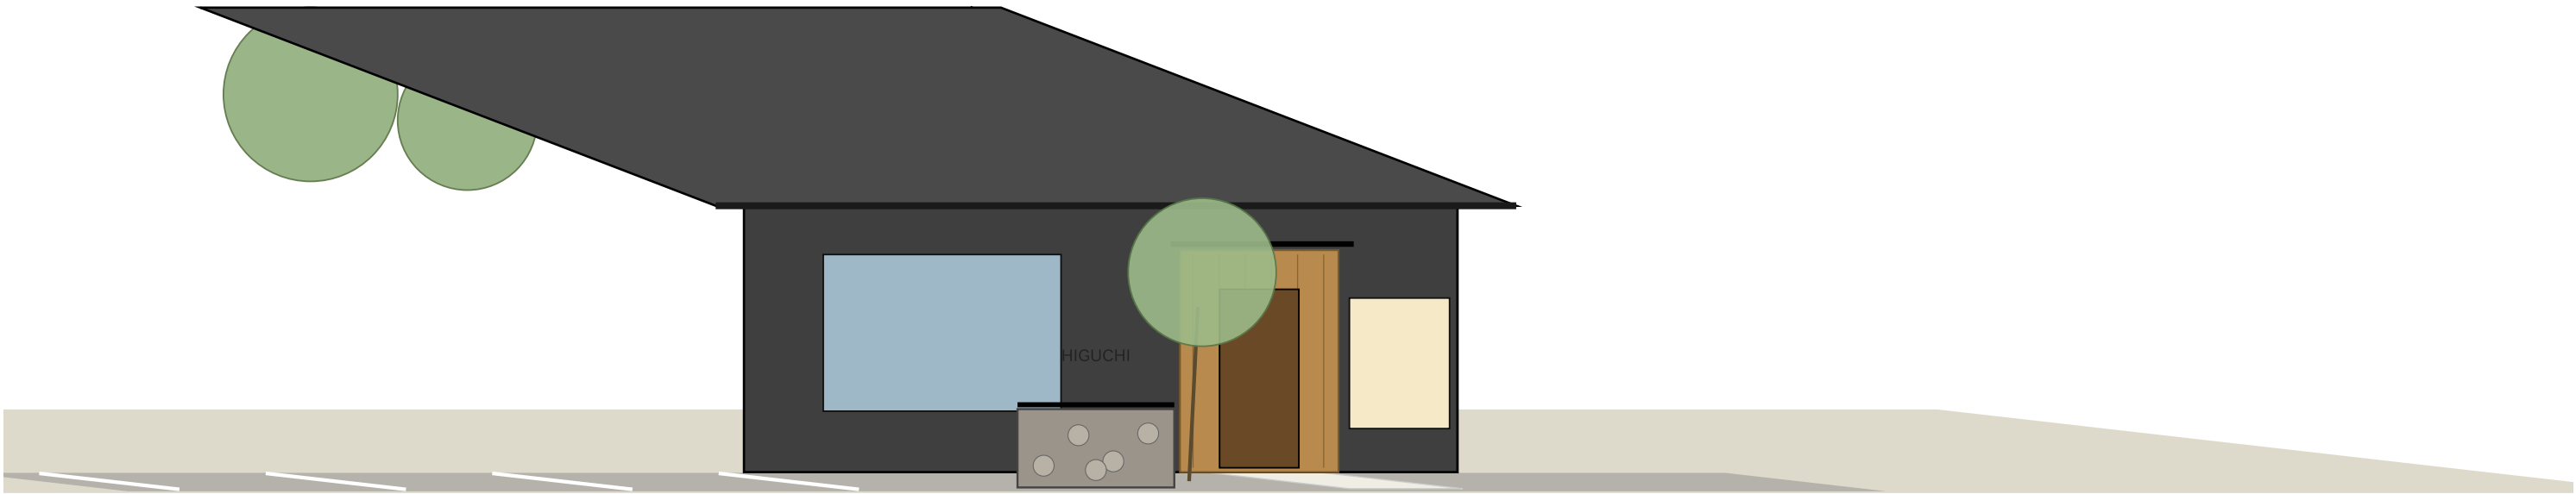

樋口工業有限会社 新社屋「縁側のある仕事場」新築工事

図面名: 外観イメージ

A-05

縮尺 NTS・2026-08-19・計画案v6(たたき台)