


町道(道路敷=広川町名義) ※42条認定確認中 ― 北面は道路際・出入口なし(窓+サイン帯)

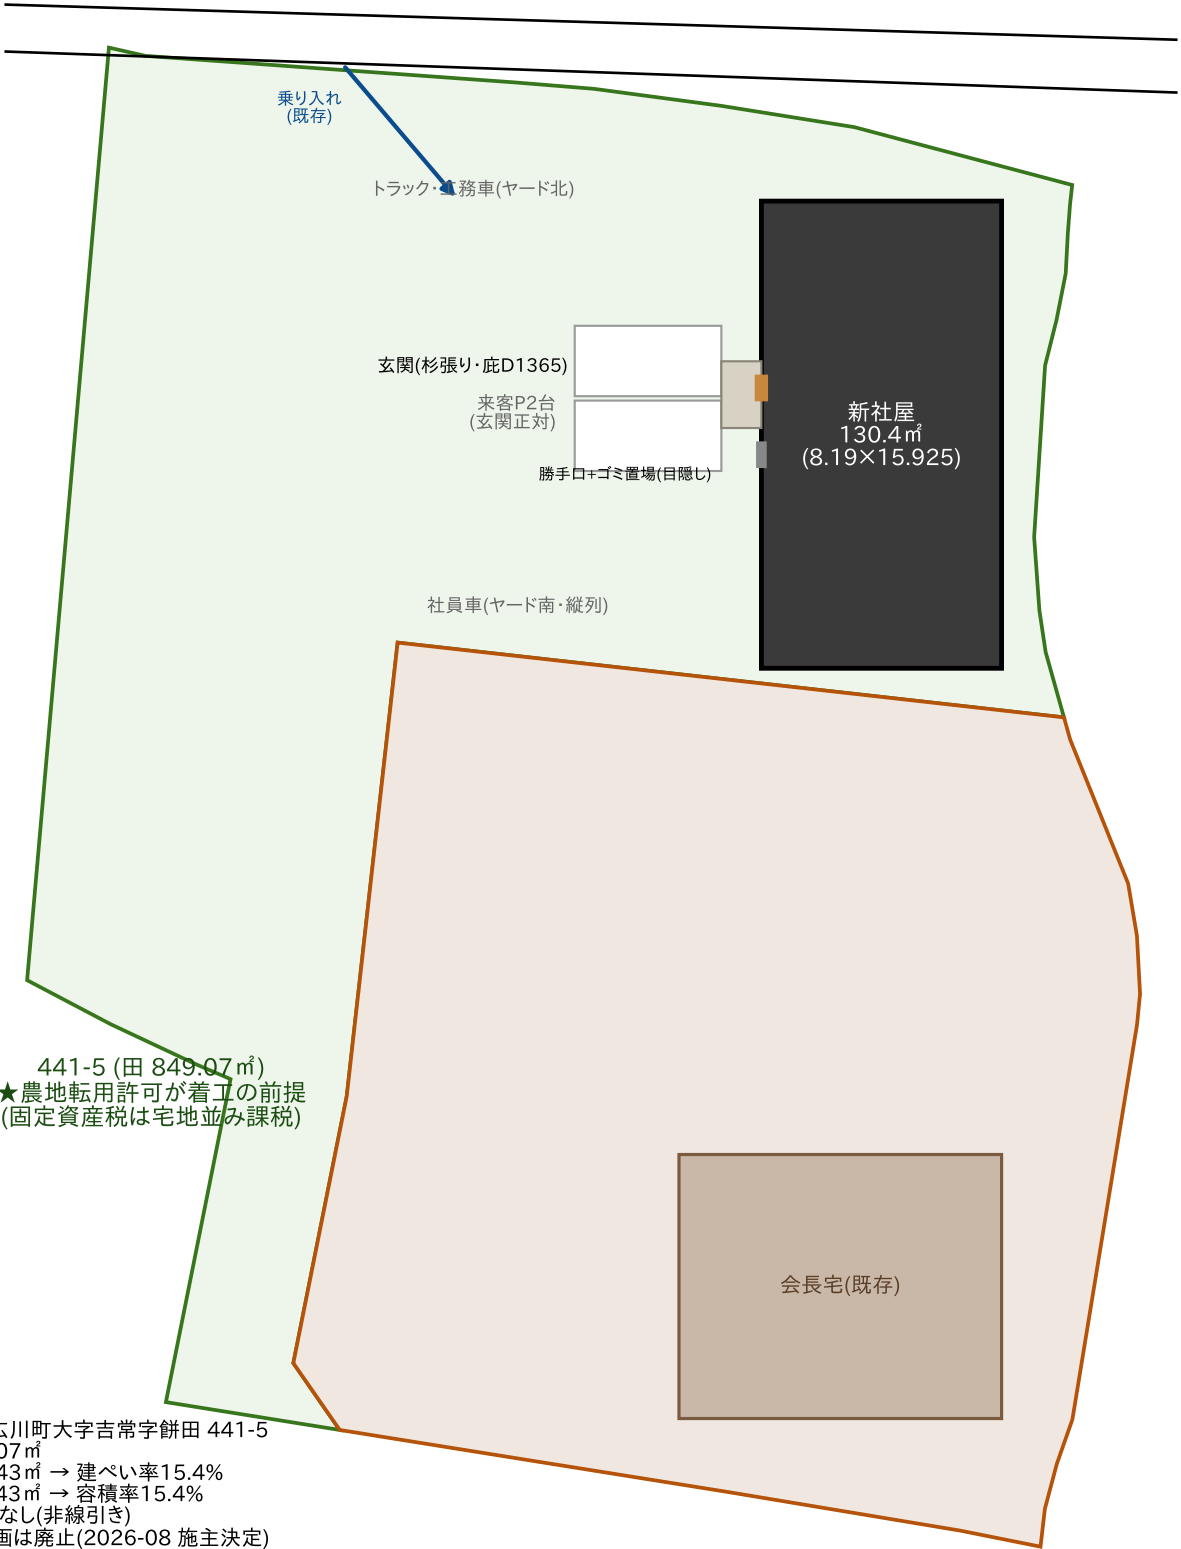


生垣・水路 → 隣地 (友野氏・駐車場)

441-5 (田 849.07㎡)
★農地転用許可が着工の前提
(固定資産税は宅地並み課税)

【敷地】八女郡広川町大字吉常字餅田 441-5
敷地面積 849.07㎡
建築面積 130.43㎡ → 建ぺい率15.4%
延べ面積 130.43㎡ → 容積率15.4%
用途地域: 指定なし(非線引き)
※GYM増築計画は廃止(2026-08 施主決定)
※農地転用許可後に着工/境界杭実測後に配置確定

10m

樋口工業有限会社 新社屋新築工事(木造平屋・事務所)	
図面名: 配置図	A-01
縮尺 1/250・2026-08-20・計画案v9(事務所最適化)	

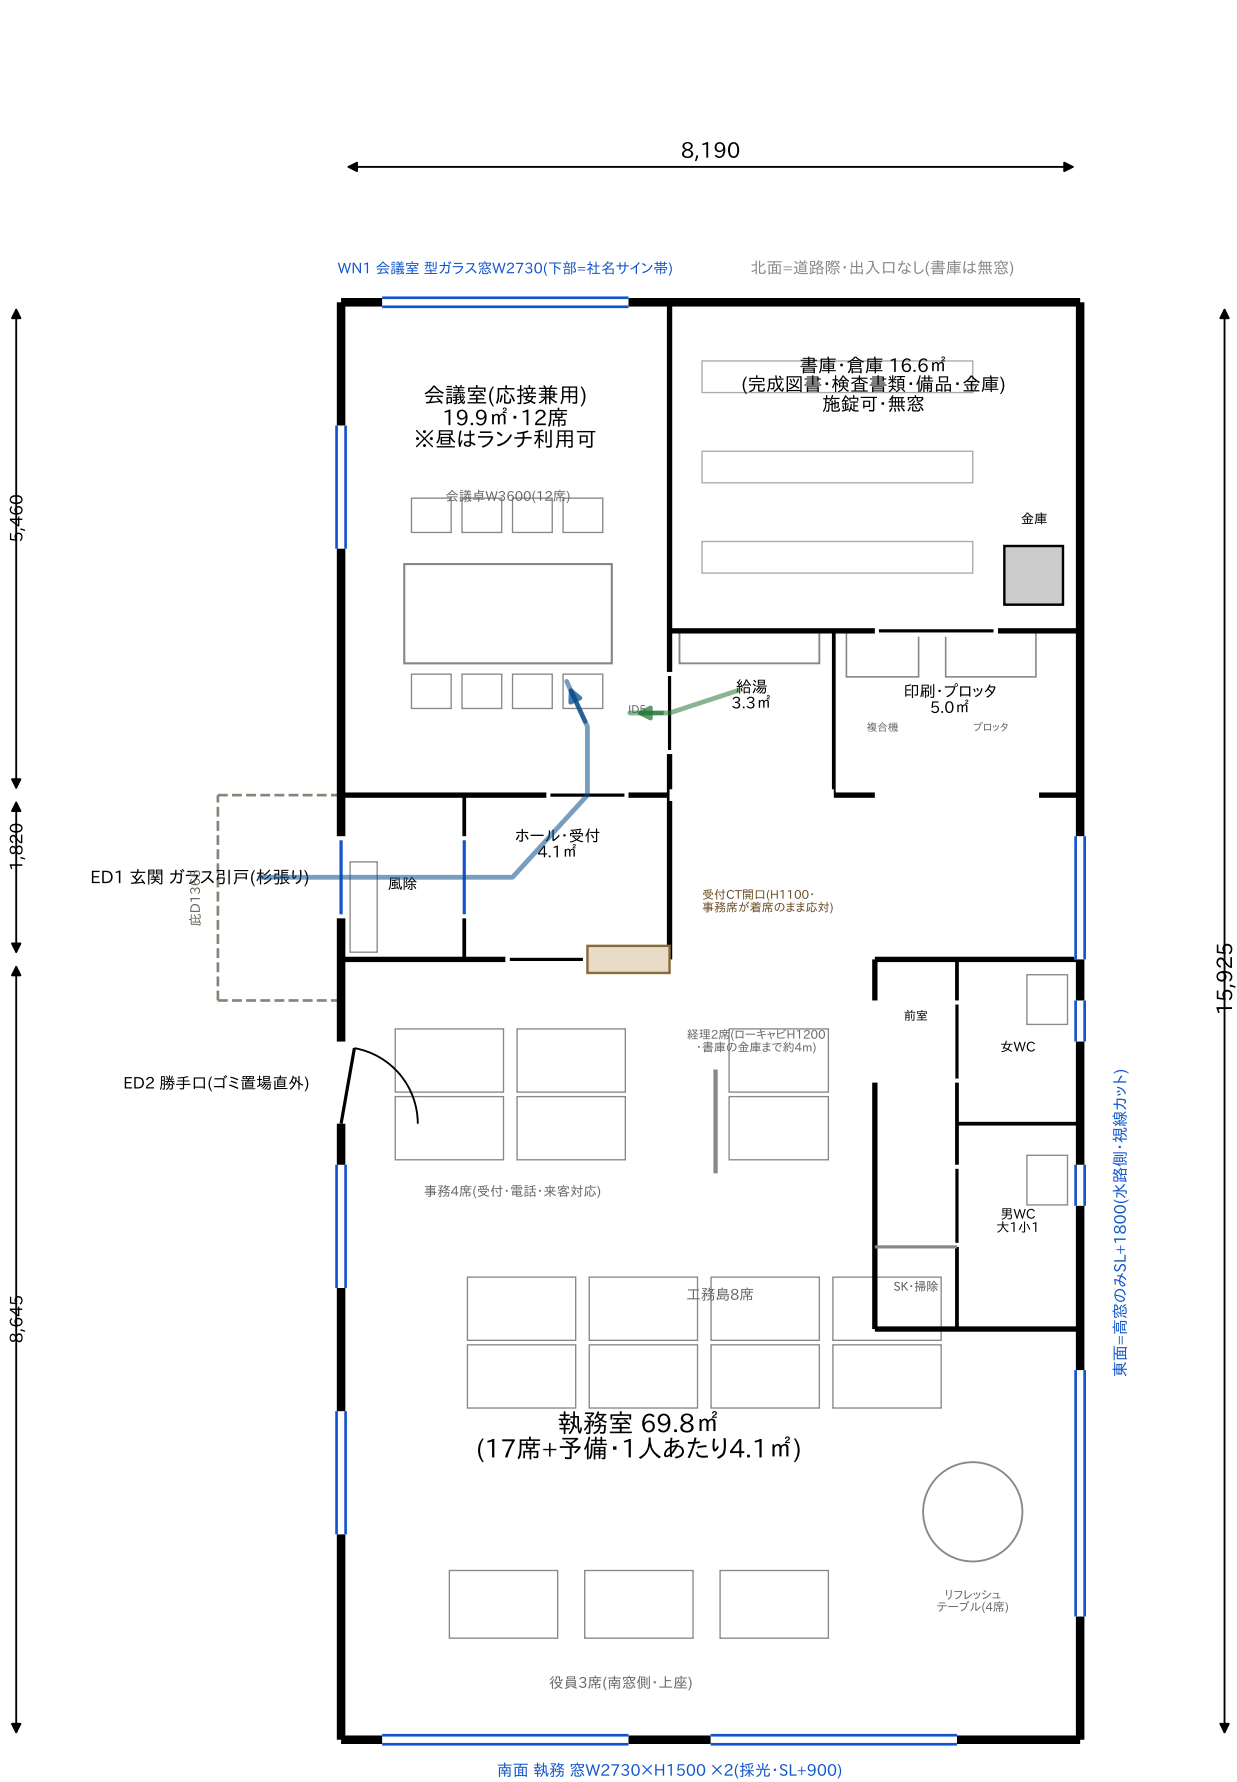


【v9 事務所として最適化(施主レビュー反映)】
・朝礼土間/日報CT/更衣シャワー/休憩室・食堂/南の庭園要素 → すべて廃止
・普通の事務所として9室+執務: 執務69.8㎡(17席・1人4.1㎡のゆとり)
+会議室(応接兼用)19.9㎡+書庫16.6㎡+給湯・印刷+WC
・来客: 玄関(西)→ホール→会議室で完結。執務室に入らない
・受付: 事務4席が玄関のすぐ内側。カウンター開口越しに着席のまま応対
・お茶出し: 給湯⇄会議室の直結戸ID5(扉1枚・2歩)
・経理: 施錠書庫内の金庫まで約4m。ローキャビH1200で手元を遮蔽
・書庫16.6㎡: 建設業の完成図書・検査書類の長期保管対応。無窓・施錠可
・工務: プロッタ(図面出力)→書庫が直結。島8席
・昼: 会議室兼用+リフレッシュテーブル4席。休憩室は設けない(施主決定)
・水回りはWCブロック+給湯の1系統に集約=配管最短・建設費減

- 来客動線: 玄関→ホール→会議室(執務室に入らない・扉2枚)
- お茶出し: 給湯⇄会議室の直結戸ID5=扉1枚・2歩

【面積表(壁芯)130.43㎡=39.5坪】
会議室(応接兼用)19.87/風除2.48/ホール・受付4.14
書庫・倉庫16.56/給湯3.31/印刷・プロッタ4.97
WC前室(SK)3.73/女WC2.48/男WC3.11/執務室69.77
※FL=GL+450(風除のみ土間)/執務は南2+西2+東高窓の採光
※敷地(441-5)は農地転用許可後に着工


樋口工業有限会社 新社屋新築工事(木造平屋・事務所)	
図面名: 平面図	A-02
縮尺 1/100・2026-08-20・計画案v9(事務所最適化)	

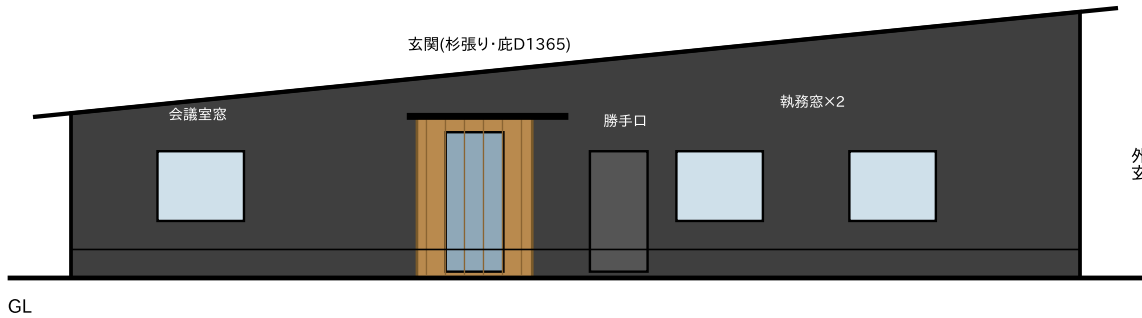


西立面図(ヤード・駐車場側=入口の顔) 1/150



北立面図(道路の顔・出入口なし) 1/150

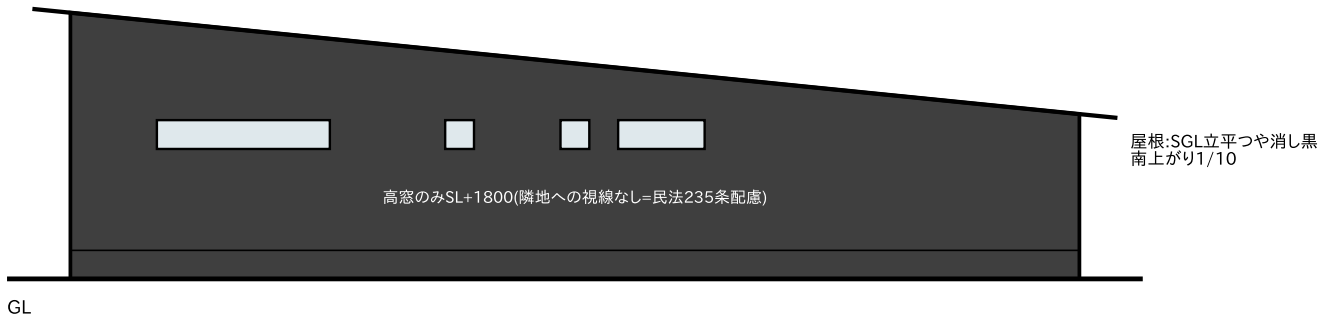


東立面図(生垣・水路側) 1/150

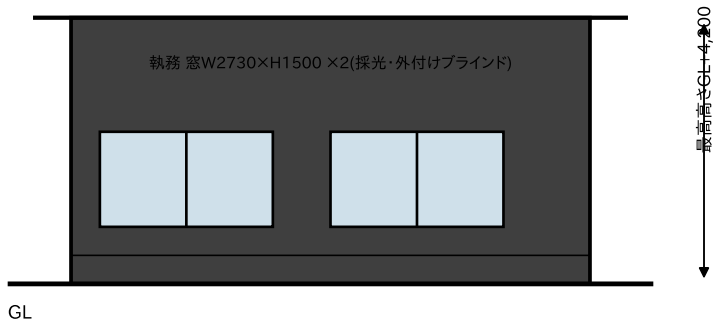

南立面図(採光面) 1/150

樋口工業有限公司 新社屋新築工事(木造平屋・事務所)	
図面名: 立面図(4面)	A-03
縮尺 1/150・2026-08-20・計画案v9(事務所最適化)	

樋口工業有限会社 新社屋新築工事(木造平屋・事務所)	
図面名: 断面図・仕様概要	A-04
縮尺 1/60・2026-08-20・計画案v9(事務所最適化)	

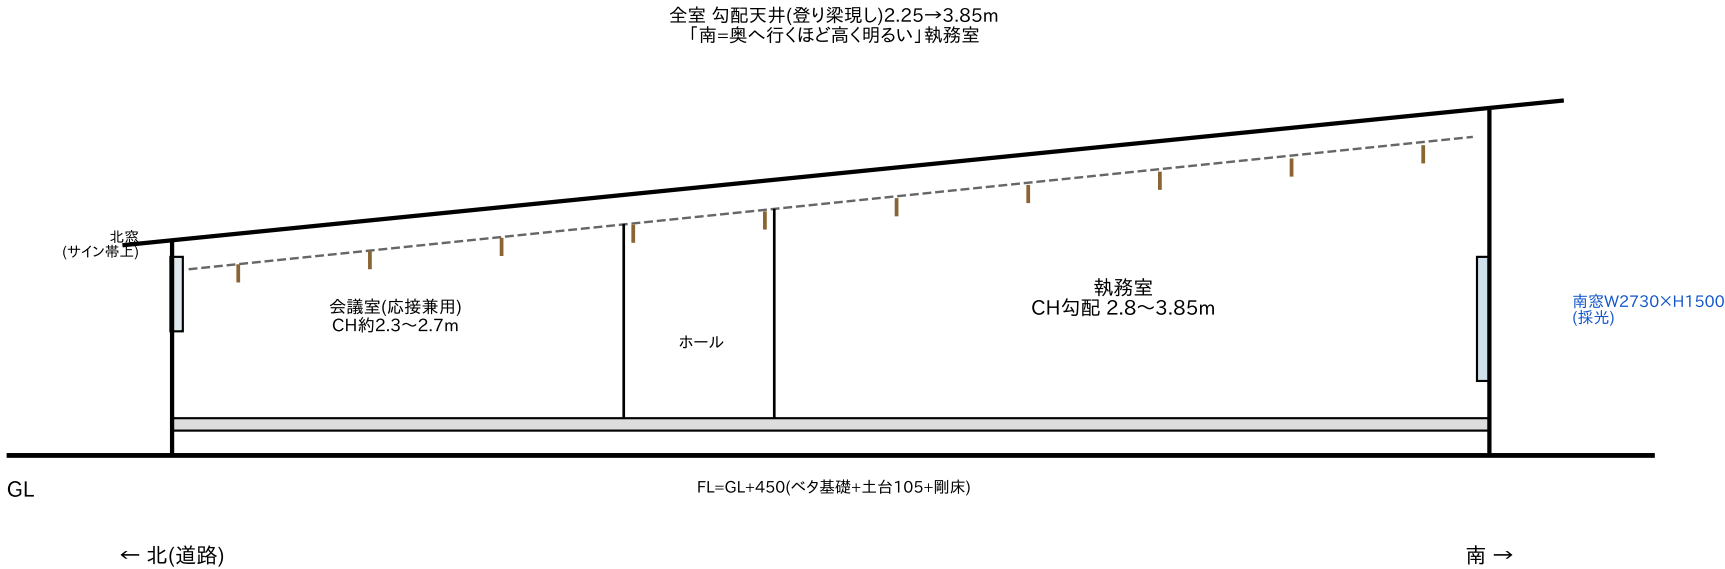


A-A断面図(南北・x=2.7 会議室～ホール～執務室) 1/60

【構造・仕上概要(v9)】
構造: 木造在来・平屋(8.19×15.925m) / 基礎: ベタ基礎 / 壁量: 2025年改正基準(要壁量計算・南2面開口は書庫・WC回りの耐力壁で補完)
屋根: SGLガルバ立平つや消し黒・南上がり1/10(北軒GL+2.6→南壁GL+4.2) / 外壁: ガルバ角波つや消し黒+玄関まわりのみ八女杉
サッシ: アルミ樹脂複合 黒 / 断熱: 屋根HGW16K155×2・壁HGW16K105・基礎XPS50 / 天窓なし(南・西・東の窓で採光)
内装: 執務=登り梁現し+タイルカーペット / 会議室=杉板1面壁 / ホール=モルタル金鏝+受付CT / 書庫=可動棚・無窓・施錠
外構(自社施工=原価): 舗装+白線・来客P2台・社名サイン・電球色2700K / 設備: 24h換気3種・エアコン執務2+会議1・LAN Cat6A
水回り集約: WCブロック+給湯を建物中央東側の1系統に=配管最短・コスト減 / 南・西窓は外付けブラインドで日射対策
※GYM増築計画は廃止 ※屋根北流れ=太陽光不向き ※建設地(441-5)は農地転用許可が前提 ※最終確認は設計者(建築士)による

外観イメージ(北西=道路・ヤード側から)

「黒い箱に、八女杉の玄関」

- ・つや消し黒のガルバの箱。玄関まわりだけ八女杉=樋口工業の顔
- ・玄関に庇D1365: 来客Pから2〜3歩、雨に濡れずに入れる
- ・道路側(左)は型ガラス窓+社名サイン帯のみ: 低い軒2.6mの控えめな顔
- ・屋根は南へ登る片流れ: 執務室の奥ほど天井が高く明るい
- ・白線の駐車場・舗装は自社施工=施工品質がそのまま名刺になる
- ・夜は電球色2700Kでポーチとサインだけ照らす

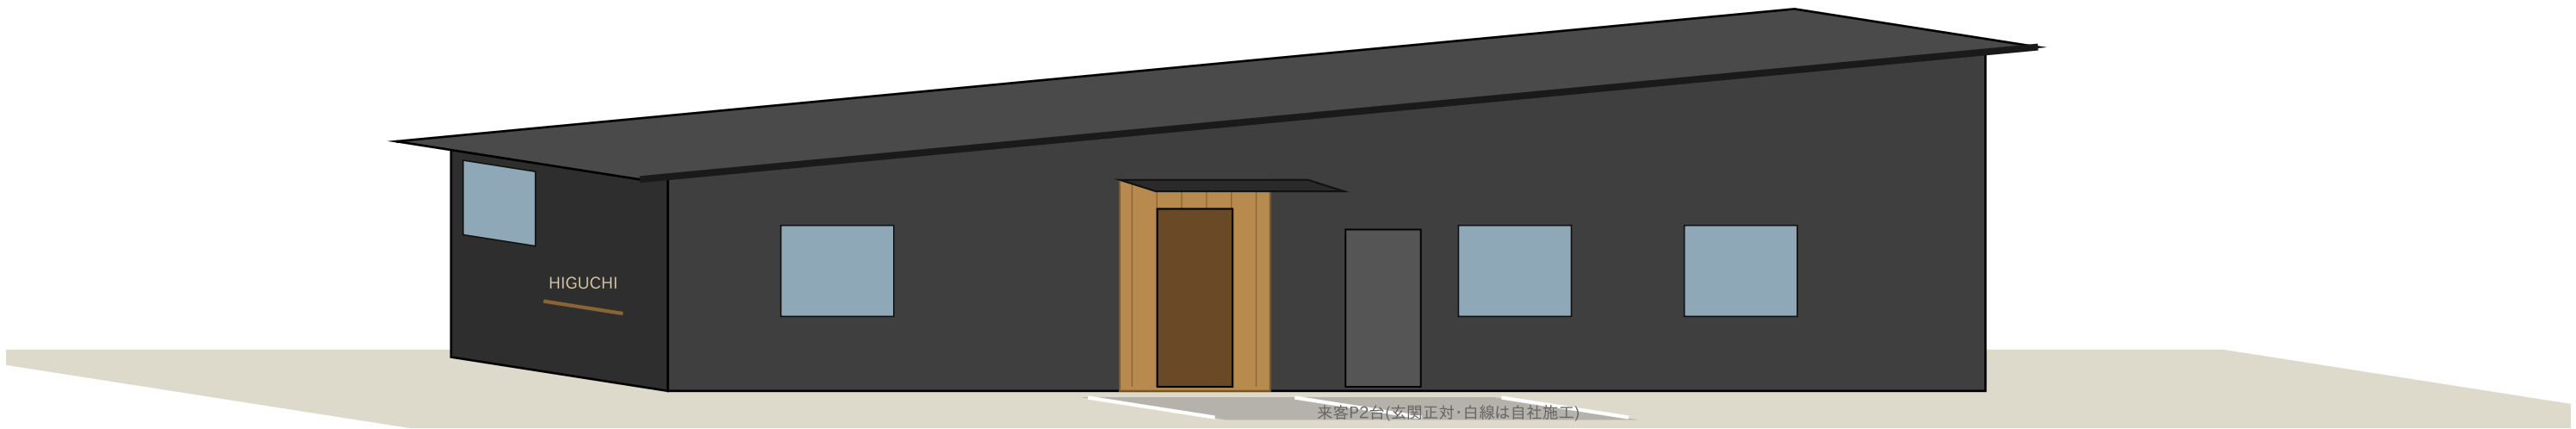

樋口工業有限会社 新社屋新築工事(木造平屋・事務所)

図面名: 外観イメージ

A-05

縮尺 NTS・2026-08-20・計画案v9(事務所最適化)