

町道(道路敷443-2・442-3=広川町名義) ※42条認定確認中



来客P3台・車回し(北庭5.2~7.1m)



441-5 (田 849.07㎡)
★農地転用許可が着工の前提
(固定資産税は宅地並み課税)

将来増築
GYM 70.8㎡

事務所
126.7㎡
(11.83×10.92)

水路まで1.5m

水路 → 隣地(友野氏・駐車場)

【敷地】八女郡広川町大字吉常字餅田 441-5
敷地面積 849.07㎡
建築面積 129.18㎡(ポーチ含む) → 建ぺい率15.2%
延べ面積 126.70㎡ → 容積率14.9%
※将来GYM増築後 延べ197.5㎡=200㎡以下(新3号)
用途地域: 指定なし(非線引き)
※農地転用許可後に着工/境界杭実測後に配置確定

既存住宅
(位置は概略)

441-1 (宅地 708.85㎡)


10m

樋口工業有限会社 新社屋(事務所棟)新築工事

図面名: 配置図

A-01

縮尺 1/250・2026-08-19・計画案v5(たたき台)

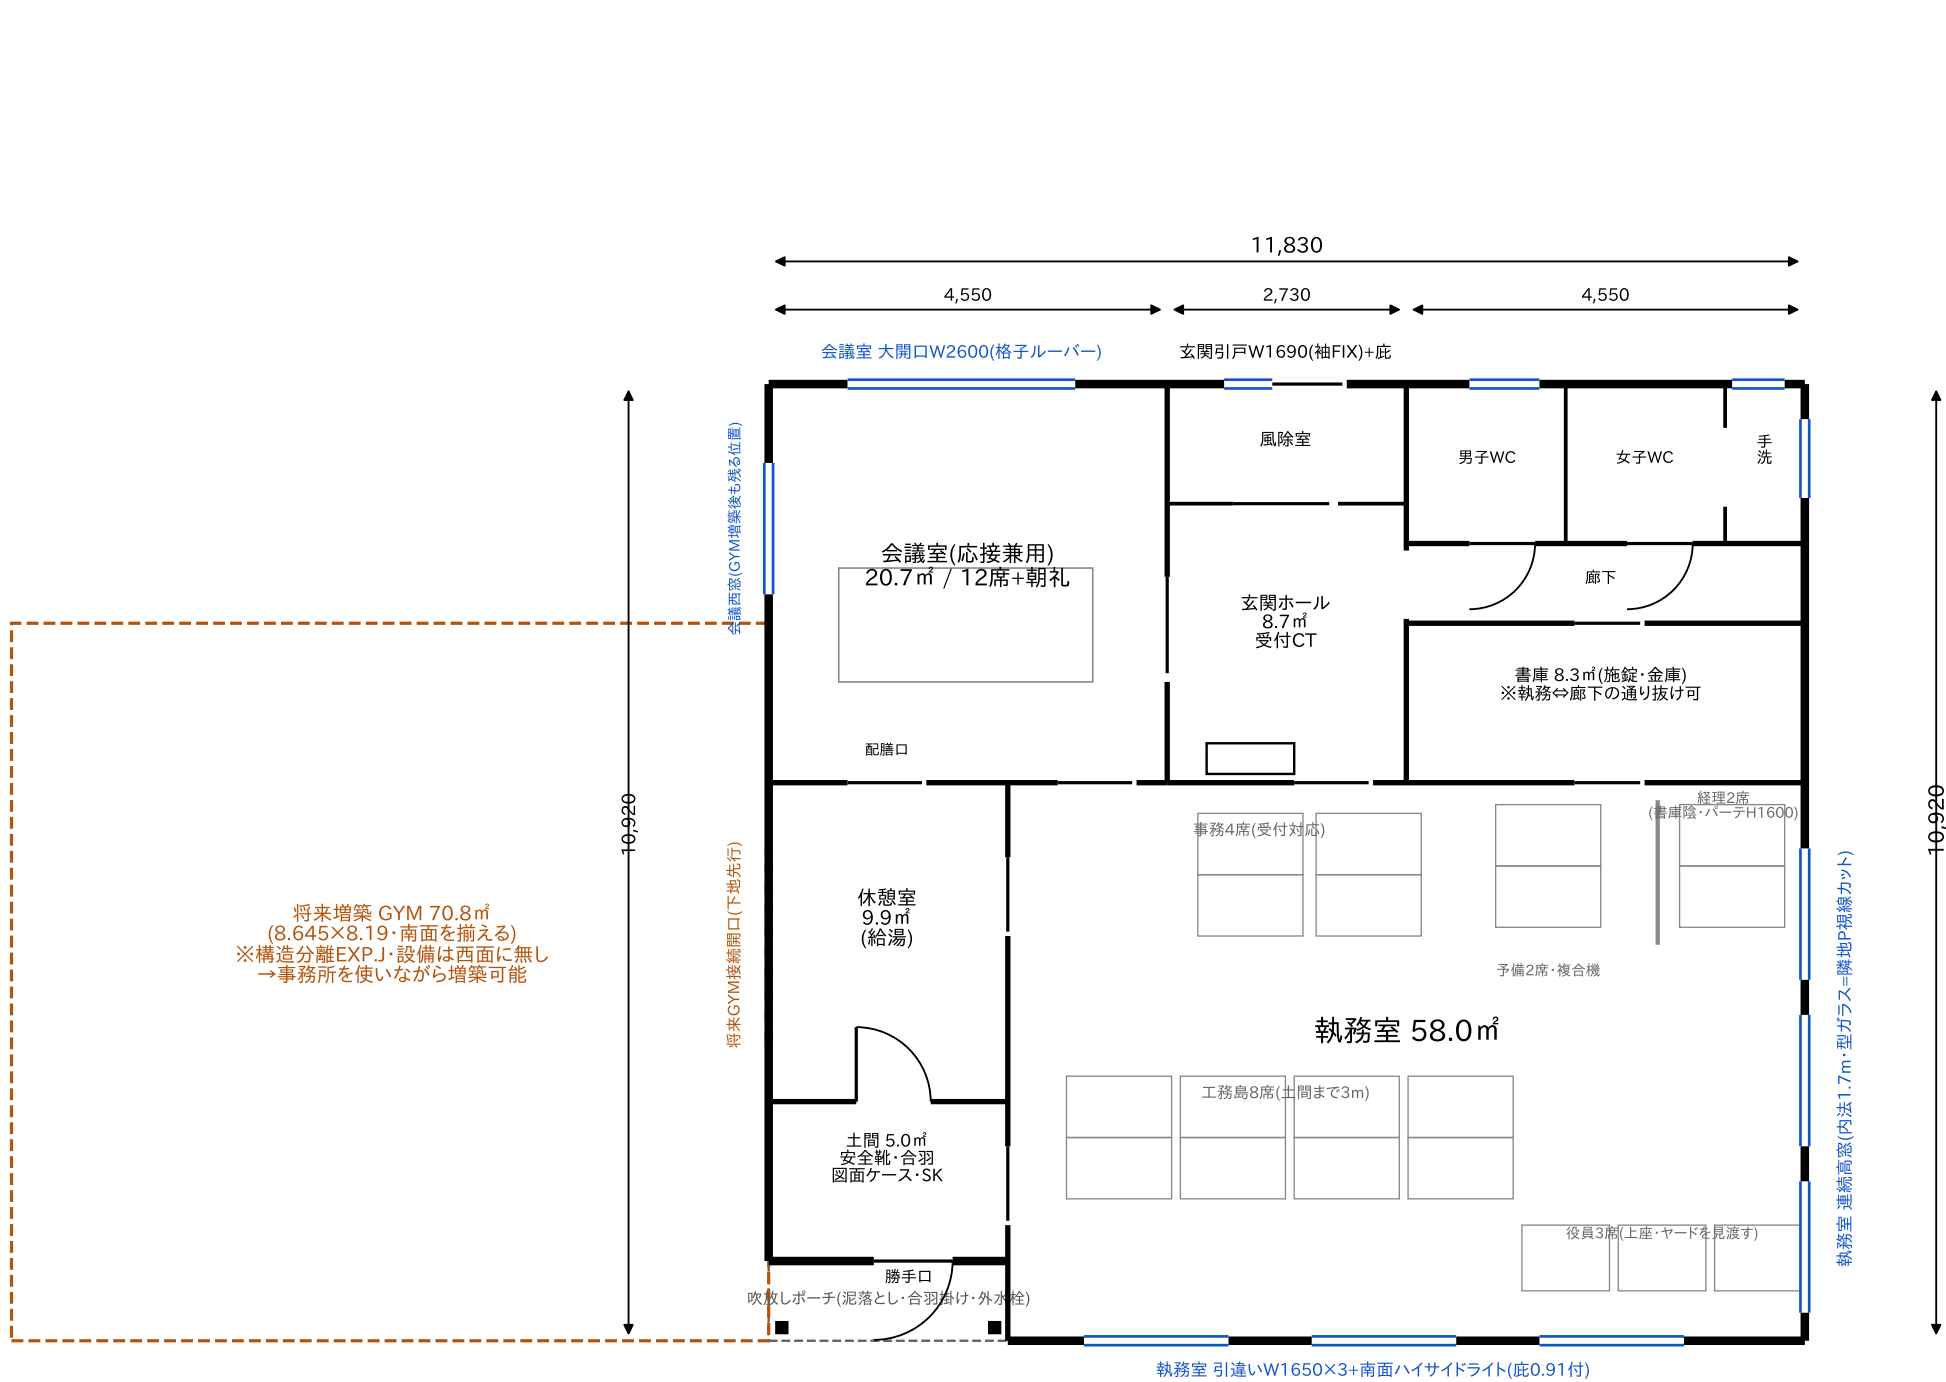

【v5=3案合成の要点】
・ほぼ正方形(11.83×10.92m)=歩行距離・空調・構造すべて効率的
・北帯=接客ゾーン: 玄関・会議・WCが完結し、来客は執務室に入らない
・WCはホール脇: 来客も社員も使える(社員は書庫通り抜けで最短)
・南西=土間: ポーチで泥を落とし→安全靴・合羽・図面→工務島まで3m
・ゴミ出しも各室→土間→ヤードの一方方向(執務を横切らない)
・給湯→会議室は配膳口で直結(お茶出し最短)
・経理は書庫の陰+バーテ、役員は南東の上座からヤードを見渡す
・執務室は南(主開口+ハイサイド)+東(高窓)の2面採光
・将来GYMは西面接続: 執務室が西に面していないので
増築中も増築後も業務・採光が無傷




【面積表(壁芯)】
事務所 126.70㎡ (38.3坪)+吹放しポーチ2.5㎡
(将来GYM増築後 197.5㎡=200㎡以下・新3号維持)
※敷地(441-5)は農地転用許可後に着工

樋口工業有限会社 新社屋(事務所棟)新築工事

図面名: 平面図

A-02

縮尺 1/100・2026-08-19・計画案v5(たたき台)

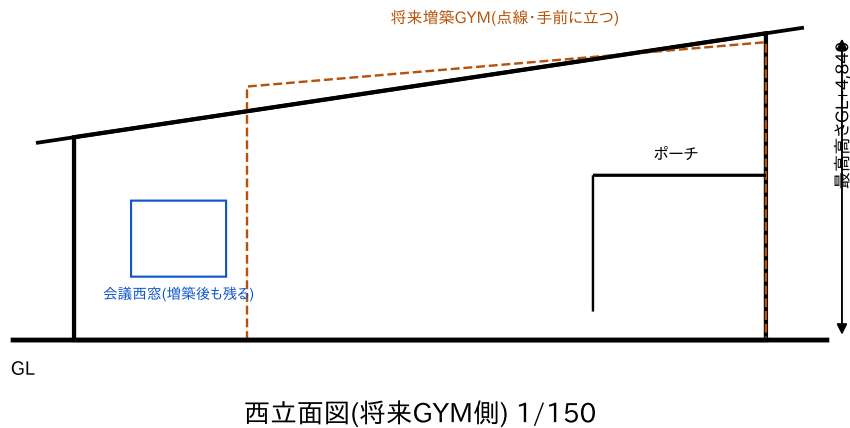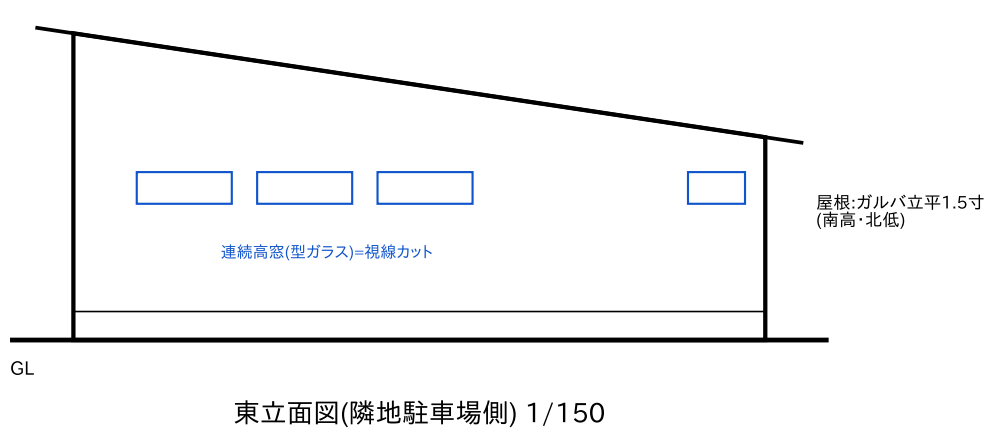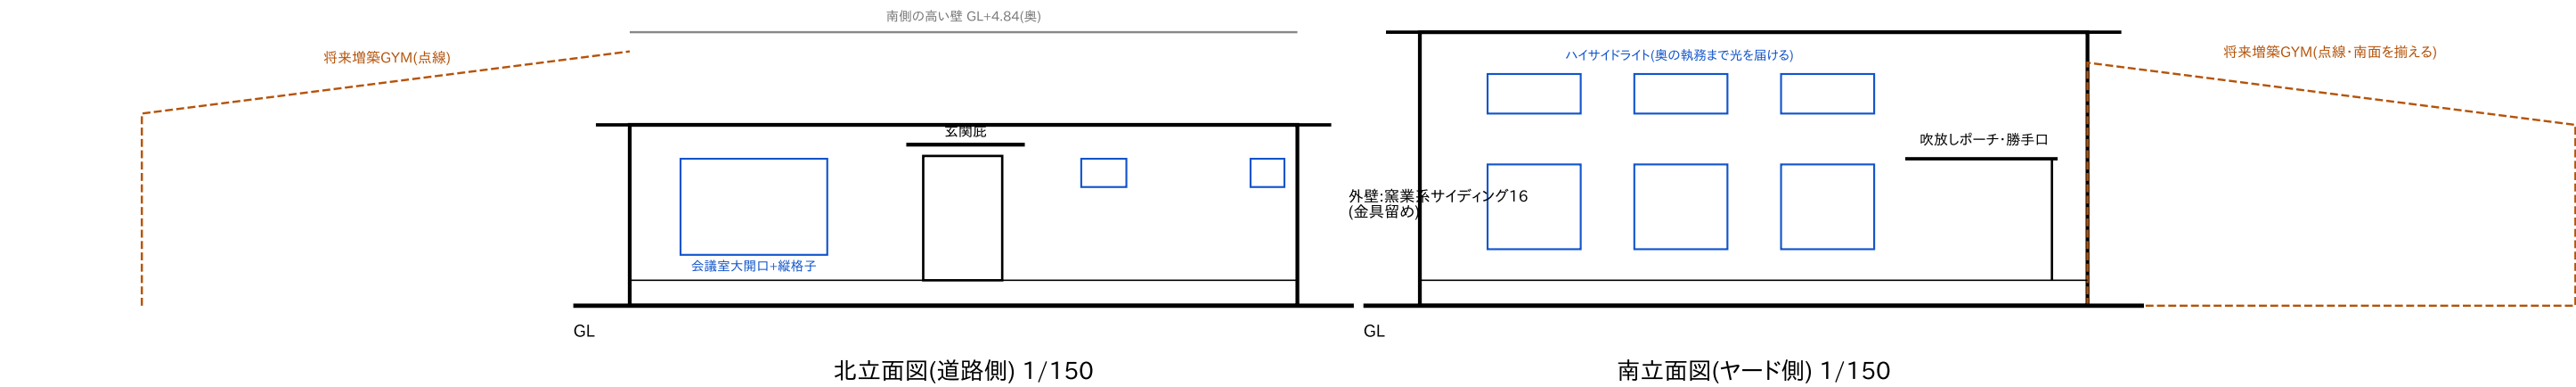

樋口工業有限公司 新社屋(事務所棟)新築工事
図面名: 立面図(4面) A-03
縮尺 1/150・2026-08-19・計画案v5(たたき台)

